ZONA D.V.	Nº TAL.	DATA PL.	ÁREA (ha)	VARIEDADE
999	1	05/2023	9.71	RB 975242
5.80 %	2		23.42	
TOTAL PLANTIO			33.13	--------

ÁREAS	(ha)	(%)
PLANTIO	33.13	93.66
CARREADORES	2.09	5.91
OUTROS	0.00	0.00
SUB TOTAL AGRICULTÁVEL	35.22	99.58
AP.P.	0.00	0.00
ÁRVORES	0.08	0.23
OUTROS	0.07	0.20
SUB TOTAL NÃO AGRICULT.	0.15	0.42
ÁREA TOTAL	35.37	100.00

C. NÍVEL:	2723.52 m/l	0.63 ha	1.77 %

LEGENDA

▬ FAZENDA	▬ CONFRONTANTE
▬ TALHÃO	‒ ‒ REDE ELÉTRICA
▪▪▪▪ CURVA DE NÍVEL	⇨ TRAJETO VAZIO
― CARREADOR	➞ TRAJETO CARREGADO

PLANTIO MANUAL - ESPAÇAMENTO: 1.50 X 1.50
TIRO MÉDIO ESTIMADO: 000.00m

Clealco
Açúcar, Etanol e Energia

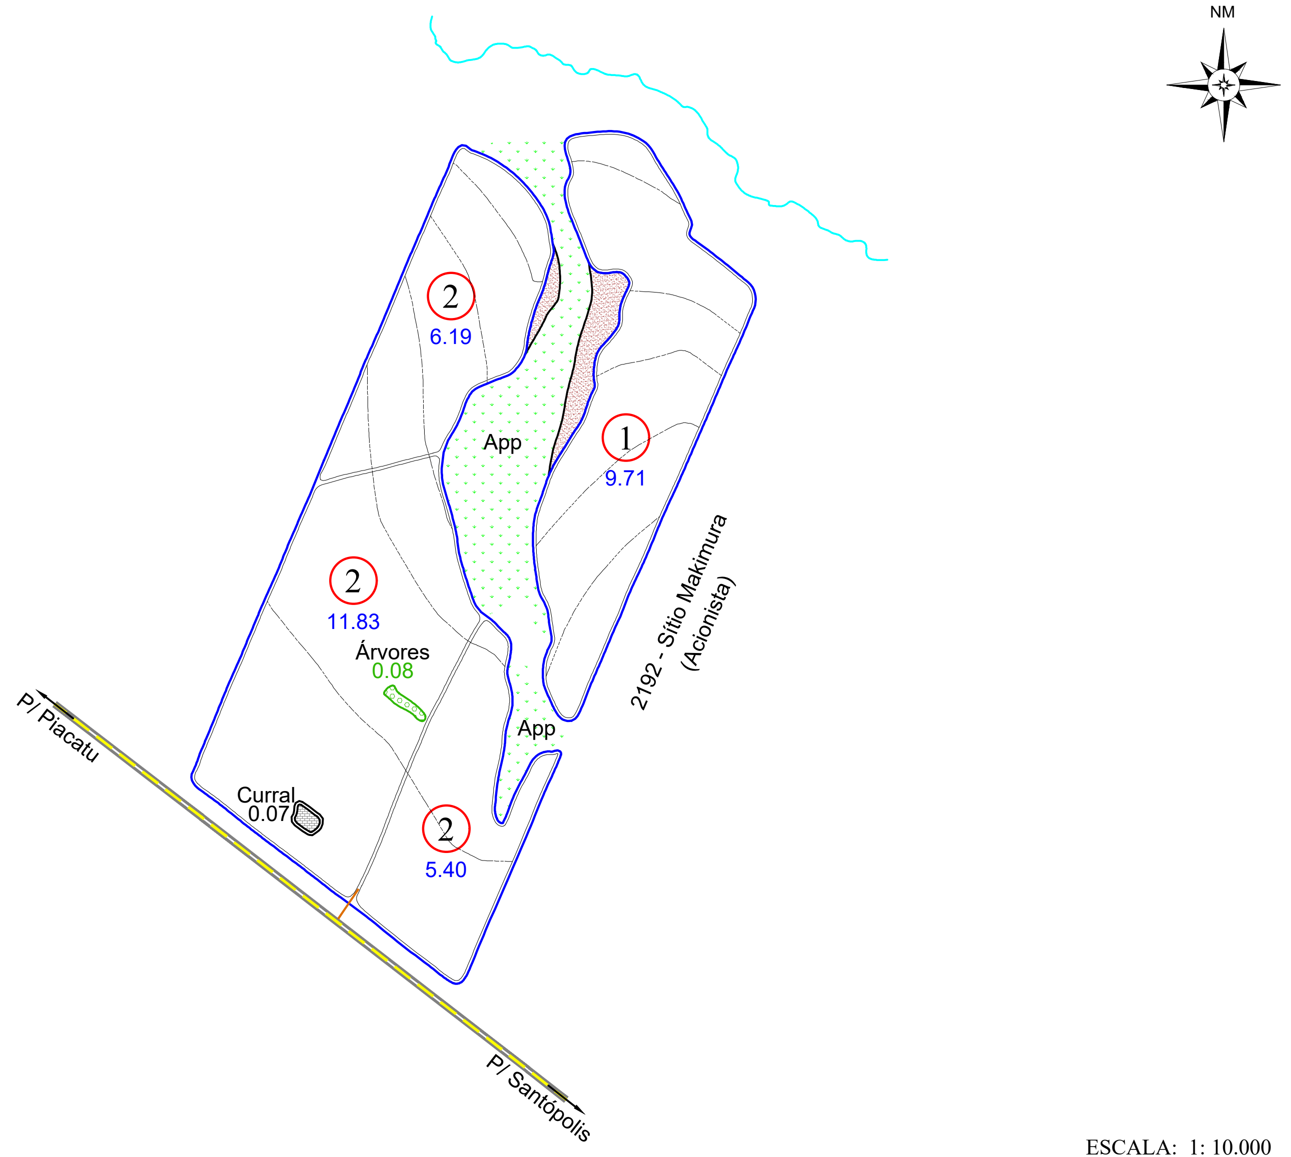

🟥 NÃO PLANTOU

ESCALA: 1: 10.000

CROQUI DE ACESSO

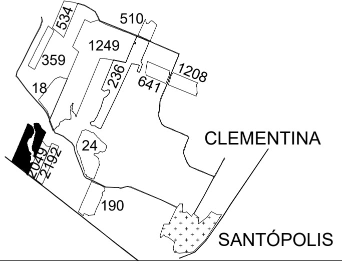

SÍTIO SÃO VALENTIM

PROPRIETÁRIO:	VERA LUCIA LEMES
COMPRADOR:	CLEALCO S/A
MUNICÍPIO:	SANTÓPOLIS DO AGUAPEÍ

DISTÂNCIAS (km):

UNID. I -	Asfalto:	18.50	Terra.:	1.00
UNID.I I -	Asfalto:	53.00	Terra.:	1.00
UNID. III -	Asfalto:	58.00	Terra.:	1.00

COORDENADAS:		
E(X): 547976.03	N(Y): 7609011.70
LAT: -21°37'16.8638"	LONG: -50°32'11.1627"

CLEALCO - AÇÚCAR E ALCOOL S/A - DEPARTAMENTO DE TOPOGRAFIA

UNIDADE:
I

PARTE:
A/A

FUNDO AGRÍCOLA:
307411

M:\03-Projetos (Sistematização, Pré, Pós e outros)\Terceiro\2023\Edvaldo\Pós Plantio\307411 - Sítio São Valentin (Vera Lucia Lemes) - Pos Plantio 2023.dwg

Bruno Gamboa 15/09/23