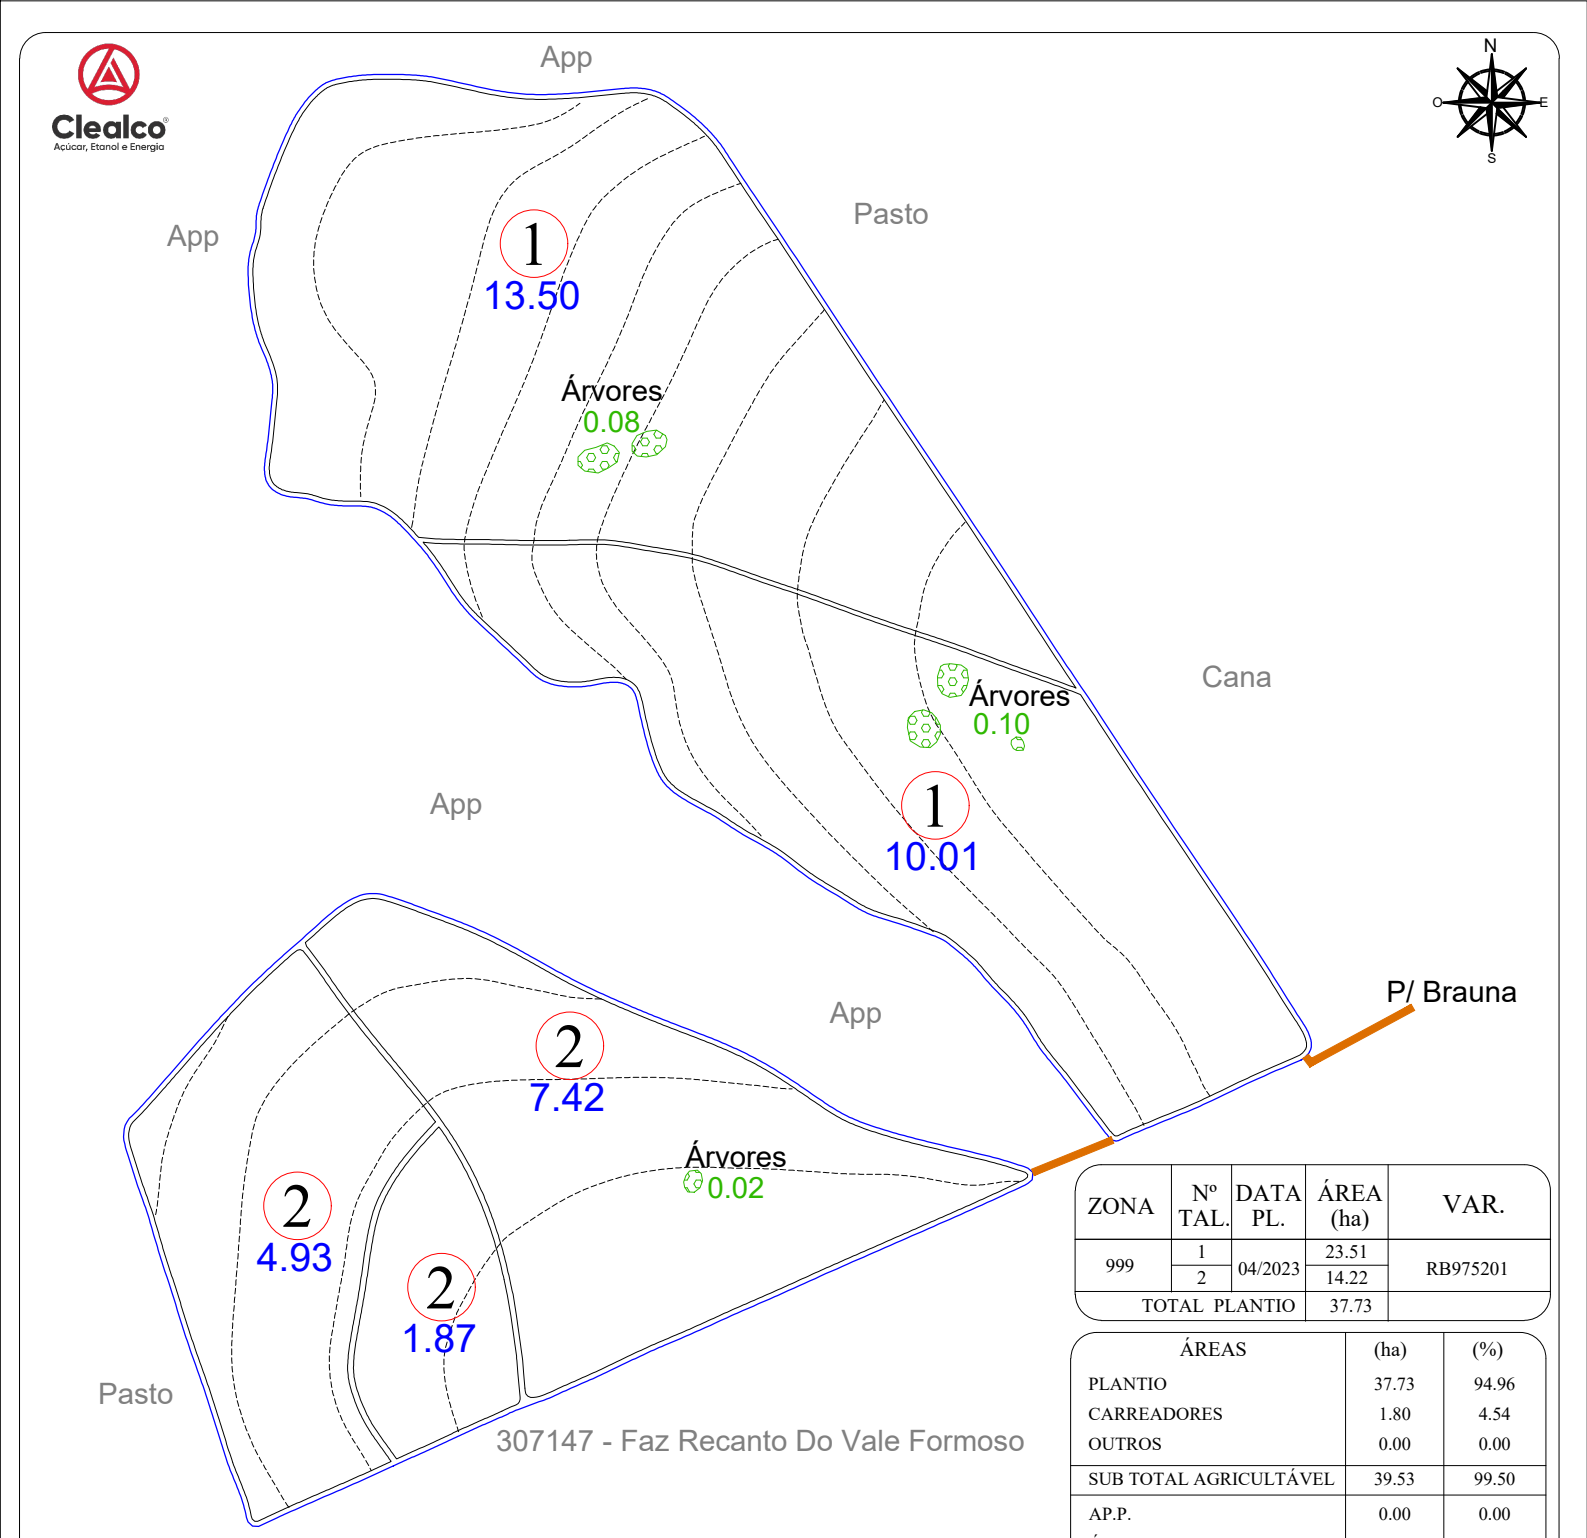


ZONA	Nº TAL.	DATA PL.	ÁREA (ha)	VAR.
999	1	04/2023	23.51	RB975201
	2		14.22	
TOTAL PLANTIO			37.73	

ÁREAS	(ha)	(%)
PLANTIO	37.73	94.96
CARREADORES	1.80	4.54
OUTROS	0.00	0.00
SUB TOTAL AGRICULTÁVEL	39.53	99.50
AP.P.	0.00	0.00
ÁRVORES	0.20	0.50
OUTROS	0.00	0.00
SUB TOTAL NÃO AGRICULT.	0.20	0.50
ÁREA TOTAL	39.73	100.00

C. NÍVEL: 0.00 m/l 0.00 ha 0.00 %

LEGENDA

- FAZENDA
- TALHÃO
- REDE ELÉTRICA
- VAZIO
- TERRAÇO BASE LARGA
- TERRAÇO EMBUTIDO
- (P.O.A) PATIO DE OPERAÇÃO
- CARREGADO

ESPAÇAMENTO: 1.50 x 1.50
TIRO MÉDIO ESTIMADO: 295.29m
D.V: 5.39%

ESCALA: 1: 5.500

CROQUI DE ACESSO



SÍTIO SÃO BRAZ

PROPRIETÁRIO: ANTONIO FLAVIO ARRIEIRO
COMPRADOR: CLEALCO
MUNICÍPIO: BRAÚNA

DISTÂNCIAS (km):
UNID. I - Asfalto: 8.50 Terra.: 8.00
UNID.I I - Asfalto: 64.50 Terra.: 8.00

COORDENADAS: E(X): 566201.70 N(Y): 7619507.39
LAT: -21°31'33.3980" LONG: -50°21'38.7100"

CLEALCO - AÇÚCAR E ALCOOL S/A - DEPARTAMENTO DE GEOTECNOLOGIA

LEVANTAMENTO VIA:
SATÉLITE
GPS / VANT
GOOGLE

UNIDADE: I
PARTE: A/A
FUNDO AGRÍCOLA: 307413

M:\01-Mapa de safra\Mapas Atualizados\Terceiro\307413 - Sítio São Braz (Antonio Flavio Arrieiro)\307413 - Sítio São Braz (Antonio Flavio Arrieiro).dwg

Bruno Gamboa 07/07/26