ZONA D.V.	Nº TAL.	DATA PL.	ÁREA (ha)	VARIEDADE
999 6.06 %	1	06/2023	20.03	RB 975242
TOTAL PLANTIO			20.03	--------

ÁREAS	(ha)	(%)
PLANTIO	20.03	85.47
CARREADORES	1.66	7.06
OUTROS	0.02	0.09
SUB TOTAL AGRICULTÁVEL	21.71	92.62
AP.P.	1.73	7.38
ÁRVORES	0.00	0.00
OUTROS	0.00	0.00
SUB TOTAL NÃO AGRICULT.	1.73	7.38
ÁREA TOTAL	23.44	100.00

C. NÍVEL:	1421.88 m/l	0.33 ha	1.40 %

LEGENDA

FAZENDA	CONFRONTANTE
TALHÃO	REDE ELÉTRICA
CURVA DE NÍVEL	TRAJETO VAZIO
CARREADOR	TRAJETO CARREGADO

PLANTIO MANUAL - ESPAÇAMENTO: 1.50 X 1.50
TIRO MÉDIO ESTIMADO: 128.04 m

Clealco
Açúcar, Etanol e Energia

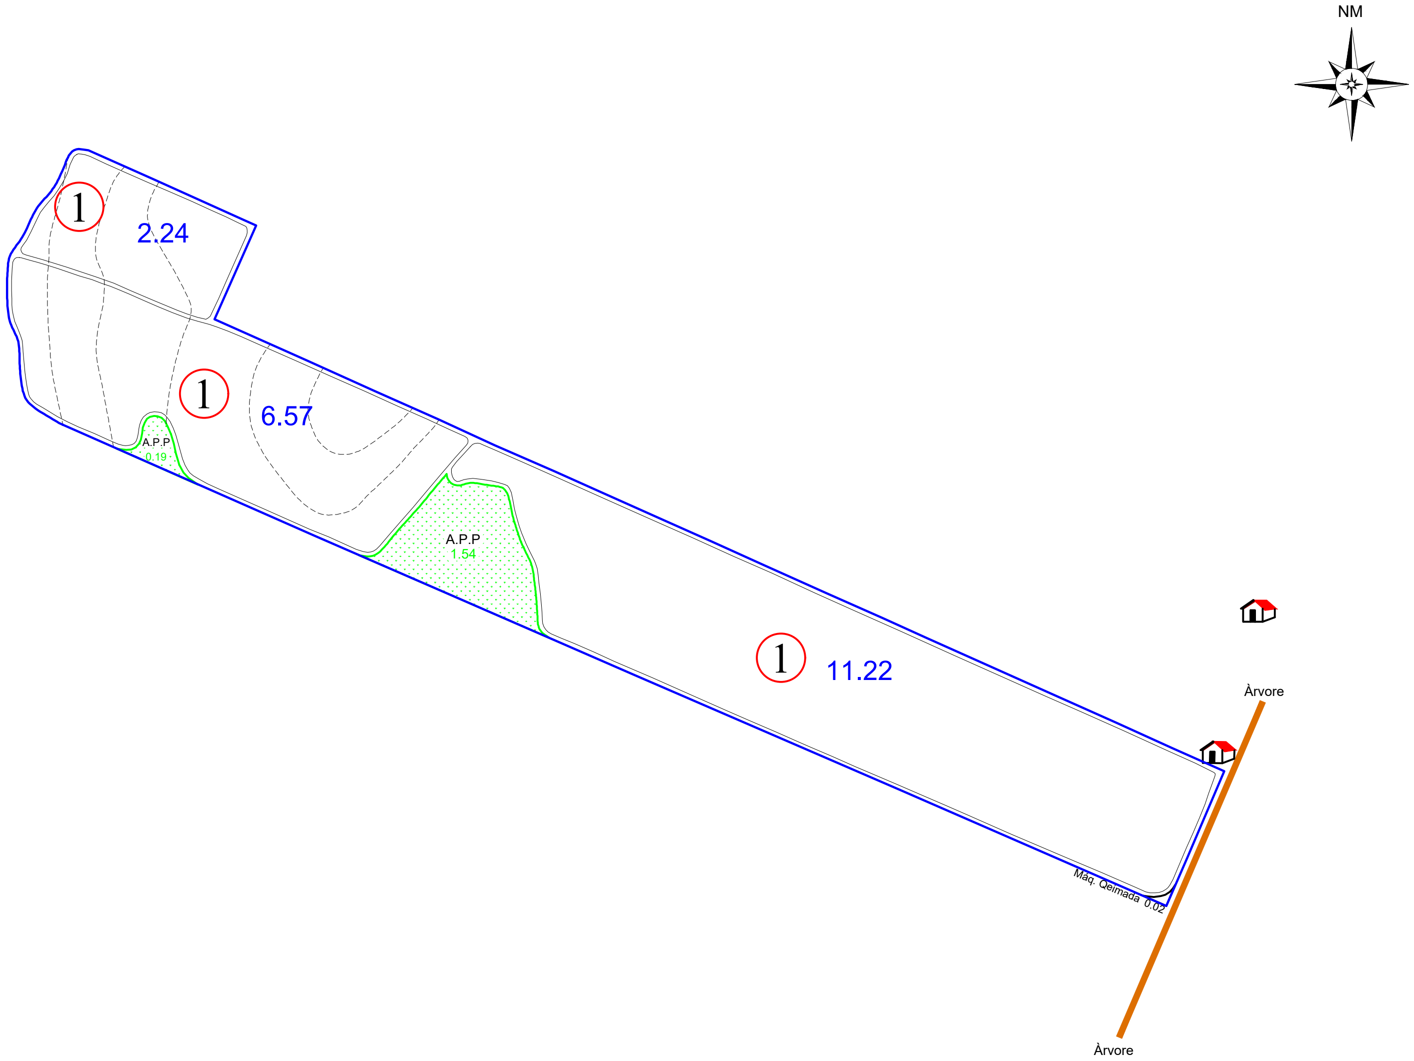
NM
1
2.24
1
6.57
A.P.P
0.19
A.P.P
1.54
1
11.22
Àrvore
Máq. Qeimada 0.02
Àrvore

ESCALA: 1: 10.000

CROQUI DE ACESSO

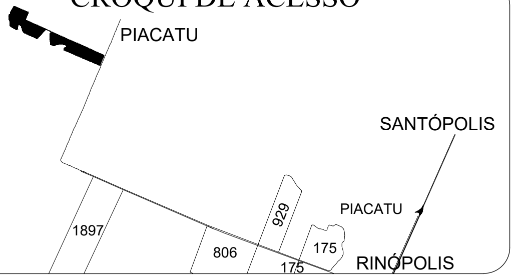
PIACATU
SANTÓPOLIS
PIACATU
1897
929
806
175
175
RINÓPOLIS

ESTÂNCIA ISABELA I

PROPRIETÁRIO: BRUNO MATEUS VENDRAME
COMPRADOR: CLEALCO S/A
MUNICÍPIO: PIACATU

DISTÂNCIAS (km):

UNID. I -	Asfalto:	20.00	Terra.:	1.00
UNID.I I -	Asfalto:	53.00	Terra.:	3.50
UNID. III -	Asfalto:	66.00	Terra.:	00.00

COORDENADAS: E(X): 543412.34 N(Y): 7609922.11
LAT: -21°36'47.6741" LONG: -50°34'49.9918"

CLEALCO - AÇÚCAR E ALCOOL S/A - DEPARTAMENTO DE TOPOGRAFIA

UNIDADE:
I

PARTE:
A/A

FUNDO AGRÍCOLA:
307415

M:\03-Projetos (Sistematização, Pré, Pós e outros)\Terceiro\2023\Edvaldo\Pós Plantio\307415 - Estancia Isabela I (Bruno Mateus Vendrame) - Pós Plantio 2023.dwg

Benati 22/03/2023