ZONA D.V.	Nº TAL.	DATA PL.	ÁREA (ha)	VAR.
2.76 %	1	04/2019	15.81	CTC4
	2		17.41	
	3		12.84	
	4		18.28	
	5		14.92	
	6	00/2024	38.35	VARIEDADE
	7		1.76	
	8		52.82	
	9		1.89	
	10	04/2022	19.46	CTC4
	11		18.36	
	12		22.25	
	13		28.42	
	14		20.98	
	15		22.86	
	16		9.35	
	17		16.52	
	18		12.36	
	19	04/2019	2.29	
	20		2.82	
	21	04/2023	11.33	CTC 9004
	22	04/2025	45.42	RB07 5322
TOTAL PLANTIO			406.50	--------


ÁREAS	(ha)	(%)
PLANTIO	406.50	95.97
CARREADORES	14.54	3.43
OUTROS	0.00	0.00
SUB TOTAL AGRICULTÁVEL	421.04	99.40
AP.P.	0.00	0.00
ÁRVORES	0.00	0.00
OUTROS	2.55	0.60
SUB TOTAL NÃO AGRICULT.	2.55	0.60
ÁREA TOTAL	423.59	100.00

C. NÍVEL: 32018.76 m/l 7.36 ha 1.74 %

LEGENDA


- FAZENDA
- TALHÃO
- CURVA DE NÍVEL
- CARREADOR
- CONFRONTANTE
- REDE ELÉTRICA
- TRAJETO VAZIO
- TRAJETO CARREGADO

PLANTIO MANUAL - ESPAÇAMENTO: 1.50 X 1.50
TIRO MÉDIO ESTIMADO: 521.50m

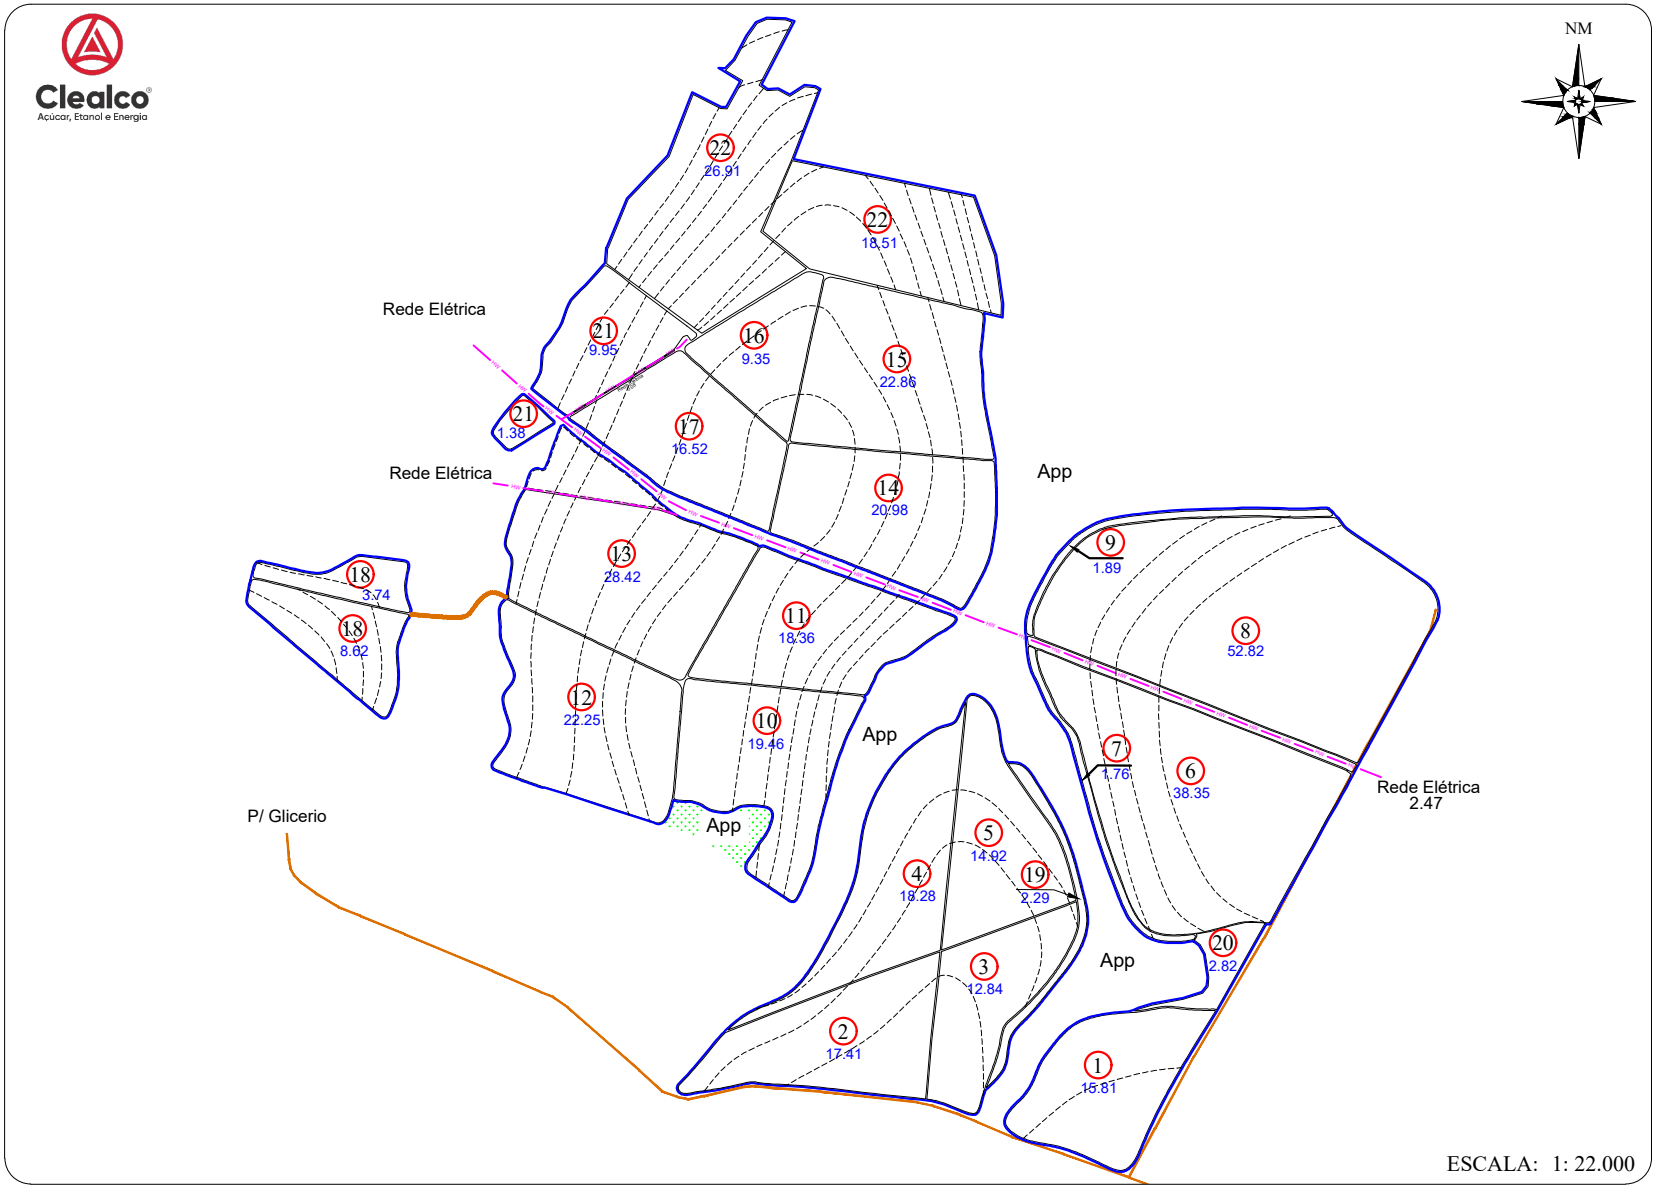

ESCALA: 1: 22.000

CROQUI DE ACESSO

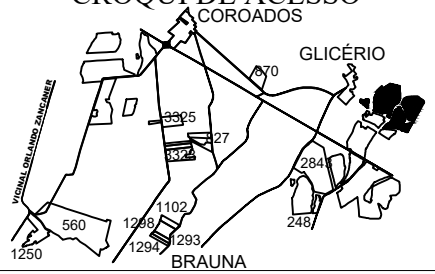

FAZENDA SANTA CATARINA

PROPRIETÁRIO: MARCELO CHAMIE HOUMSI
COMPRADOR: CLEALCO S/A
MUNICÍPIO: COROADOS

DISTÂNCIAS (km):
UNID. I - Asfalto: 43.09 Terra.: 11.09
UNID.I I - Asfalto: 67.50 Terra.: 2.00
UNID. III -Asfalto: 27.50 Terra.: 2.00

COORDENADAS: E(X): 585181.88 N(Y): 7634881.91
LAT: -21°23'10.4799" LONG: -50°10'41.7743"

CLEALCO - AÇÚCAR E ALCOOL S/A - DEPARTAMENTO DE TOPOGRAFIA

UNIDADE: I
PARTE: A/A
FUNDO AGRÍCOLA: 307423

M:\01-Mapa de safra\Mapas Atualizados\Terceiro\307423 - Fazenda Santa Catarina (Marcelo Chamie Houmsi)\307423 - Fazenda Santa Catarina - Marcelo Chamie Houmsi.dwg

Bruno Gamboa 03/02/26