ZONA DV	Nº TAL.	DATA PL.	ÁREA (ha)	VARIEDADE
999 3.70%	1	04/2022	46.21	CTC 04
TOTAL PLANTIO			46.21	--------

ÁREAS	(ha)	(%)
PLANTIO	46.21	95.46
CARREADORES	2.20	4.54
OUTROS	0.00	0.00
SUB TOTAL AGRICULTÁVEL	48.41	100.00
AP.P.	0.00	0.00
ÁRVORES	0.00	0.00
OUTROS	0.00	0.00
SUB TOTAL NÃO AGRICULT.	0.00	0.00
ÁREA TOTAL	48.41	100.00

C. NÍVEL:	3561.33 m/l	0.82 ha	1.69 %

LEGENDA

🟦 FAZENDA	▬ CONFRONTANTE
▬ TALHÃO	--- REDE ELÉTRICA
▪▪▪▪ CURVA DE NÍVEL	⇒ TRAJETO VAZIO
— CARREADOR	→ TRAJETO CARREGADO

PLANTIO MANUAL - ESPAÇAMENTO: 1.50 X 1.50
TIRO MÉDIO ESTIMADO: 264.83 m

Clealco
Açúcar, Etanol e Energia

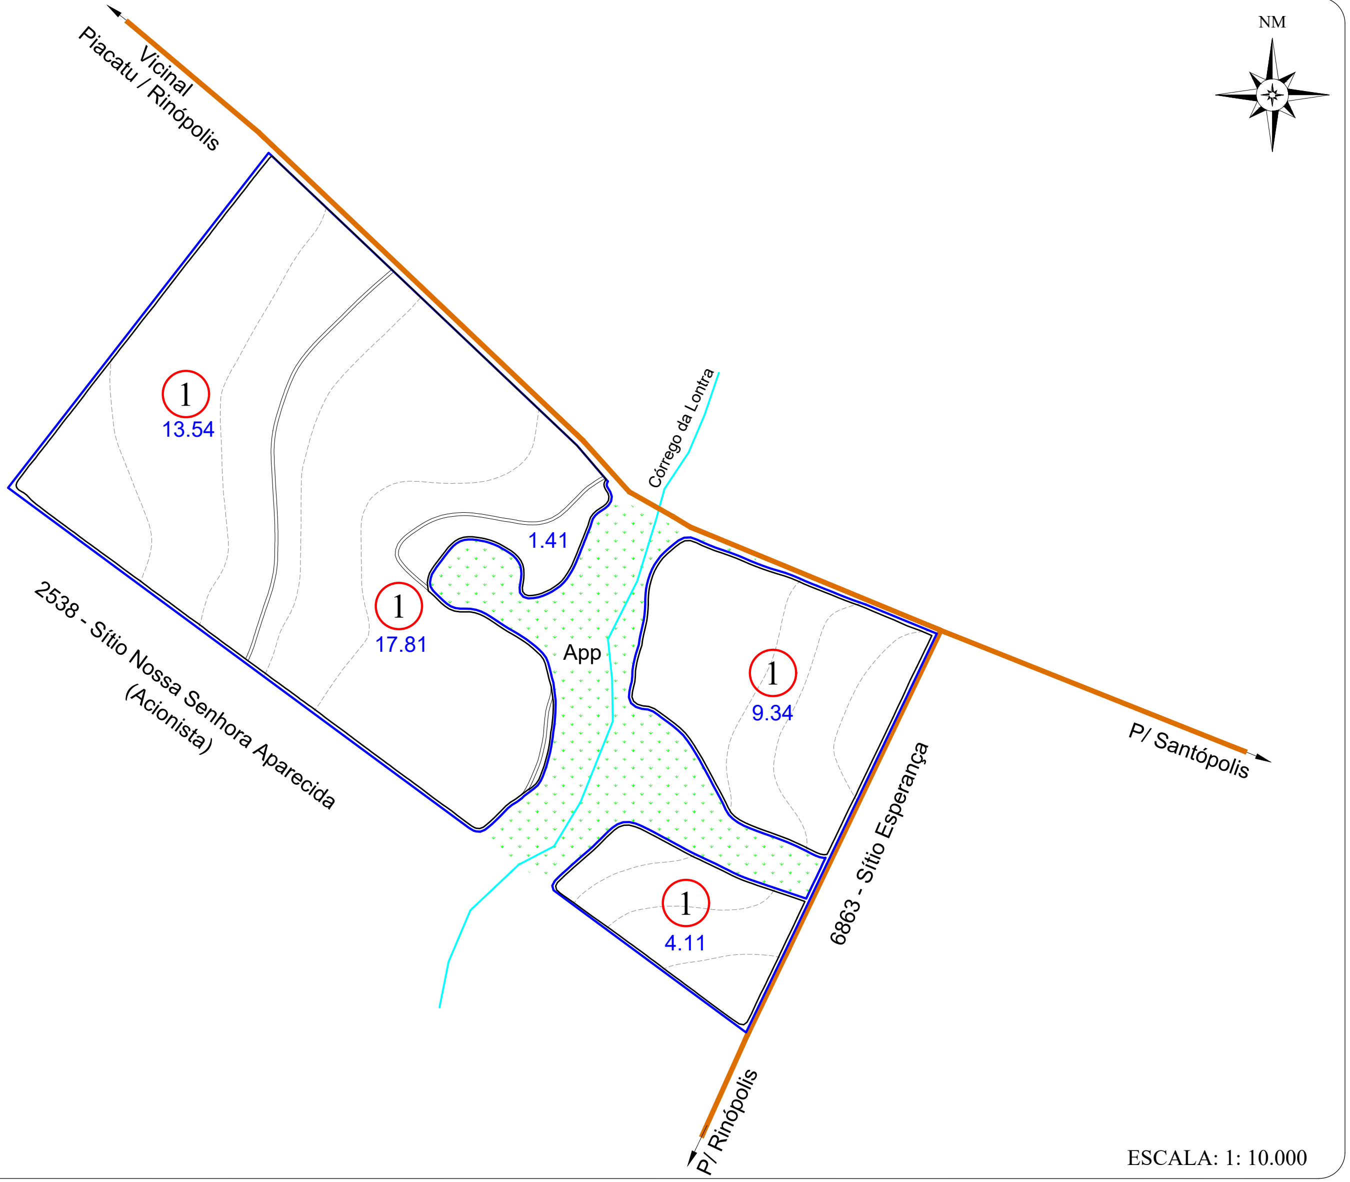

ESCALA: 1: 10.000

CROQUI DE ACESSO

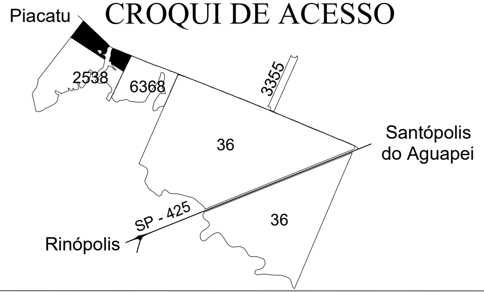

SÍTIO NOSSA SENHORA APARECIDA

PROPRIETÁRIO: JOSE HONORIO GASTALDI
COMPRADOR: CLEALCO S/A
MUNICÍPIO: IACRI

DISTÂNCIAS (km):

UNID. I -	Asfalto:	18.00	Terra.:	5.50
UNID.I I -	Asfalto:	50.00	Terra.:	5.50
UNID. III -	Asfalto:	61.00	Terra.:	5.50

COORDENADAS:	E(X): 540421.28	N(Y): 7606074.10
	LAT: -21°38'53.0844"	LONG: -50°36'33.6916"

CLEALCO - AÇÚCAR E ALCOOL S/A - DEPARTAMENTO DE TOPOGRAFIA

UNIDADE:
I
PARTE:
A/A
FUNDO AGRÍCOLA:
307425

M:\01-Mapa de safra\Mapas Atualizados\Terceiro\307425 - Sítio Nossa Senhora Aparecida (Jose Honorio Gastaldi)\307425 - Sítio Nossa Senhora Aparecida (Jose Honorio Gastaldi).dwg

Fernanda Bezerra 09/02/23