Clealco
Açúcar, Etanol e Energia


NÃO PLANTOU

Talhão	
1	0.70
2	0.38
3	0.28
5	0.41

Nº TAL.	DATA PL.	ÁREA (ha)	VARIEDADE
1	06/2023	18.12	RB97 5201
2		28.76	
3		18.42	
4		13.18	
5		32.41	
6	04/2024	40.75	
7	05/2025	19.62	
8		40.62	
TOTAL PLANTIO		211.88	

ÁREAS	(ha)	(%)
PLANTIO	211.88	93.22
CARREADORES	12.77	5.62
OUTROS	1.77	0.78
SUB TOTAL AGRICULTÁVEL	226.42	99.62
AP.P.	0.00	0.00
ÁRVORES	0.09	0.04
OUTROS	0.78	0.34
SUB TOTAL NÃO AGRICULT.	0.87	0.38
ÁREA TOTAL	227.29	100.00

C. NÍVEL: 19645.90 m/l 4.52 ha 1.99 %

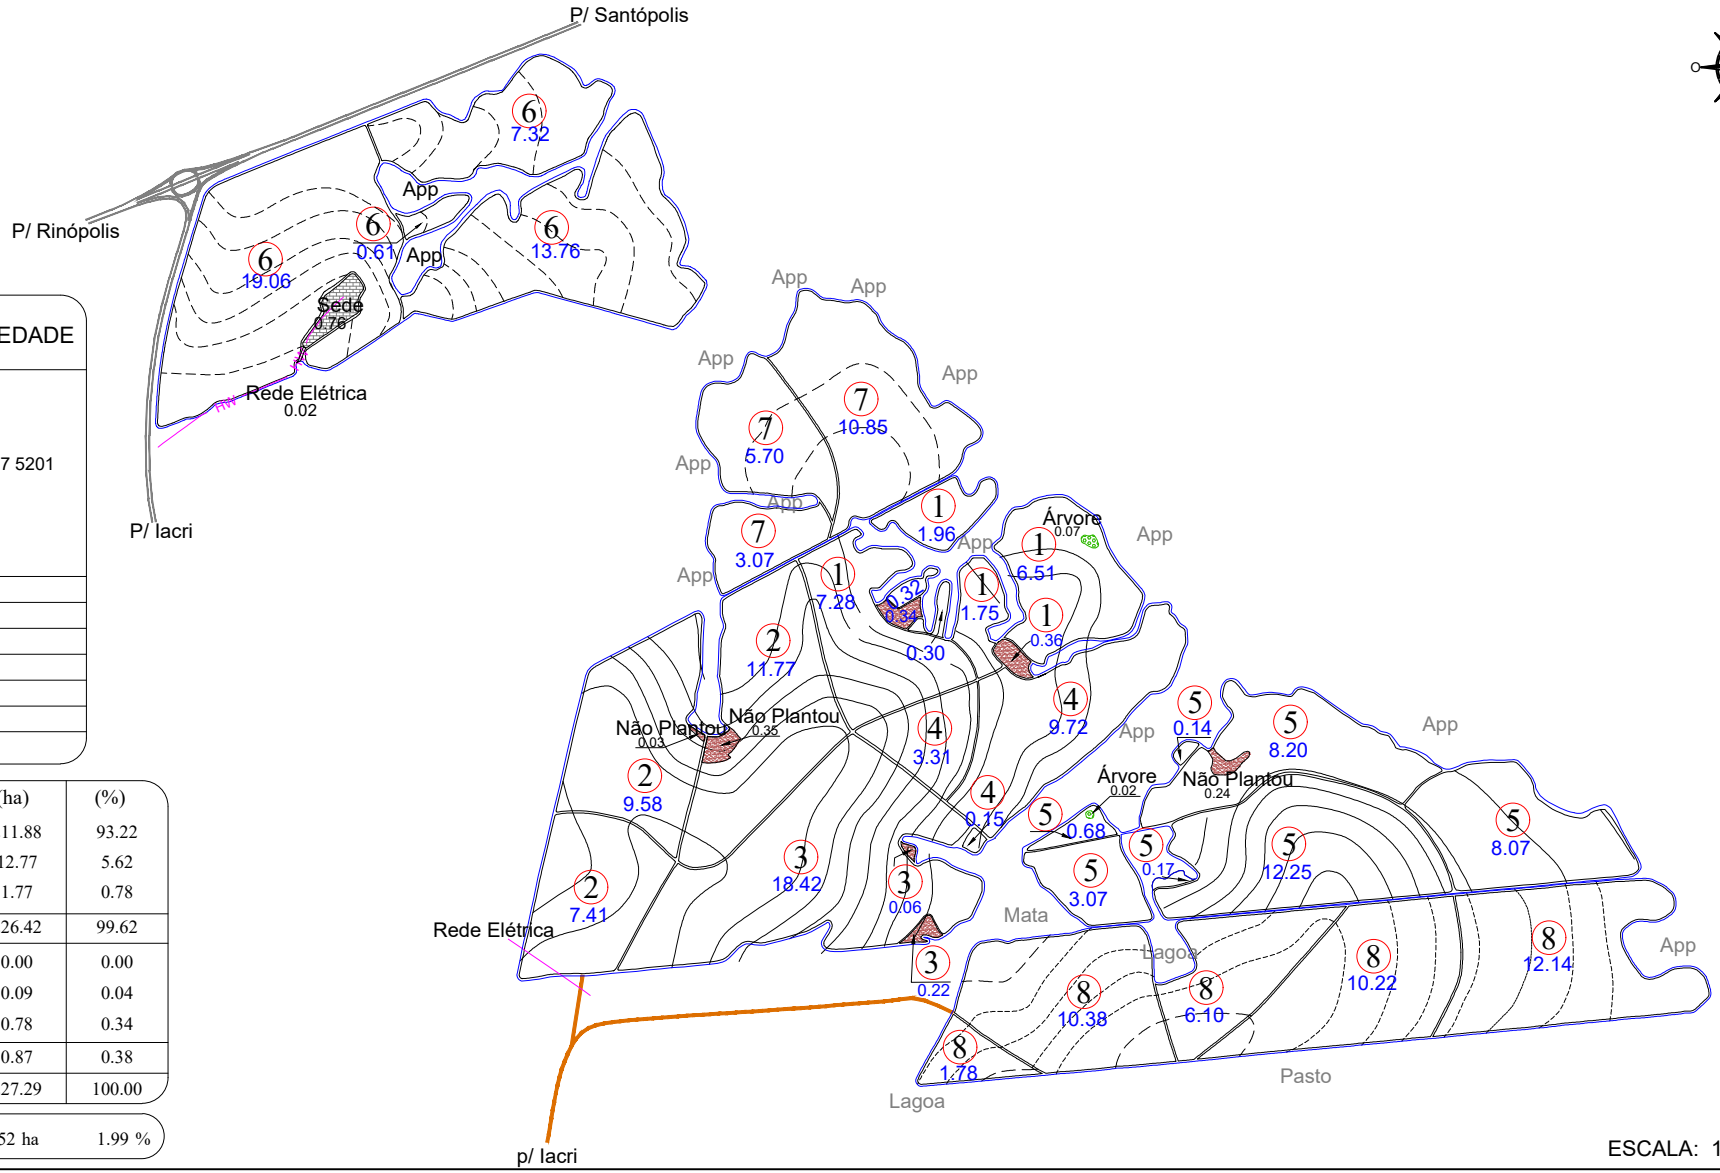


ESCALA: 1: 16.000

LEGENDA

- FAZENDA
- TALHÃO
- REDE ELÉTRICA
- TERRAÇO BASE LARGA
- TERRAÇO EMBUTIDO

ESPAÇAMENTO: 1.50 x 1.50 D.V: 5.93%
TIRO MÉDIO ESTIMADO: 213.46 m

CROQUI DE ACESSO

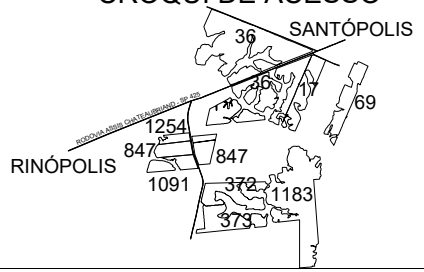

FAZENDA SÃO BENEDITO

PROPRIETÁRIO: VILMAR JOSÉ GASTALDI
COMPRADOR: CLEALCO
MUNICÍPIO: IACRI - SP

DISTÂNCIAS (km):
UNID. I - Asfalto: 26.00 Terra.: 1.00
UNID.I I - Asfalto: 60.00 Terra.: 1.00

COORDENADAS: E(X): 542935.13 N(Y): 7601818.60
LAT: -21°41'11.2820" LONG: -50°35'5.8371"
CLEALCO - AÇÚCAR E ALCOOL S/A - DEPARTAMENTO DE GEOTECNOLOGIA

LEVANTAMENTO VIA:
SATÉLITE
GPS / VANT
GOOGLE

UNIDADE: I
PARTE: A/A
FUNDO AGRÍCOLA: 307432

M:\01-Mapa de safra\Mapas Atualizados\Terceiro\307432 - Fazenda São Benedito (Vilmar José Gastaldi)\307432 - Fazenda São Benedito (Vilmar José Gastaldi).dwg

Bruno Gamboa 26/02/26