ZONA D.V.	Nº TAL.	DATA PL.	ÁREA (ha)	VARIEDADE
999 4.84%	1	05/2023	28.38	CV 7870
	2		40.05	
	3		12.95	
	4		10.24	
TOTAL PLANTIO			91.62	--------

ÁREAS	(ha)	(%)
PLANTIO	91.62	95.71
CARREADORES	4.10	4.29
OUTROS	0.00	0.00
SUB TOTAL AGRICULTÁVEL	95.72	100.00
AP.P.	0.00	0.00
ÁRVORES	0.00	0.00
OUTROS	0.00	0.00
SUB TOTAL NÃO AGRICULT.	0.00	0.00
ÁREA TOTAL	95.72	100.00

C. NÍVEL: 0.00 m/l 0.00 ha 0.00 %


LEGENDA

- FAZENDA
- TALHÃO
- CURVA DE NÍVEL
- CARREADOR
- CONFRONTANTE
- REDE ELÉTRICA
- TRAJETO VAZIO
- TRAJETO CARREGADO

PLANTIO MANUAL - ESPAÇAMENTO: 1.50 X 1.50
TIRO MÉDIO ESTIMADO: 252.48 m


Clealco
Açúcar, Etanol e Energia

NM

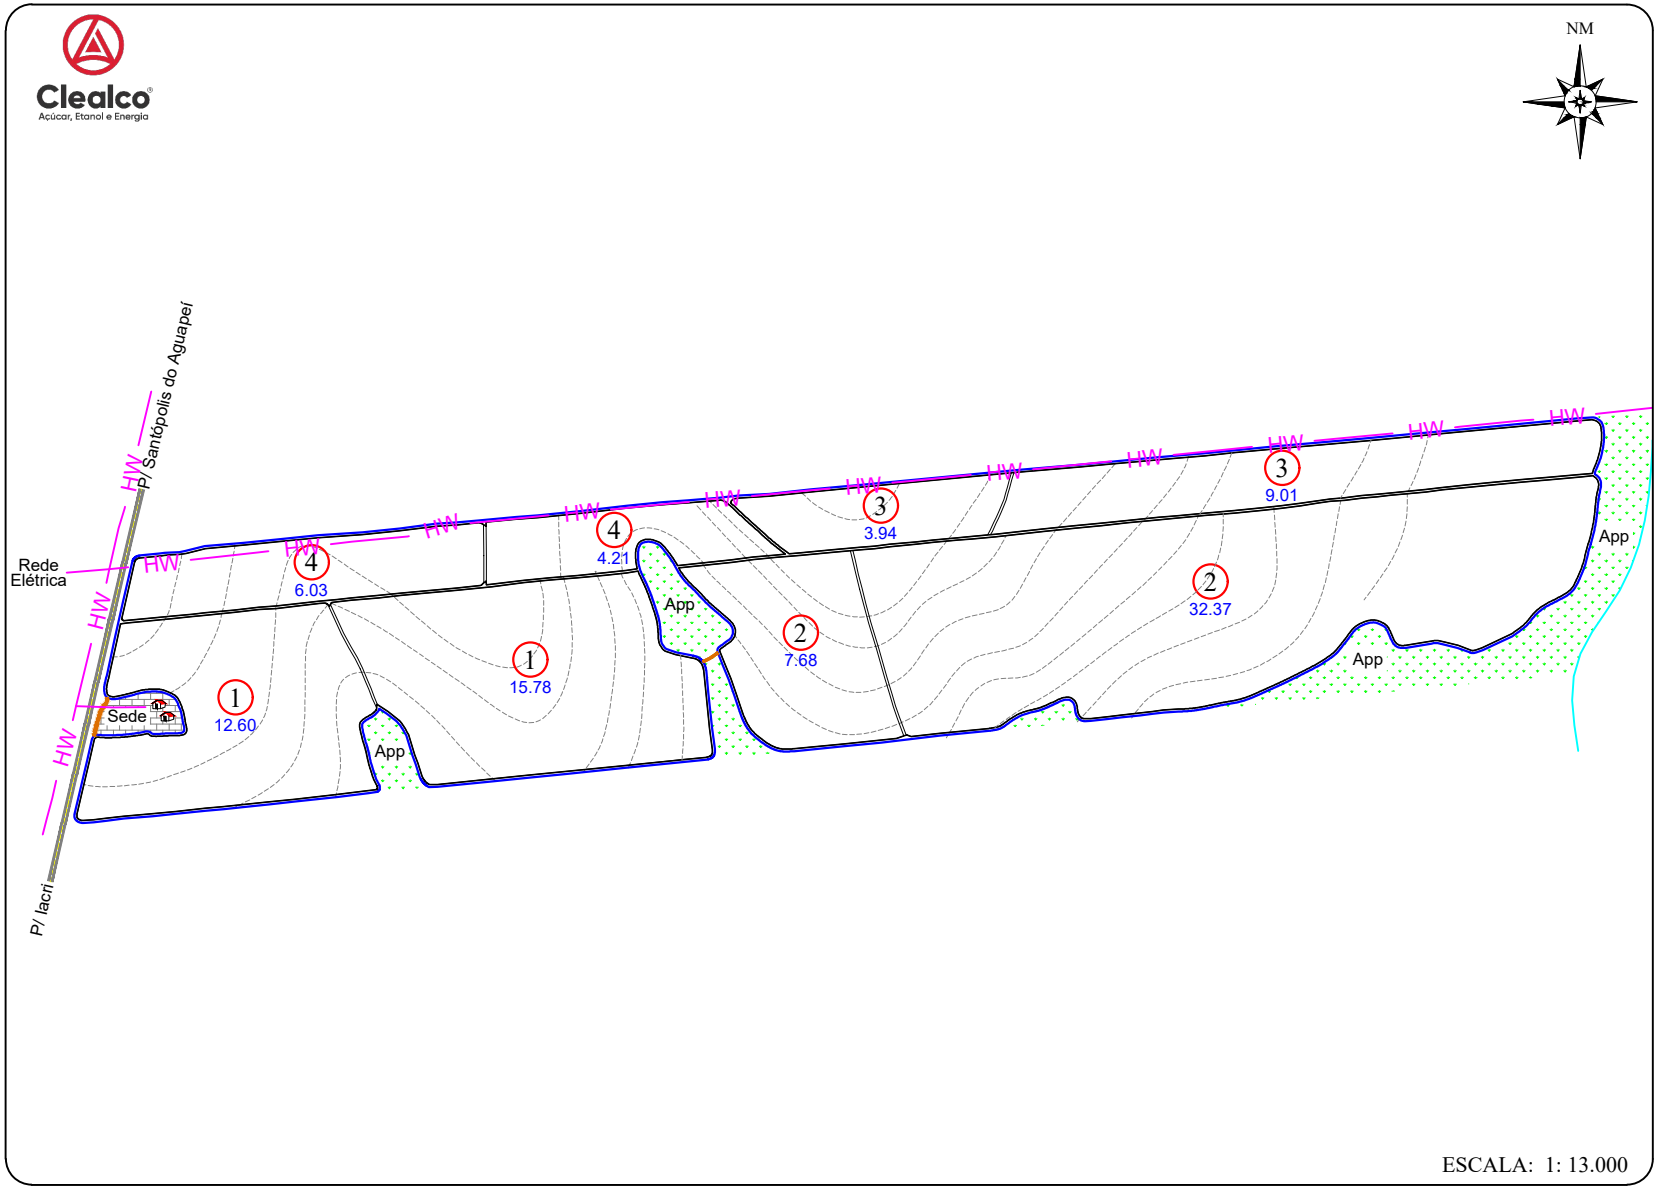

ESCALA: 1: 13.000

CROQUI DE ACESSO

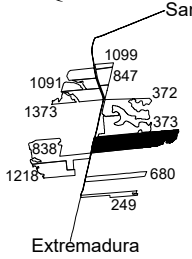

SÍTIO SANTA BÁRBARA

PROPRIETÁRIO: VILMAR JOSÉ GASTALDI
COMPRADOR: CLEALCO S/A
MUNICÍPIO: IACRI

DISTÂNCIAS (km):
UNID. I - Asfalto: 28.80 Terra.: 0.50
UNID.I I - Asfalto: 55.20 Terra.: 0.50
UNID. III -Asfalto: 71.00 Terra.: 0.50

COORDENADAS: E(X): 543134.88 N(Y): 7598245.60
LAT: -21°43'7.4754" LONG: -50°34'58.5511"

CLEALCO - AÇÚCAR E ALCOOL S/A - DEPARTAMENTO DE TOPOGRAFIA

UNIDADE: I
PARTE: A/A
FUNDO AGRÍCOLA: 307433