ZONA DV	Nº TAL.	DATA PL.	ÁREA (ha)	VARIEDADE
999 5.34%	1	06/2022	63.18	RB975201
TOTAL PLANTIO			63.18	--------

ÁREAS	(ha)	(%)
PLANTIO	63.18	94.12
CARREADORES	2.77	4.13
OUTROS	0.00	0.00
SUB TOTAL AGRICULTÁVEL	65.95	98.26
AP.P.	0.00	0.00
ÁRVORES	0.18	0.27
OUTROS	0.99	1.47
SUB TOTAL NÃO AGRICULT.	1.17	1.74
ÁREA TOTAL	67.12	100.00

C. NÍVEL:	0.00 m/l	0.00 ha	0.00 %

LEGENDA

▬ FAZENDA	▬ CONFRONTANTE
▬ TALHÃO	-·- REDE ELÉTRICA
▬ CURVA DE NÍVEL	→ TRAJETO VAZIO
— CARREADOR	→ TRAJETO CARREGADO

PLANTIO MANUAL - ESPAÇAMENTO: 1.50 X 1.50
TIRO MÉDIO ESTIMADO: 212.33 m

Clealco
Açúcar, Etanol e Energia

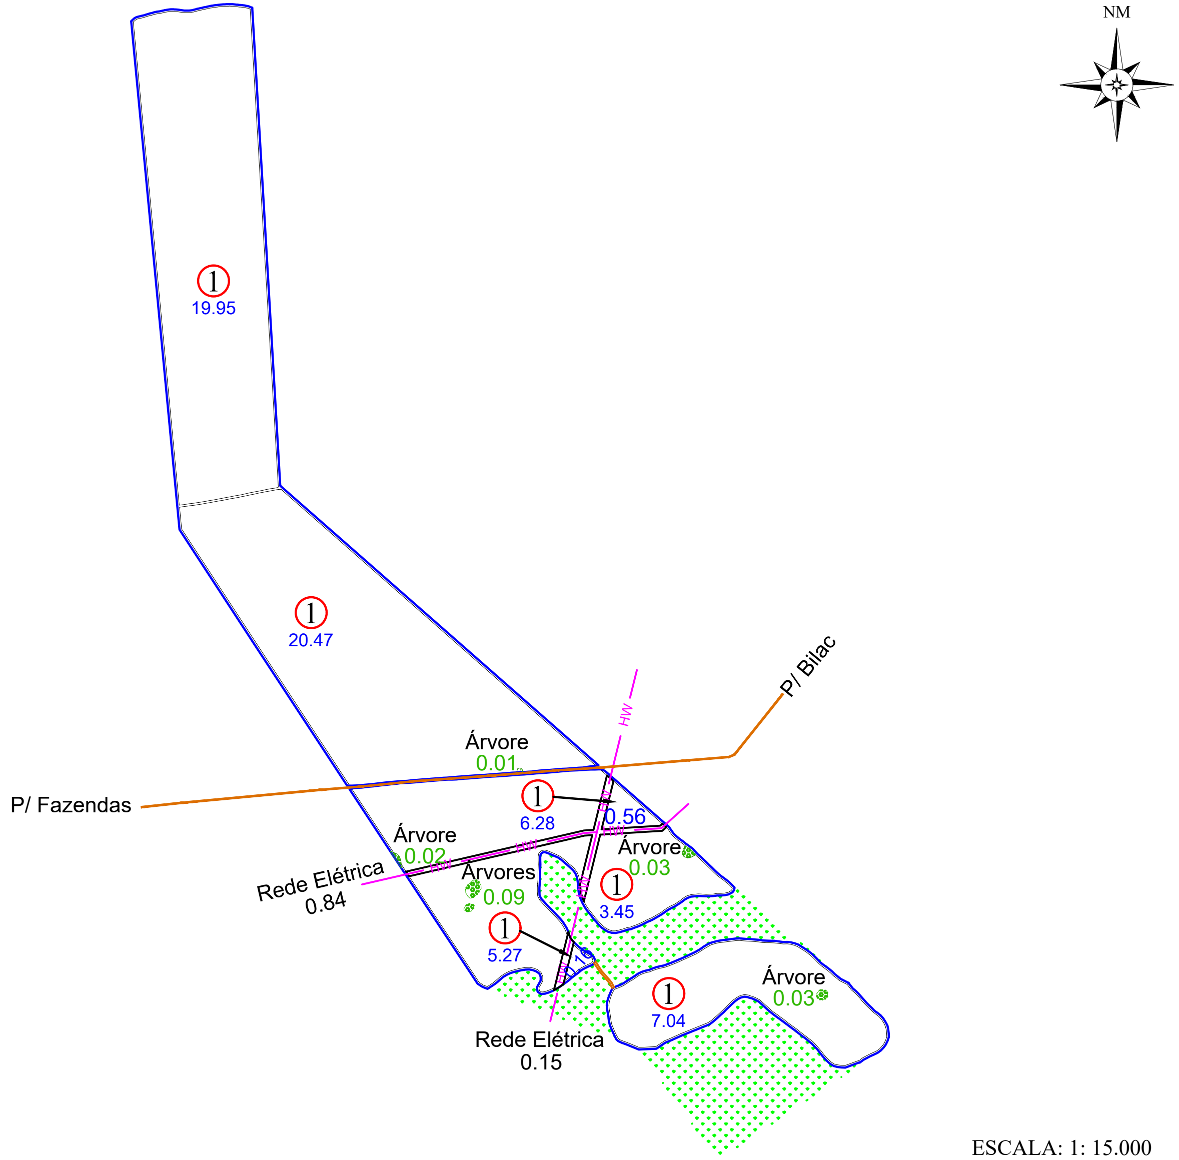
NM
1
19.95
1
20.47
P/ Bilac
HW
Árvore
0.01
P/ Fazendas
1
6.28
0.56
HW
Árvore
0.02
Árvore
0.03
Rede Elétrica
0.84
Árvores
0.09
1
3.45
1
5.27
0.16
1
7.04
Árvore
0.03
Rede Elétrica
0.15

ESCALA: 1: 15.000

CROQUI DE ACESSO

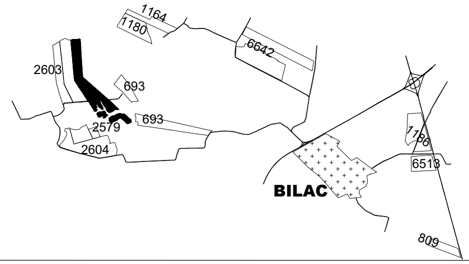
1164
1180
6642
2603
693
693
2579
2604
7186
6513
BILAC
809

SÍTIO JRS I

PROPRIETÁRIO: LUIZ CARLOS GENARI
COMPRADOR: CLEALCO S/A
MUNICÍPIO: BILAC

DISTÂNCIAS (km):

	Asfalto:		Terra.:	
UNID. I -	Asfalto:	26.00	Terra.:	6.00
UNID.I I -	Asfalto:	81.50	Terra.:	6.00
UNID. III -	Asfalto:	68.00	Terra.:	6.00

COORDENADAS: E(X): 548849.07 N(Y): 7634692.25
LAT: -21°23'21.5113" LONG: -50°31'43.4886"

CLEALCO - AÇÚCAR E ALCOOL S/A - DEPARTAMENTO DE TOPOGRAFIA

UNIDADE:
I

PARTE:
A/A

FUNDO AGRÍCOLA:
307440

M:\01-Mapa de safra\Mapas Atualizados\Terceiro\307440 - Sítio Jrs (Luis Carlos Genari)\307440 - Sítio Jrs (Luis Carlos Genari).dwg

Fabiano Castro 03/06/2023