

Clealco
Açúcar, Etanol e Energia

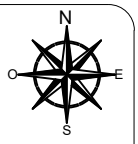

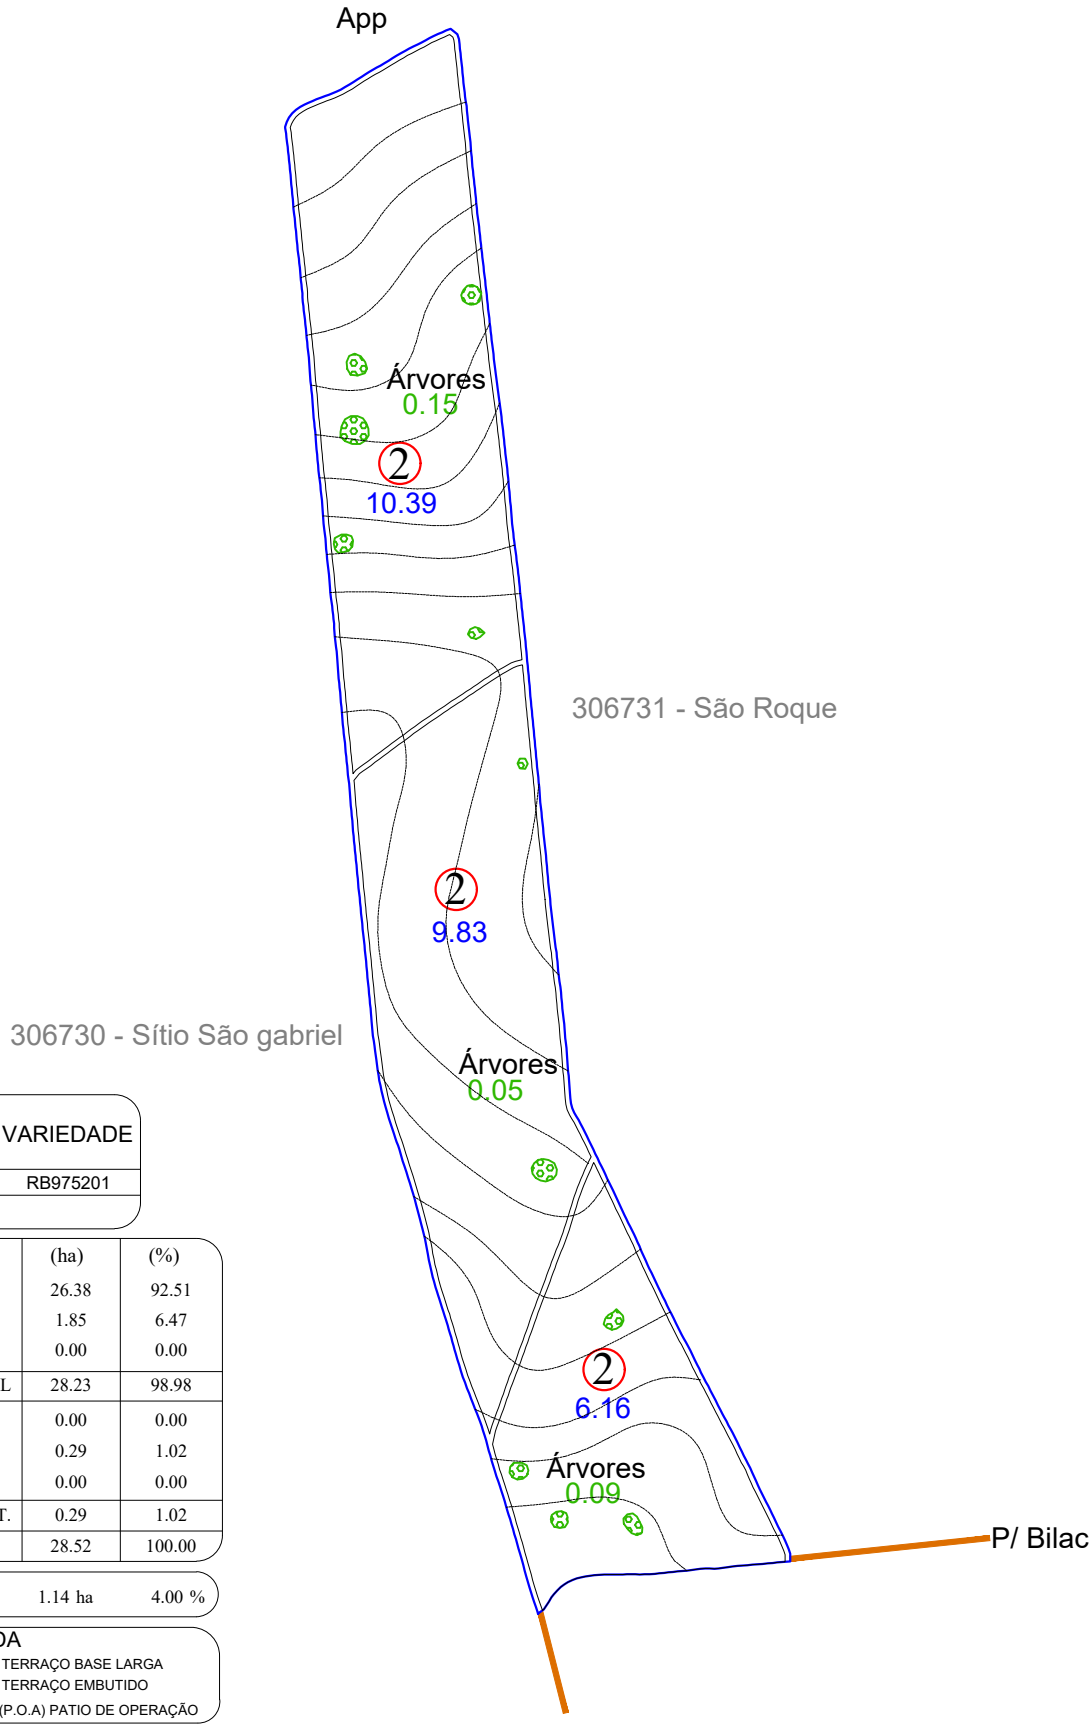

Nº TAL.	DATA PL.	ÁREA (ha)	VARIEDADE
2	06/2022	26.38	RB975201
TOTAL PLANTIO		26.38	

ÁREAS	(ha)	(%)
PLANTIO	26.38	92.51
CARREADORES	1.85	6.47
OUTROS	0.00	0.00
SUB TOTAL AGRICULTÁVEL	28.23	98.98
AP.P.	0.00	0.00
ÁRVORES	0.29	1.02
OUTROS	0.00	0.00
SUB TOTAL NÃO AGRICULT.	0.29	1.02
ÁREA TOTAL	28.52	100.00

C. NÍVEL: 4958.67 m/l 1.14 ha 4.00 %


LEGENDA

- FAZENDA
- TALHÃO
- REDE ELÉTRICA
- TERRAÇO BASE LARGA
- TERRAÇO EMBUTIDO
- (P.O.A) PATIO DE OPERAÇÃO

ESPAÇAMENTO: 1.50 x 1.50
TIRO MÉDIO ESTIMADO: 000.00 m
D.V: 0.00 %

ESCALA: 1: 7.500

CROQUI DE ACESSO

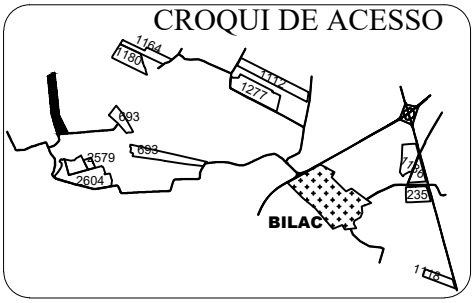

SÍTIO BOA VISTA

PROPRIETÁRIO: ANTONIO ROBERTO GENARI
COMPRADOR: CLEALCO S/A
MUNICÍPIO: ARAÇATUBA - SP

DISTÂNCIAS (km):
UNID. I - Asfalto: 26.00 Terra.: 6.00
UNID.I I - Asfalto: 81.50 Terra.: 6.00

COORDENADAS: E(X): 547560.80 N(Y): 7635563.01
LAT: -21°22'53.3129" LONG: -50°32'28.3170"

CLEALCO - AÇÚCAR E ALCOOL S/A - DEPARTAMENTO DE GEOTECNOLOGIA

LEVANTAMENTO VIA:
- SATÉLITE
- GPS / VANT
- GOOGLE

UNIDADE: I
PARTE: B/B
FUNDO AGRÍCOLA: 307441

M:\01-Mapa de safra\Mapas Atualizados\Terceiro\307441 - Sitio Boa Vista (Antonio Roberto Genari)\307441 A e B - Sitio Boa Vista (Antonio Roberto Genari).dwg

Peteson Santos 00/00/25