
Clealco
Açúcar, Etanol e Energia

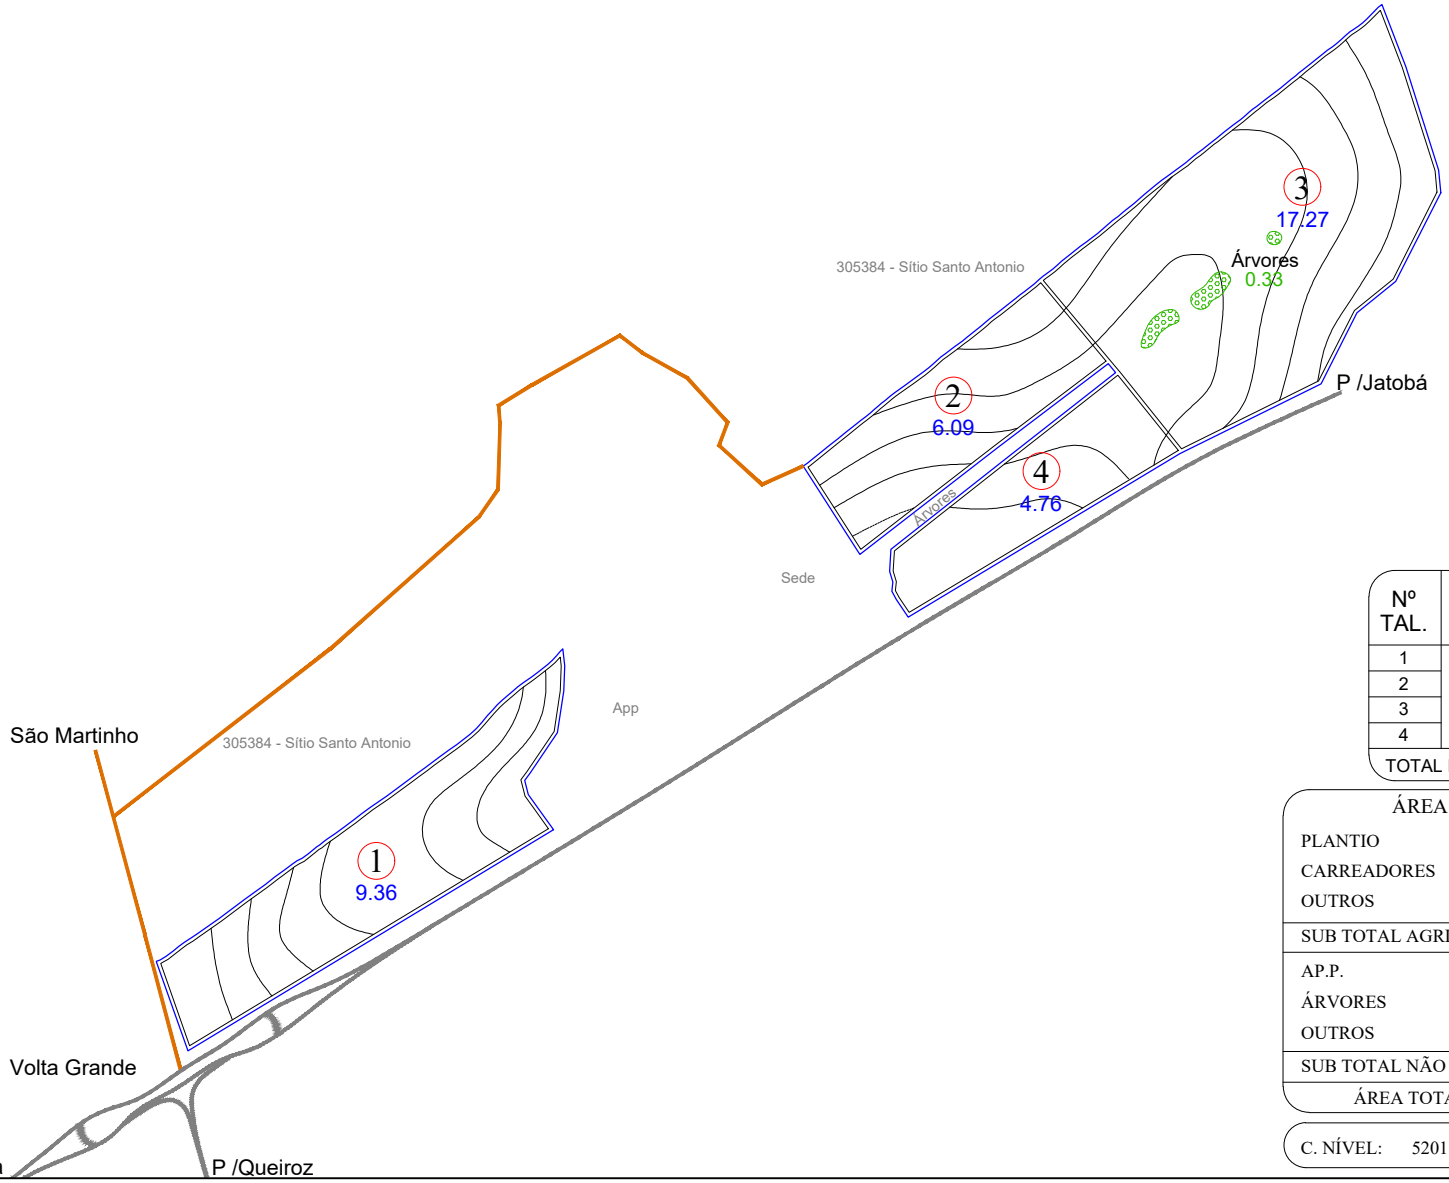

ESCALA: 1: 11.000

Nº TAL.	DATA PL.	ÁREA (ha)	VARIEDADE
1	04/2022	9.36	CTC 04
2		6.09	
3		17.27	
4		4.76	
TOTAL PLANTIO		37.48	


ÁREAS	(ha)	(%)
PLANTIO	37.48	92.47
CARREADORES	2.72	6.72
OUTROS	0.00	0.00
SUB TOTAL AGRICULTÁVEL	40.20	99.19
AP.P.	0.00	0.00
ÁRVORES	0.33	0.81
OUTROS	0.00	0.00
SUB TOTAL NÃO AGRICULT.	0.33	0.81
ÁREA TOTAL	40.53	100.00

C. NÍVEL: 5201.62 m/l 1.20 ha 2.95 %

LEGENDA
- FAZENDA
- TALHÃO
- REDE ELÉTRICA
- TERRAÇO BASE LARGA
- TERRAÇO EMBUTIDO
- VAZIO
- CARREGADO

ESPAÇAMENTO: 1.50 x 1.50
TIRO MÉDIO ESTIMADO: 214.05m
D.V: 5.09 %

CROQUI DE ACESSO

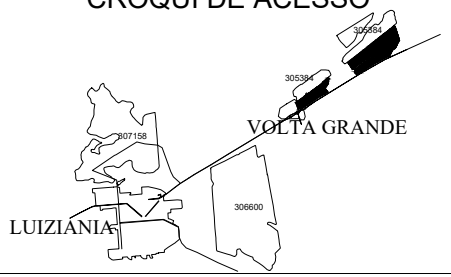

SITIO SÃO SEBASTIÃO

PROPRIETÁRIO: VICTOR BARRETO ROSSI
COMPRADOR: CLEALCO
MUNICÍPIO: LUIZIÂNIA - SP

DISTÂNCIAS (km):
UNID. I - Asfalto: 35.00 Terra.: 0.50
UNID.I I - Asfalto: 24.00 Terra.: 2.00

COORDENADAS: E(X): 572686.37 N(Y): 7605038.07
LAT: -21°39'23.0866" LONG: -50°17'51.0342"
CLEALCO - AÇÚCAR E ALCOOL S/A - DEPARTAMENTO DE GEOTECNOLOGIA

LEVANTAMENTO VIA:
SATÉLITE
GPS / VANT
GOOGLE

UNIDADE: I
PARTE: A/A
FUNDO AGRÍCOLA: 307442

M:\01-Mapa de safra\Mapas Atualizados\Terceiro\307442 - Sítio São Sebastião (Victor Barreto Rossi)\307442 - Sítio São Sebastião (Victor Barreto Rossi).dwg

Bruno Gamboa 27/05/26