ZONA DV	Nº TAL.	DATA PL.	ÁREA (ha)	VARIEDADE
999	1	04/2022	5.39	RB 975201
5.56 %	2		10.91	
TOTAL PLANTIO			16.30	--------

ÁREAS	(ha)	(%)
PLANTIO	16.30	92.16
CARREADORES	1.37	7.72
OUTROS	0.00	0.00
SUB TOTAL AGRICULTÁVEL	17.67	99.89
AP.P.	0.00	0.00
ÁRVORES	0.02	0.11
OUTROS	0.00	0.00
SUB TOTAL NÃO AGRICULT.	0.02	0.11
ÁREA TOTAL	17.69	100.00

C. NÍVEL: 3186.56 m/l 0.73 ha 4.14 %

LEGENDA

▬ FAZENDA	▬ CONFRONTANTE
▬ TALHÃO	-·- REDE ELÉTRICA
▪▪▪ CURVA DE NÍVEL	⇨ TRAJETO VAZIO
— CARREADOR	→ TRAJETO CARREGADO

PLANTIO MANUAL - ESPAÇAMENTO: 1.50 X 1.50
TIRO MÉDIO ESTIMADO: 172.82 m

Clealco
Açúcar, Etanol e Energia

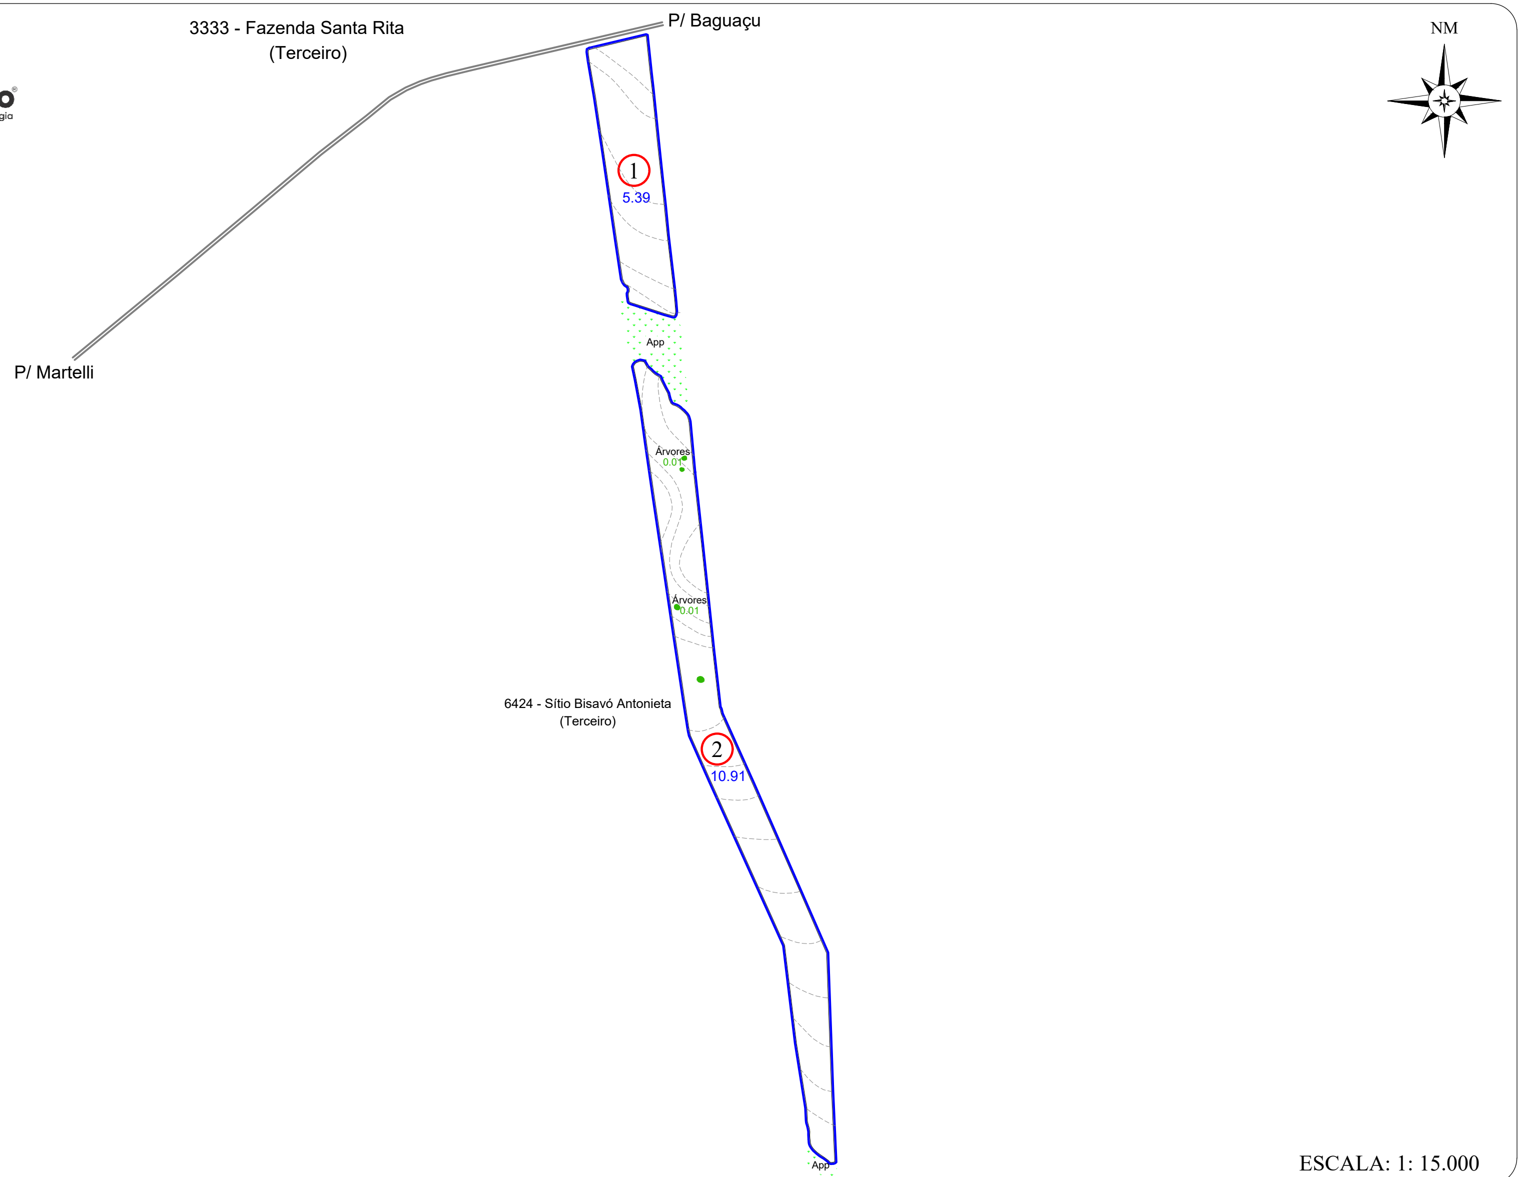

ESCALA: 1: 15.000

CROQUI DE ACESSO

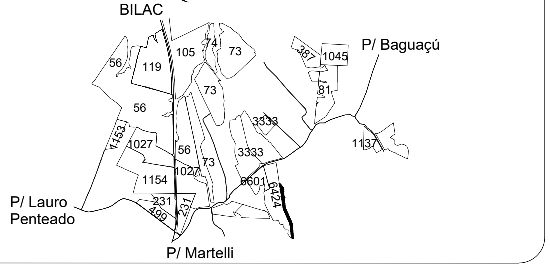

SÍTIO SANTA ROSA

PROPRIETÁRIO:	PAULO BENTO BOGO
ARRENDATÁRIO:	CLEALCO S/A
MUNICÍPIO:	CLEMENTINA

DISTÂNCIAS (km):

	Asfalto:		Terra.:	
UNID. I -	Asfalto:	10.50	Terra.:	1.00
UNID.I I -	Asfalto:	69.50	Terra.:	1.00
UNID. III -	Asfalto:	55.00	Terra.:	1.00

COORDENADAS: E(X): 562217.39 N(Y): 7620839.30
LAT: -21°30'50.5928" LONG: -50°23'57.3839"

CLEALCO - AÇÚCAR E ALCOOL S/A - DEPARTAMENTO DE TOPOGRAFIA

UNIDADE:
I

PARTE:
A/A

FUNDO AGRÍCOLA:
307444

M:\01-Mapa de safra\Mapas Atualizados\Terceiro\307444 - Sítio Santa Rosa (Paulo Bento Bogo)\307444 - Sítio Santa Rosa (Paulo Bento Bogo) - 2024.dwg

Fernanda Bezerra 20/02/23