ZONA D.V.	Nº TAL.	DATA PL.	ÁREA (ha)	VARIEDADE
999 6.15 %	1	04/2022	16.36	RB 975201
TOTAL PLANTIO			16.36	--------

ÁREAS	(ha)	(%)
PLANTIO	16.36	94.49
CARREADORES	0.84	4.87
OUTROS	0.00	0.00
SUB TOTAL AGRICULTÁVEL	17.20	99.36
AP.P.	0.00	0.00
ÁRVORES	0.11	0.64
OUTROS	0.00	0.00
SUB TOTAL NÃO AGRICULT.	0.11	0.64
ÁREA TOTAL	17.31	100.00

C. NÍVEL: 1808.79 m/l 0.42 ha 2.40 %

LEGENDA

FAZENDA	CONFRONTANTE
TALHÃO	REDE ELÉTRICA
CURVA DE NÍVEL	TRAJETO VAZIO
CARREADOR	TRAJETO CARREGADO

PLANTIO MANUAL - ESPAÇAMENTO: 1.50 X 1.50
TIRO MÉDIO ESTIMADO: 205.91 m

Clealco
Açúcar, Etanol e Energia

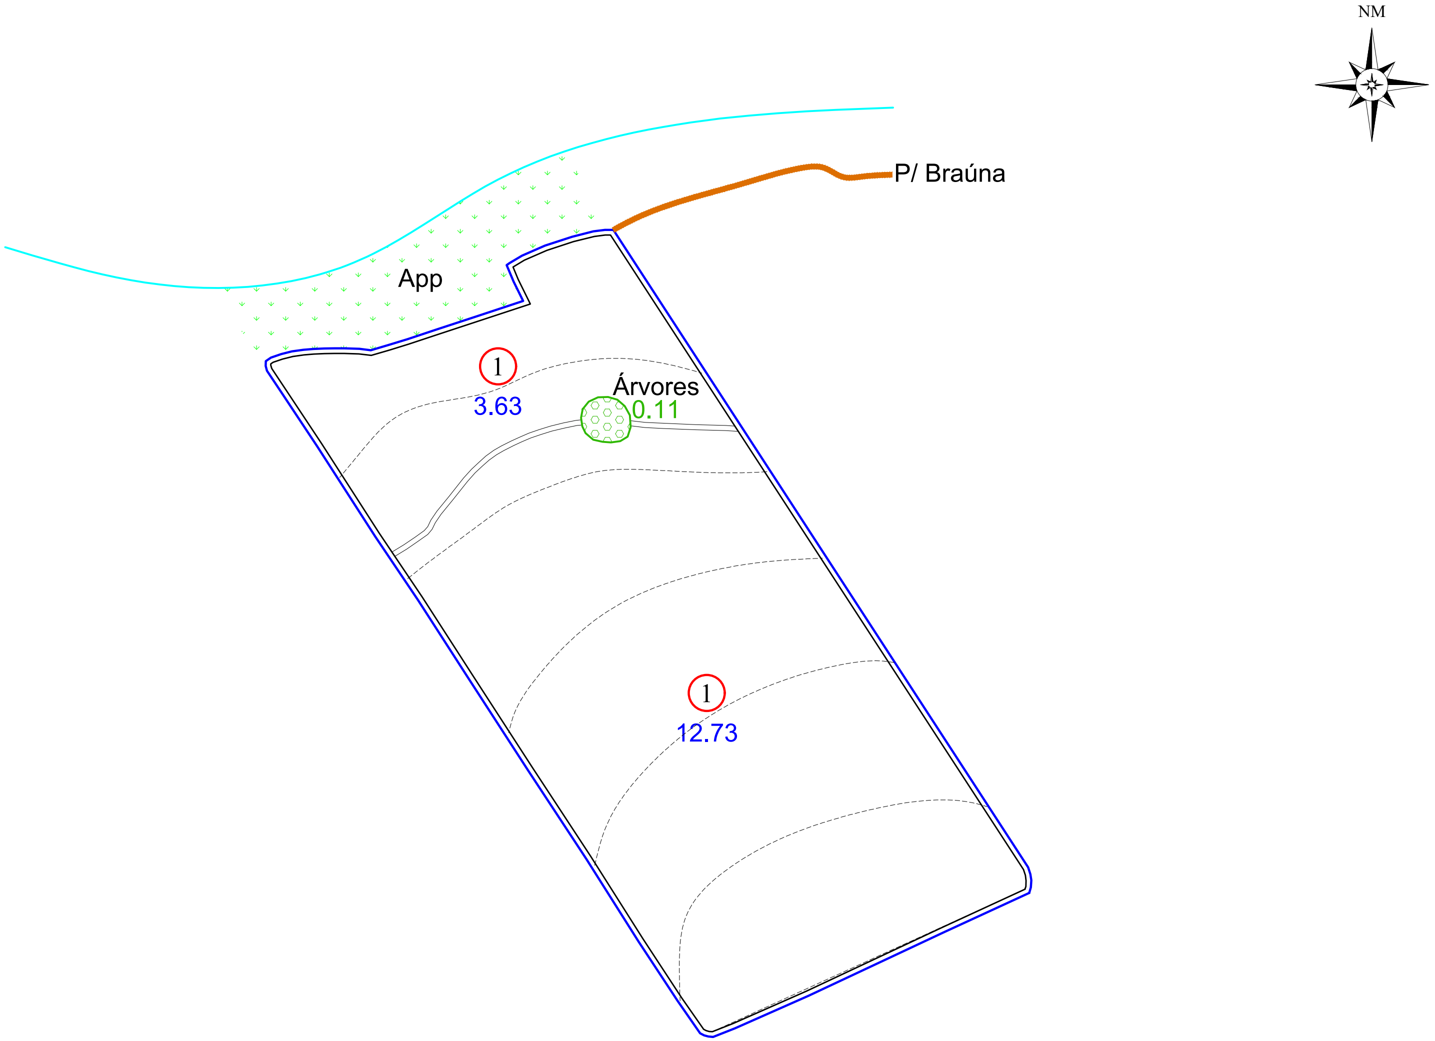

ESCALA: 1: 6.000

CROQUI DE ACESSO

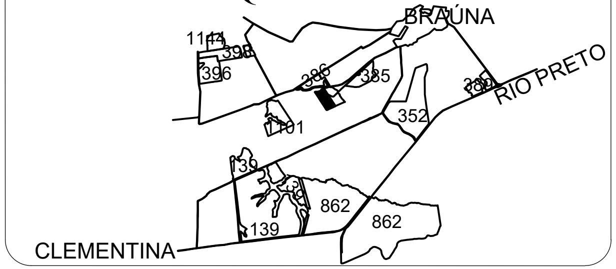

SÍTIO SANTA CLARA II

PROPRIETÁRIO: VALTER ANTONIO BOSCO
COMPRADOR: CLEALCO S/A
MUNICÍPIO: BRAÚNA

DISTÂNCIAS (km):

UNID. I -	Asfalto:	21.00	Terra.:	5.80
UNID.I I -	Asfalto:	58.00	Terra.:	2.60
UNID. III -	Asfalto:	29.00	Terra.:	5.80

COORDENADAS: E(X): 567292.55 N(Y): 7619849.77
LAT: -21°31'22.1160" LONG: -50°21'0.8412"

CLEALCO - AÇÚCAR E ALCOOL S/A - DEPARTAMENTO DE TOPOGRAFIA

UNIDADE:
I

PARTE:
A/A

FUNDO AGRÍCOLA:
307445

M:\01-Mapa de safra\Mapas Atualizados\Terceiro\307445 - Sítio Santa Clara II (Valter Antonio Bosco)\307445 - Sítio Santa Clara II (Valter Antonio Bosco).dwg

Fernanda Bezerra 18/04/23