ZONA DV	Nº TAL.	DATA PL.	ÁREA (ha)	VARIEDADE
999 4.91%	1	05/2022	24.27	RB 975201
	2		30.64	
	3		25.39	
	4		4.40	
TOTAL PLANTIO			84.70	--------


ÁREAS	(ha)	(%)
PLANTIO	84.70	93.94
CARREADORES	5.41	6.01
OUTROS	0.00	0.00
SUB TOTAL AGRICULTÁVEL	90.11	99.94
AP.P.	0.00	0.00
ÁRVORES	0.01	0.01
OUTROS	0.04	0.04
SUB TOTAL NÃO AGRICULT.	0.05	0.06
ÁREA TOTAL	90.16	100.00

C. NÍVEL: 0.00 m/l 0.00 ha 0.00 %


LEGENDA

- FAZENDA
- TALHÃO
- CURVA DE NÍVEL
- CARREADOR
- CONFRONTANTE
- REDE ELÉTRICA
- TRAJETO VAZIO
- TRAJETO CARREGADO

PLANTIO MANUAL - ESPAÇAMENTO: 1.50 X 1.50
TIRO MÉDIO ESTIMADO: 222.31 m

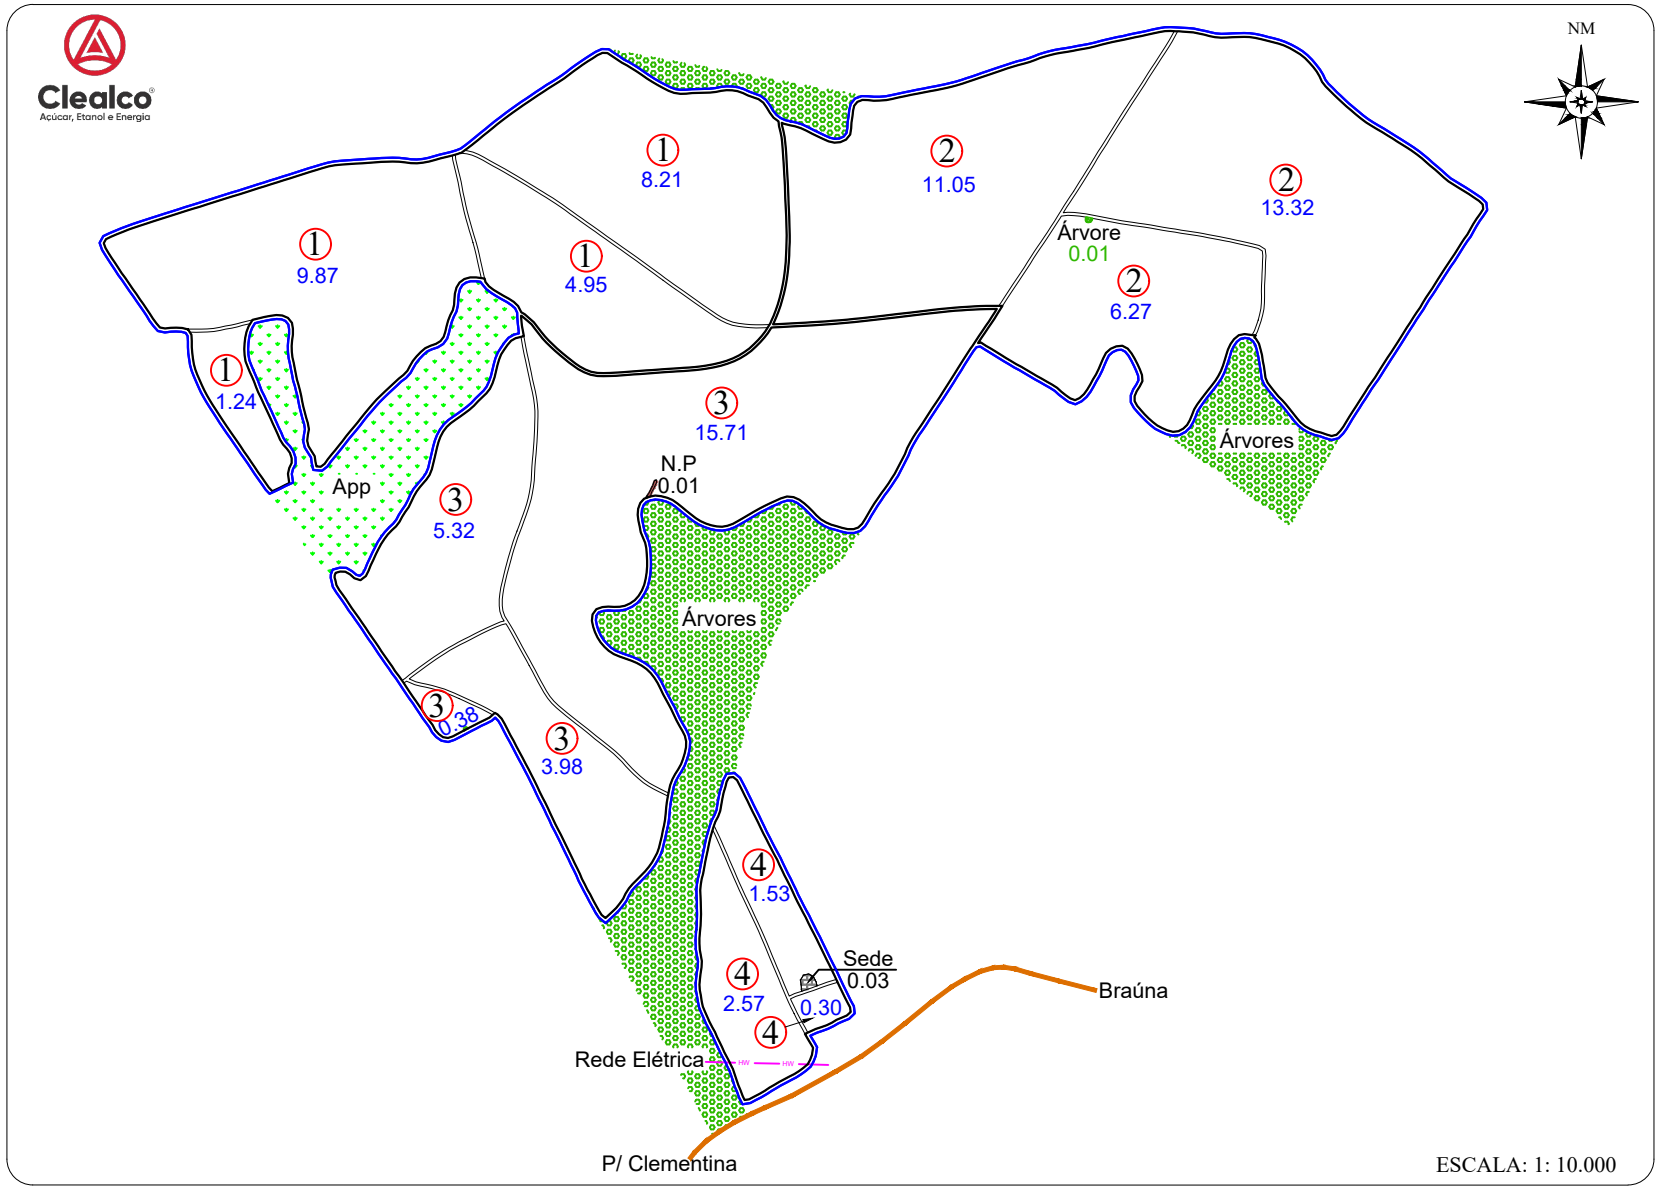

CROQUI DE ACESSO

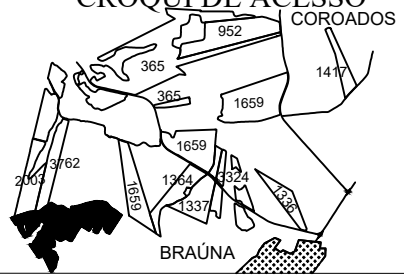

SÍTIO NOSSO RANCHO

PROPRIETÁRIO: FERNANDO BOUGO AVELHAN
COMPRADOR: CLEALCO S/A
MUNICÍPIO: BRAÚNA

DISTÂNCIAS (km):
UNID. I - Asfalto: 20.10 Terra.: 1.00
UNID.I I - Asfalto: 82.00 Terra.: 1.00
UNID. III -Asfalto: 28.00 Terra.: 1.50

COORDENADAS: E(X): 566721.20 N(Y): 7622872.24
LAT: -21°29'43.8893" LONG: -50°21'21.1341"

CLEALCO - AÇÚCAR E ALCOOL S/A - DEPARTAMENTO DE TOPOGRAFIA

UNIDADE: I
PARTE: A/A
FUNDO AGRÍCOLA: 307447

M:\01-Mapa de safra\Mapas Atualizados\Terceiro\307447 - Sítio Nosso Rancho (Fernando Bougo Avelhan)\307447 - Sítio Nosso Rancho (Fernando Bougo Avelhan).dwg

Fernanda Bezerra 20/07/22