ZONA DV	Nº TAL.	DATA PL.	ÁREA (ha)	VARIEDADE
999 5.56 %	1	05/2022	21.15	RB 97 5242
	2		17.38	
	3		17.85	
	4		16.58	
	5		24.35	
TOTAL PLANTIO			97.31	--------

ÁREAS	(ha)	(%)
PLANTIO	97.31	95.86
CARREADORES	2.66	2.62
OUTROS	0.00	0.00
SUB TOTAL AGRICULTÁVEL	99.97	98.48
AP.P.	0.00	0.00
ÁRVORES	1.54	1.52
OUTROS	0.00	0.00
SUB TOTAL NÃO AGRICULT.	1.54	1.52
ÁREA TOTAL	101.51	100.00


C. NÍVEL: 0.00 m/l 0.00 ha 0.00 %

LEGENDA

- FAZENDA
- TALHÃO
- CURVA DE NÍVEL
- CARREADOR
- CONFRONTANTE
- REDE ELÉTRICA
- TRAJETO VAZIO
- TRAJETO CARREGADO


PLANTIO MANUAL - ESPAÇAMENTO: 1.50 X 1.50
TIRO MÉDIO ESTIMADO: 271.30m

Clealco
Açúcar, Etanol e Energia

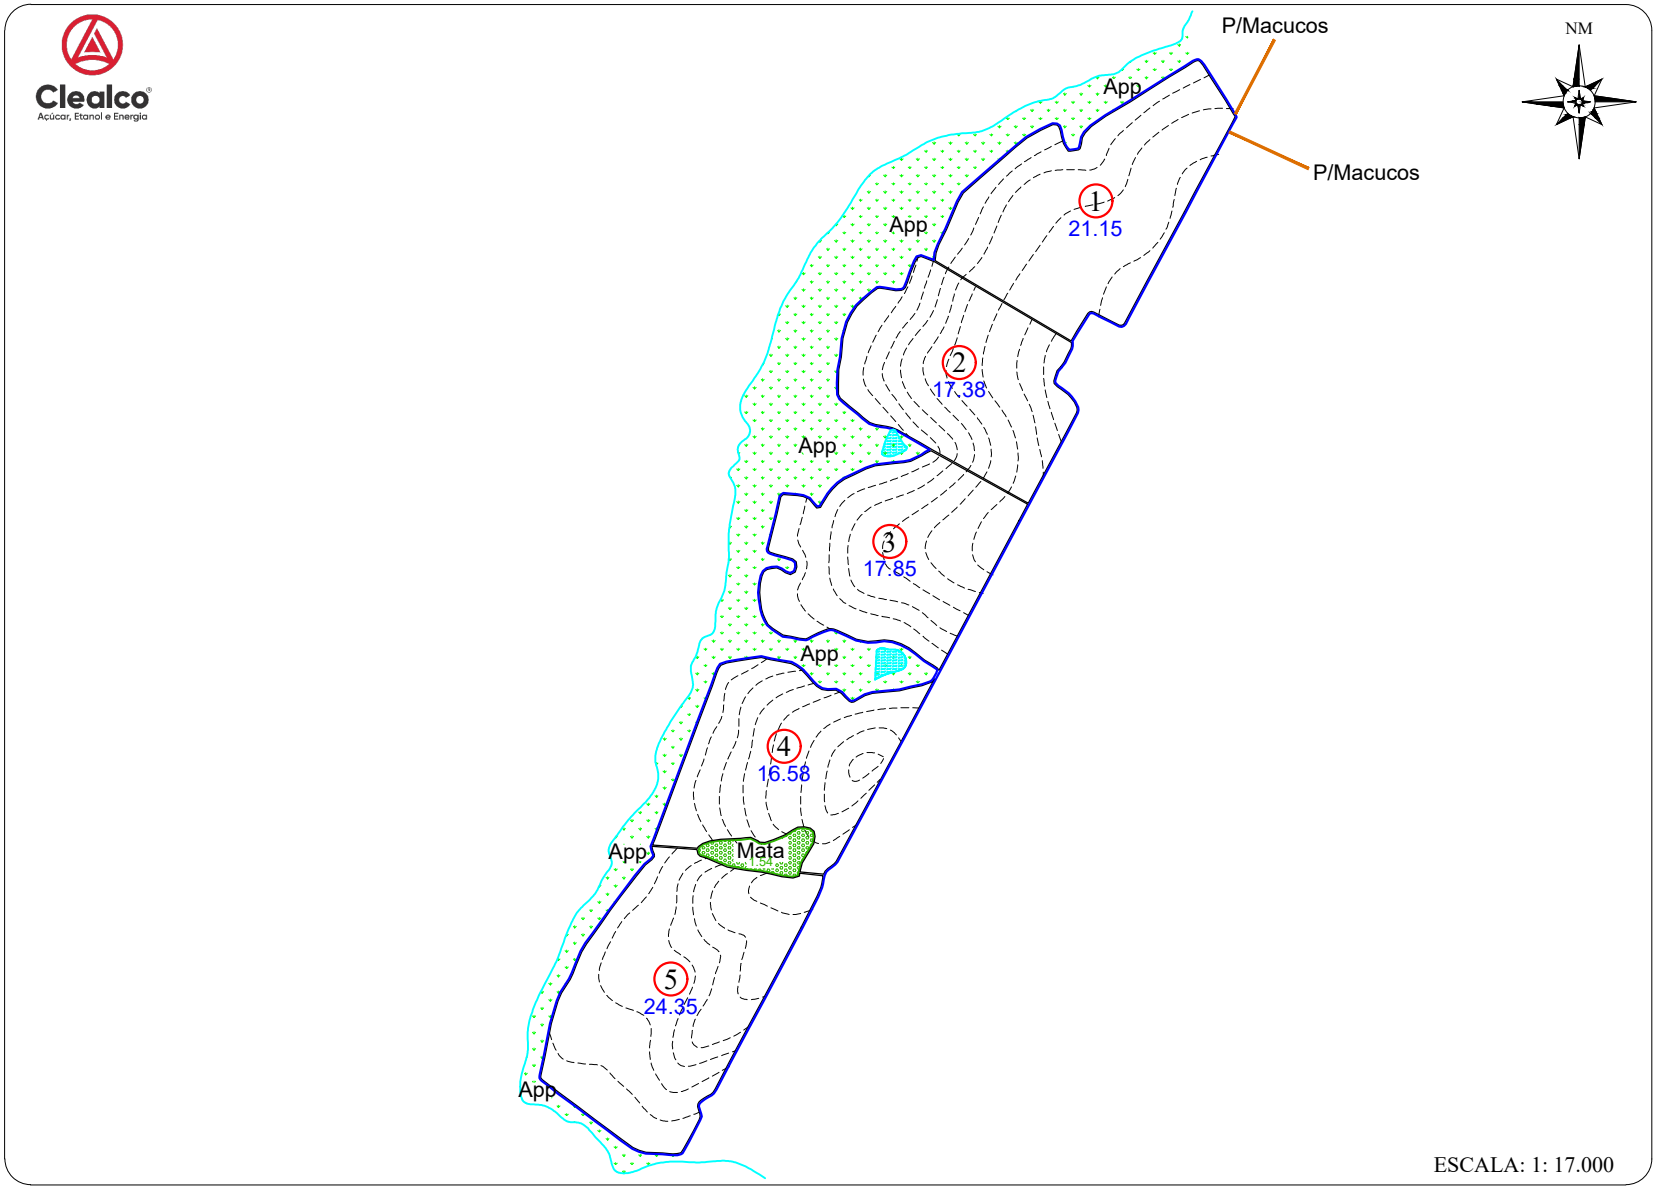

ESCALA: 1: 17.000

CROQUI DE ACESSO

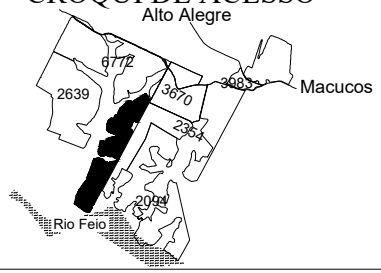

FAZENDA SANTA MARIA

PROPRIETÁRIO: WILLIAN ÁVILA PEREIRA
COMPRADOR: CLEALCO S/A
MUNICÍPIO: GETULINA

DISTÂNCIAS (km):
UNID. I - Asfalto: 68.00 Terra.: 10.60
UNID.I I - Asfalto: 14.60 Terra.: 10.60
UNID. III -Asfalto: 16.60 Terra.: 10.60

COORDENADAS: E(X): 583748.83 N(Y): 7594373.89
LAT: -21°45'8.1590" LONG: -50°11'24.2274"

CLEALCO - AÇÚCAR E ALCOOL S/A - DEPARTAMENTO DE TOPOGRAFIA

UNIDADE: II
PARTE: A/A
FUNDO AGRÍCOLA: 307451

M:\01-Mapa de safra\Mapas Atualizados\Terceiro\307451 - Fazenda Santa Maria (Willian Ávila Pereira)\307451 - Fazenda Santa Maria (Willian Ávila Pereira).dwg

Fabiano Castro 03/06/2023