ZONA DV	Nº TAL.	DATA PL.	ÁREA (ha)	VARIEDADE
999 5.81 %	1	06/2022	23.25	RB 975201
TOTAL PLANTIO			23.25	--------

ÁREAS	(ha)	(%)
PLANTIO	23.25	96.49
CARREADORES	0.85	3.51
OUTROS	0.00	0.00
SUB TOTAL AGRICULTÁVEL	24.10	100.00
AP.P.	0.00	0.00
ÁRVORES	0.00	0.00
OUTROS	0.00	0.00
SUB TOTAL NÃO AGRICULT.	0.00	0.00
ÁREA TOTAL	24.10	100.00

C. NÍVEL:	0.00 m/l	0.00 ha	0.00 %

LEGENDA

▬ FAZENDA	▬ CONFRONTANTE
▬ TALHÃO	— · — REDE ELÉTRICA
▪▪▪ CURVA DE NÍVEL	—▷ TRAJETO VAZIO
— CARREADOR	—► TRAJETO CARREGADO

PLANTIO MANUAL - ESPAÇAMENTO: 1.50 X 1.50
TIRO MÉDIO ESTIMADO: 223.51 m

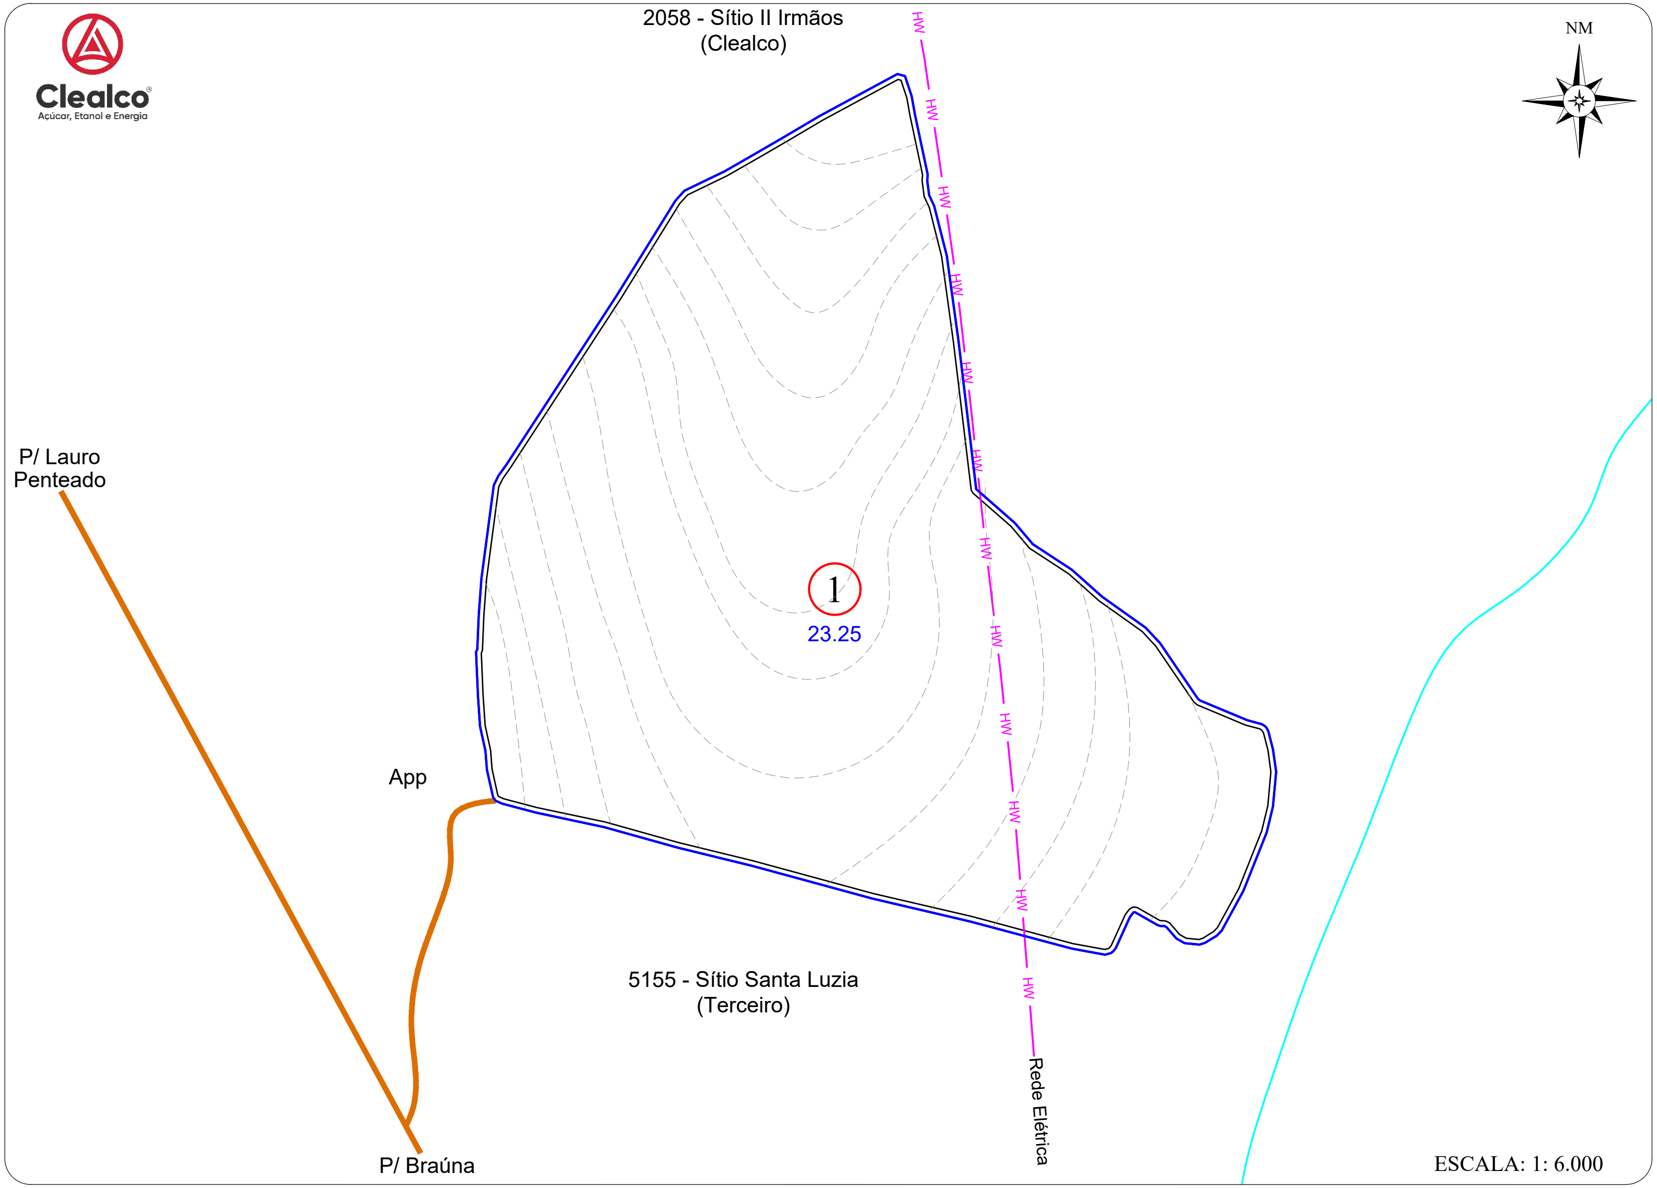

CROQUI DE ACESSO

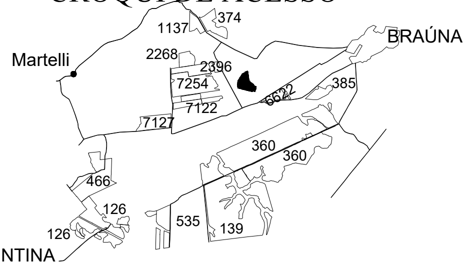

SÍTIO SANTA LUZIA

PROPRIETÁRIO: GILBERTO DANELUCCI
COMPRADOR: CLEALCO S/A
MUNICÍPIO: BRAÚNA

DISTÂNCIAS (km):

UNID. I -	Asfalto:	11.30	Terra.:	9.40
UNID.I I -	Asfalto:	68.00	Terra.:	3.70
UNID. III -	Asfalto:	65.00	Terra.:	3.70

COORDENADAS: E(X):	566114.64	N(Y):	7620923.62
LAT:	-21°30'47.3477"	LONG:	-50°21'41.9372"

CLEALCO - AÇÚCAR E ALCOOL S/A - DEPARTAMENTO DE TOPOGRAFIA

UNIDADE:
I

PARTE:
A/A

FUNDO AGRÍCOLA:
307461

M:\01-Mapa de safra\Mapas Atualizados\Terceiro\307461 - Sítio Santa Luzia (Gilberto Danelucci)\307461 - Sítio Santa Luzia (Gilberto Danelucci).dwg

Fernanda Bezerra 07/02/22