
Clealco
Açúcar, Etanol e Energia

ZONA	Nº TAL.	DATA PL.	ÁREA (ha)	VAR.
999	1	06/2023	7.38	RB975201
	2		1.28	
	3		4.40	
	4		3.19	
	5		4.71	
TOTAL PLANTIO			20.96	--------

ÁREAS	(ha)	(%)
PLANTIO	20.96	92.67
CARREADORES	1.29	5.69
OUTROS	0.00	0.00
SUB TOTAL AGRICULTÁVEL	22.25	98.36
AP.P.	0.00	0.00
ÁRVORES	0.04	0.18
OUTROS	0.33	1.46
SUB TOTAL NÃO AGRICULT.	0.37	1.64
ÁREA TOTAL	22.62	100.00

C. NÍVEL: 3088.96 m/l 0.71 ha 3.14 %

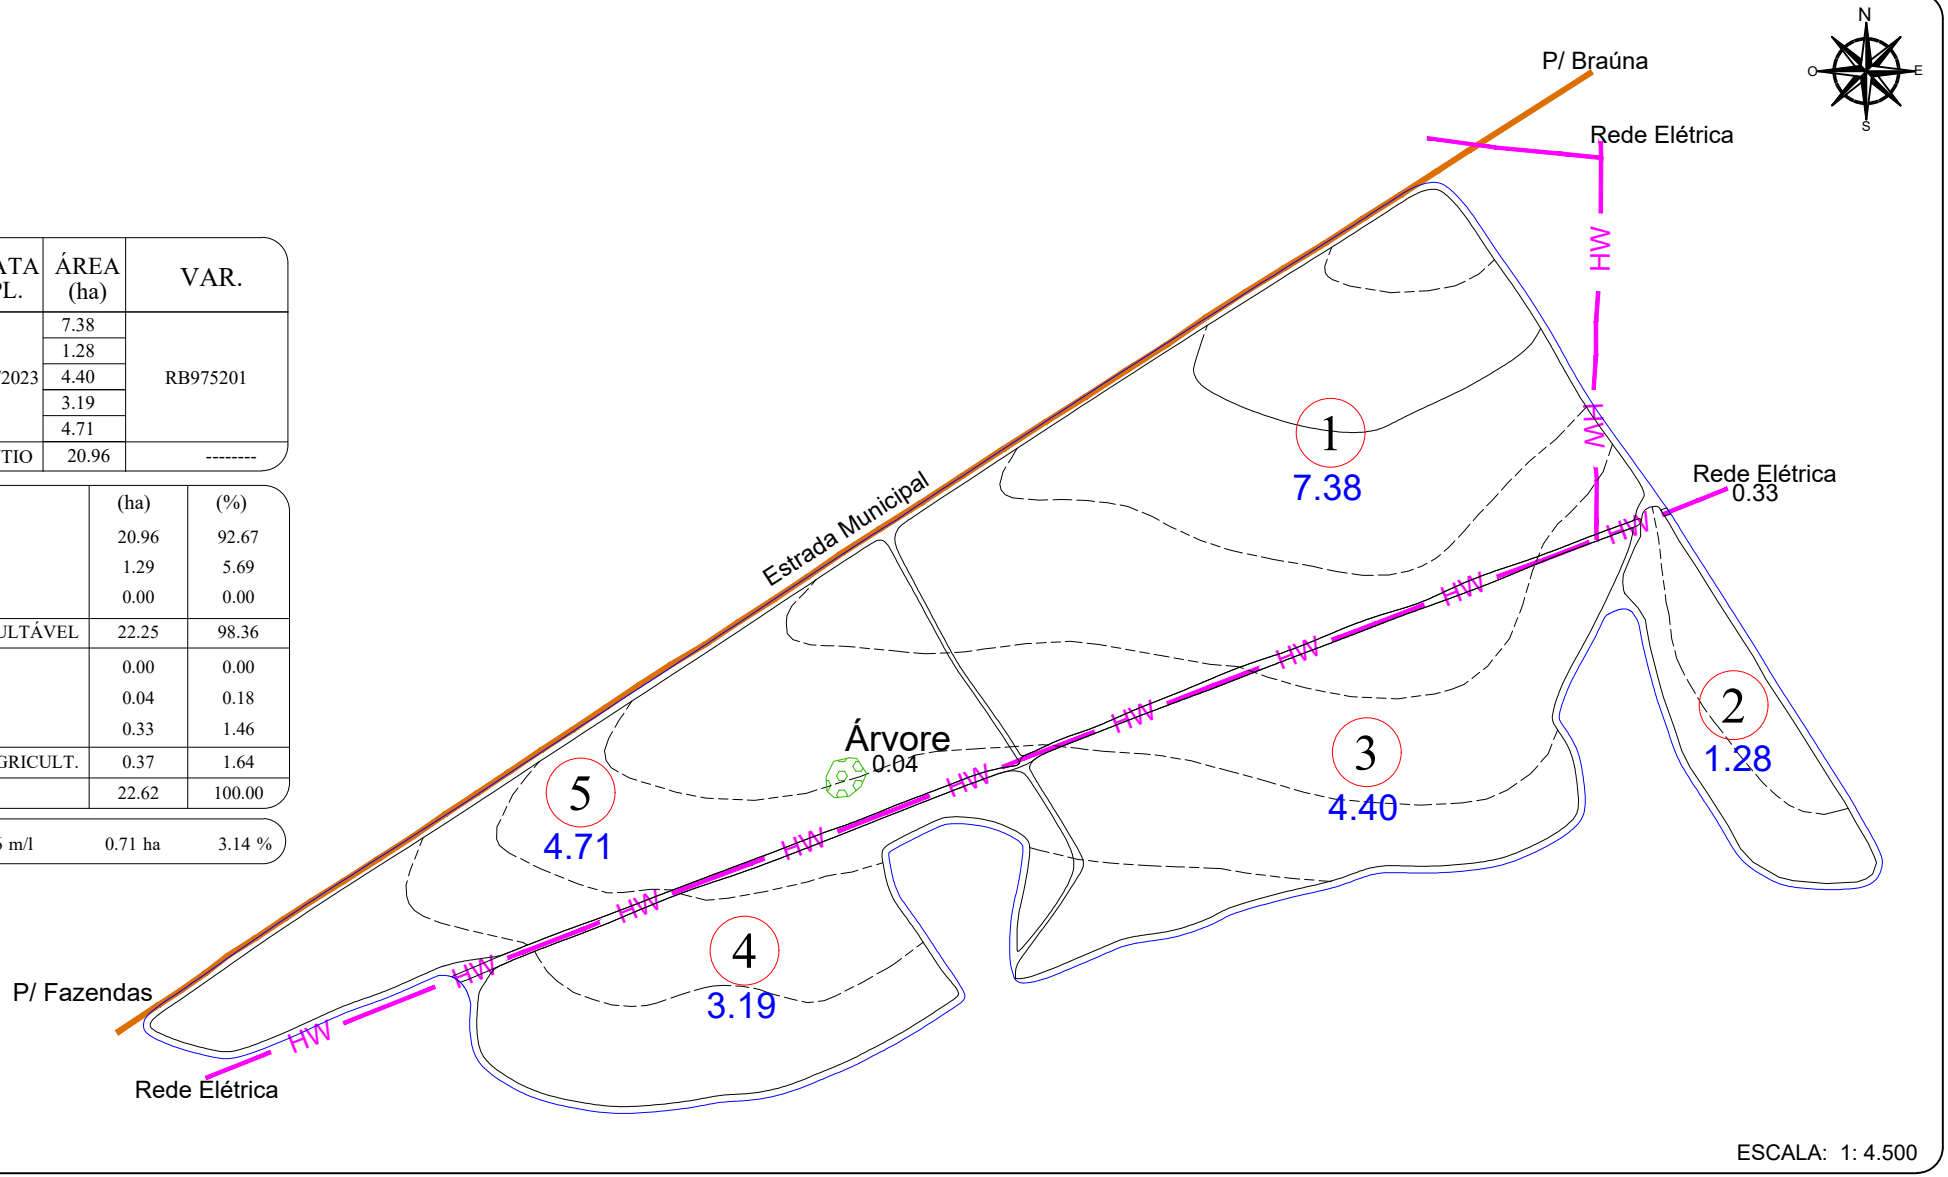


ESCALA: 1: 4.500

LEGENDA
- FAZENDA
- TALHÃO
- REDE ELÉTRICA
- TERRAÇO BASE LARGA
- TERRAÇO EMBUTIDO

ESPAÇAMENTO: 1.50 x 1.50
TIRO MÉDIO ESTIMADO: 129.76m
D.V: 6.06%

CROQUI DE ACESSO

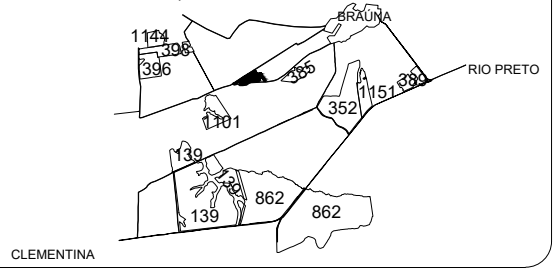

SÍTIO SÃO FRANCISCO

PROPRIETÁRIO: JOSÉ FRANCISCO MARTINS
COMPRADOR: CLEALCO
MUNICÍPIO: BRAÚNA - SP

DISTÂNCIAS (km):
UNID. I - Asfalto: 17.90 Terra.: 7.50
UNID.I I - Asfalto: 68.00 Terra.: 3.70

COORDENADAS: E(X): 567182.20 N(Y): 7620458.68
LAT: -21°31'2.3265" LONG: -50°21'4.7650"
CLEALCO - AÇÚCAR E ALCOOL S/A - DEPARTAMENTO DE GEOTECNOLOGIA

LEVANTAMENTO VIA:
- SATÉLITE
- GPS / VANT
- GOOGLE

UNIDADE: I
PARTE: A/A
FUNDO AGRÍCOLA: 307463

M:\01-Mapa de safra\Mapas Atualizados\Terceiro\307463 - Sítio São Francisco (Jose Francisco Martins)\307463 - Sítio São Francisco (Jose Francisco Martins).dwg

Bruno Gamboa 25/07/25