ZONA DV	Nº TAL.	DATA PL.	ÁREA (ha)	VARIEDADE
999 7.93%	1	07/2023	45.85	RB 867515
TOTAL PLANTIO			45.85	--------

ÁREAS	(ha)	(%)
PLANTIO	45.85	95.62
CARREADORES	1.61	3.36
OUTROS	0.00	0.00
SUB TOTAL AGRICULTÁVEL	47.46	98.98
AP.P.	0.00	0.00
ÁRVORES	0.05	0.10
OUTROS	0.44	0.92
SUB TOTAL NÃO AGRICULT.	0.49	1.02
ÁREA TOTAL	47.95	100.00

C. NÍVEL: 6625.54 m/l 1.52 ha 3.18 %

LEGENDA

FAZENDA	CONFRONTANTE
TALHÃO	REDE ELÉTRICA
CURVA DE NÍVEL	TRAJETO VAZIO
CARREADOR	TRAJETO CARREGADO

PLANTIO MANUAL - ESPAÇAMENTO: 1.50 X 1.50
TIRO MÉDIO ESTIMADO: 341.11 m

Clealco
Açúcar, Etanol e Energia

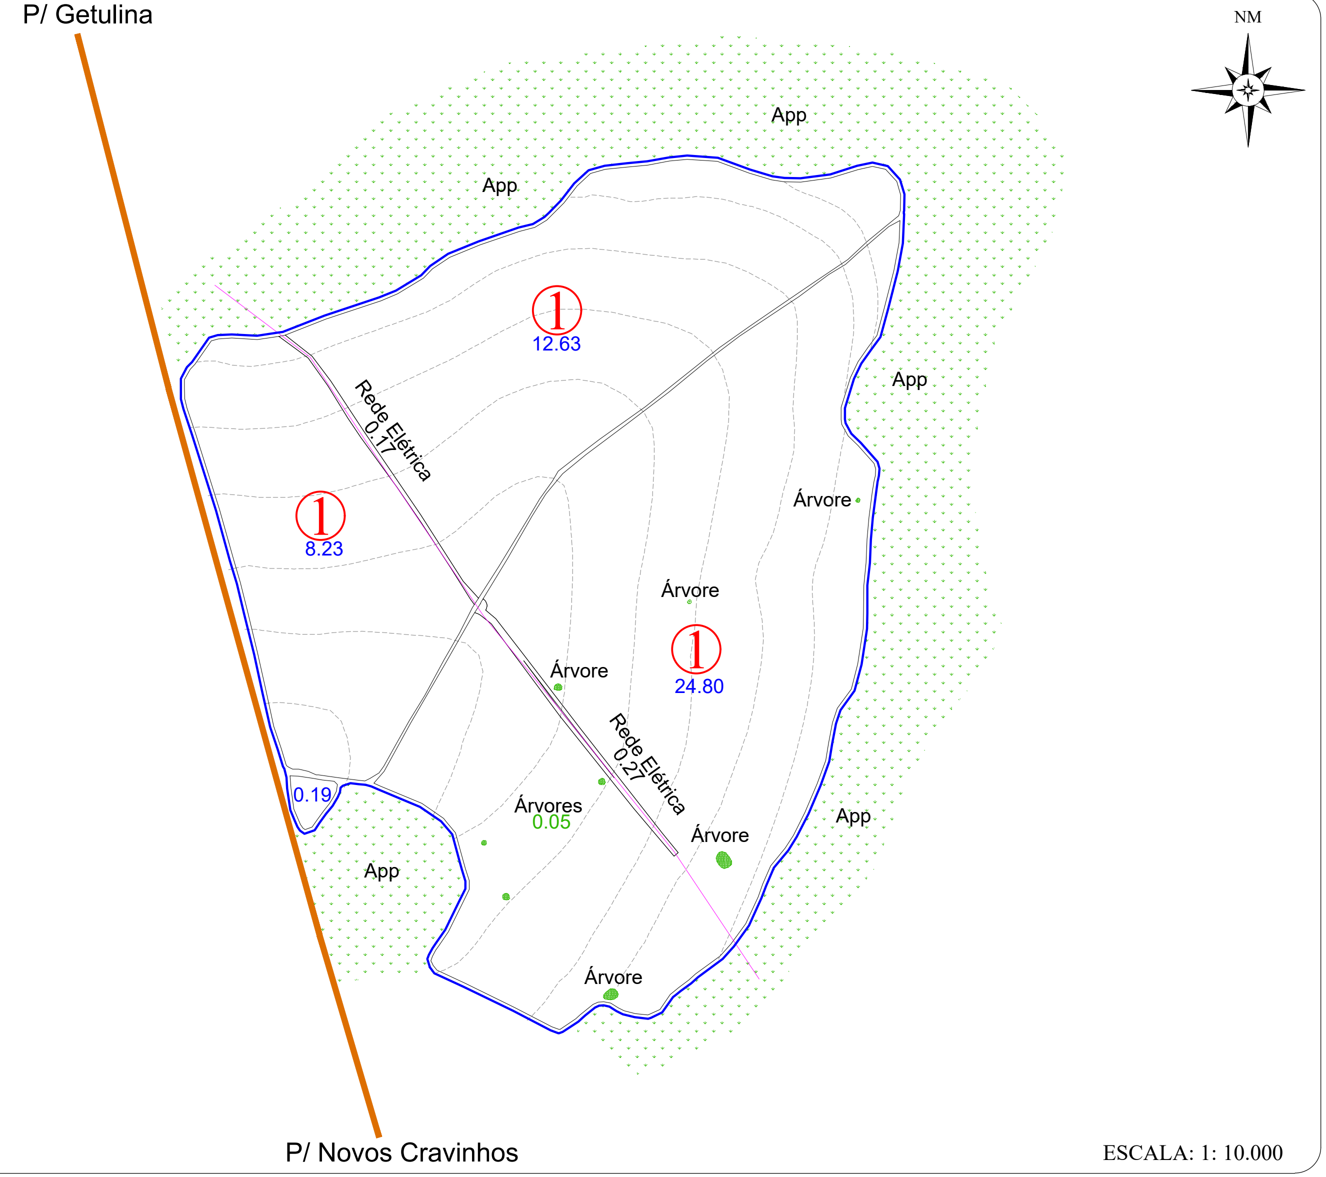
P/ Getulina
NM
App
App
App
App
App
①
12.63
①
8.23
①
24.80
Rede Elétrica
0.17
Rede Elétrica
0.27
Árvore
Árvore
Árvore
Árvore
Árvore
Árvores
0.05
0.19
P/ Novos Cravinhos

ESCALA: 1: 10.000

CROQUI DE ACESSO

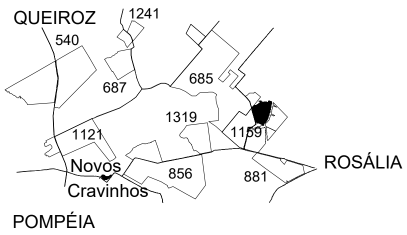
QUEIROZ
1241
540
687
685
1319
1121
1159
Novos
Cravinhos
856
881
ROSÁLIA
POMPÉIA

SÍTIO OKI

PROPRIETÁRIO:	FLAVIO HENRIQUE S. DE JESUS
ARRENDATÁRIO:	CLEALCO S/A
MUNICÍPIO:	MARÍLIA

DISTÂNCIAS (km):

UNID. I -	Asfalto:	71.50	Terra.:	13.80
UNID.I I -	Asfalto:	20.50	Terra.:	13.80
UNID. III -	Asfalto:	78.00	Terra.:	13.80

COORDENADAS: E(X): 598593.7413 N(Y): 7571070.3699
LAT: 21º57'42,98644" LONG: 50º02'42,44821"

CLEALCO - AÇÚCAR E ALCOOL S/A - DEPARTAMENTO DE TOPOGRAFIA

UNIDADE:
II

PARTE:
A/A

FUNDO AGRÍCOLA:
307473

M:\03-Projetos (Sistematização, Pré, Pós e outros)\Terceiro\2023\Joao\Pós Plantio\307473 - Sítio Oki (Flavio Henrique Silva de Jesus) - Pós Plantio 2023.dwg

Benati 07/12/2023