D.V.	Nº TAL.	DATA PL.	ÁREA (ha)	VARIEDADE
6.14 %	1	07/2023	18.90	CTC 9001
	2		14.31	
	3		7.28	
	4		17.64	
	5		4.82	
	6		10.74	
	7	04/2024	52.32	CV7870
TOTAL PLANTIO			126.01	

ÁREAS	(ha)	(%)
PLANTIO	126.01	95.99
CARREADORES	4.24	3.23
OUTROS	0.90	0.69
SUB TOTAL AGRICULTÁVEL	131.15	99.90
AP.P.	0.00	0.00
ÁRVORES	0.04	0.03
OUTROS	0.09	0.07
SUB TOTAL NÃO AGRICULT.	0.13	0.10
ÁREA TOTAL	131.28	100.00


C. NÍVEL: 23547.59 m/l 5.42 ha 4.13 %

LEGENDA


- FAZENDA
- TALHÃO
- REDE ELÉTRICA
- TERRAÇO BASE LARGA
- TERRAÇO EMBUTIDO

ESPAÇAMENTO: 1.50 x 1.50

TIRO MÉDIO ESTIMADO: 000.00 m

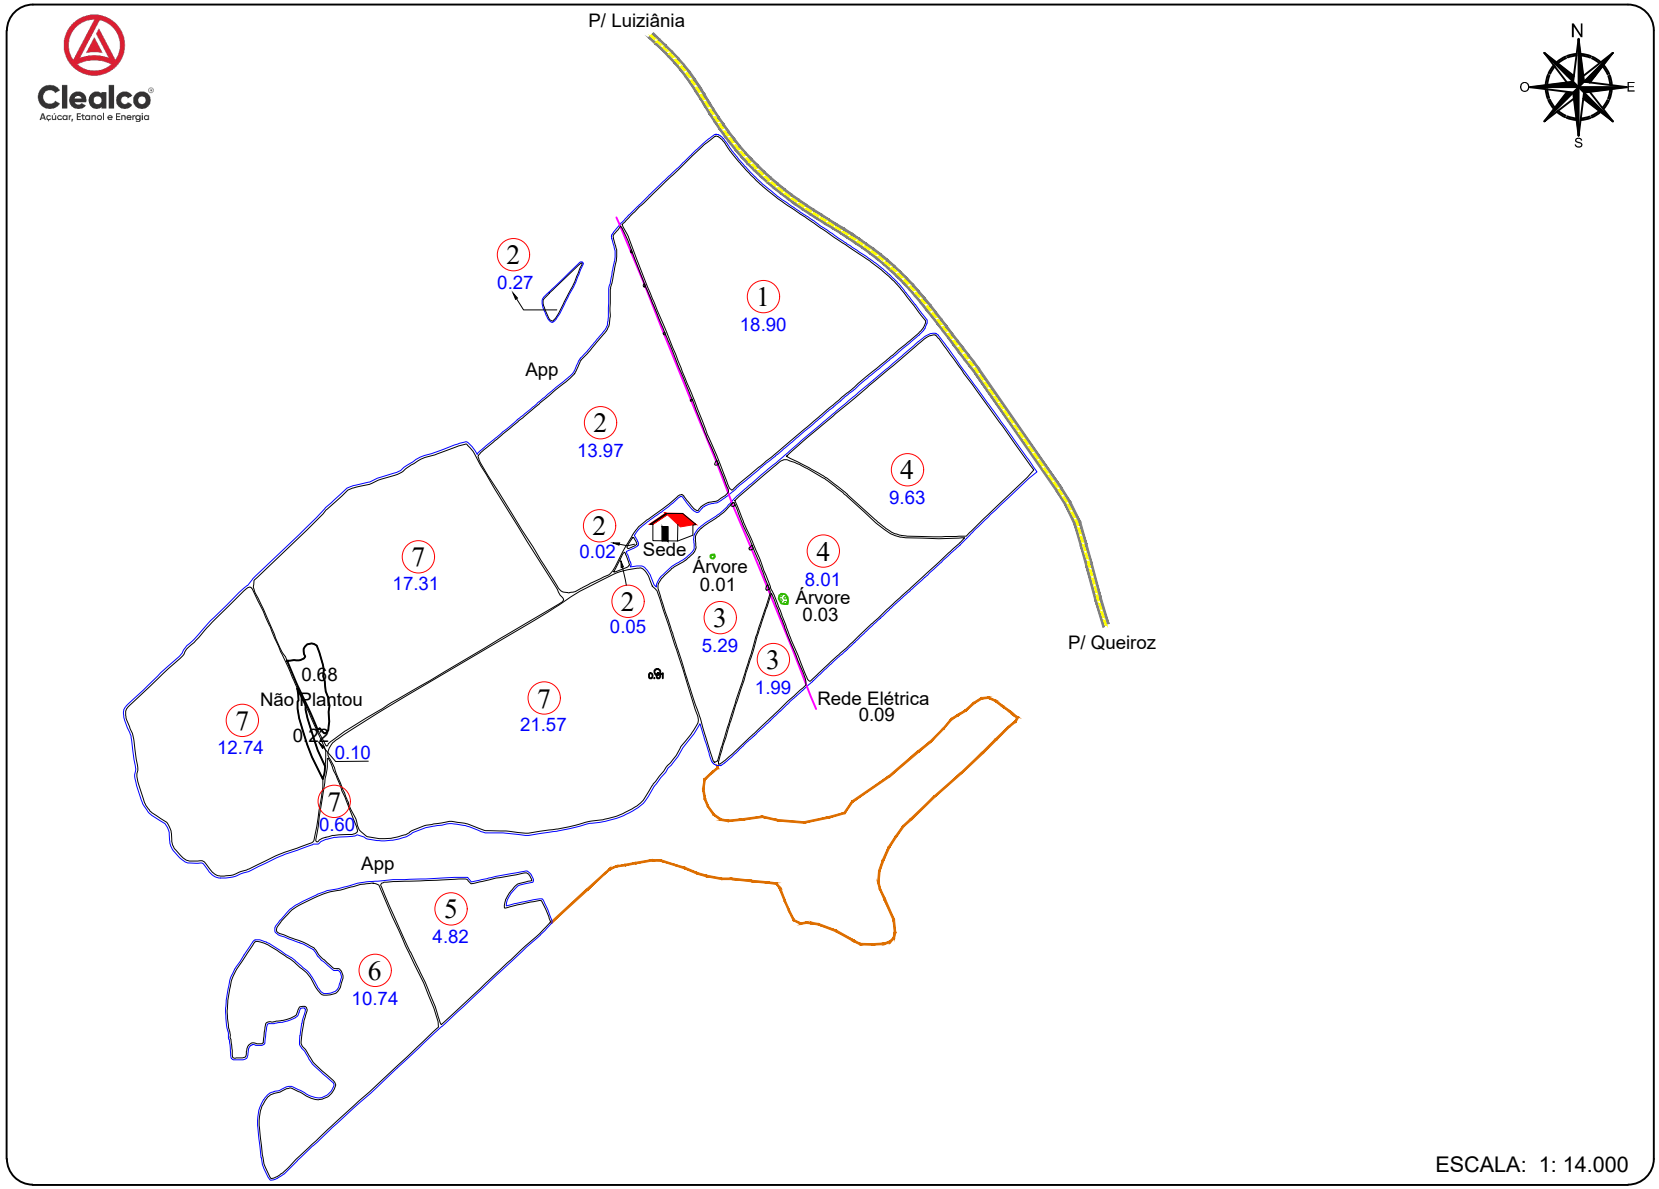

CROQUI DE ACESSO

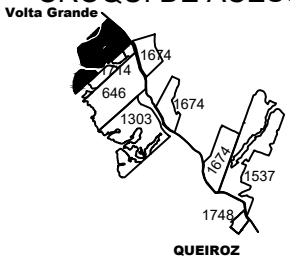

FAZENDA SOLER

PROPRIETÁRIO: SILVANA SOLER T. LONG DE SOUZA
COMPRADOR: CLEALCO S/A
MUNICÍPIO: QUEIROZ - SP

DISTÂNCIAS (km):
UNIDADE I - 47.50
UNIDADE I I - 15.31

COORDENADAS: E(X): 573592.57 N(Y): 7594897.73
LAT: -21°44'52.7479" LONG: -50°17'17.8863"

CLEALCO - AÇÚCAR E ALCOOL S/A - DEPARTAMENTO DE GEOTECNOLOGIA

UNIDADE: II

PARTE: A/A

FUNDO AGRÍCOLA: 307476