ZONA D.V.	Nº TAL.	DATA PL.	ÁREA (ha)	VARIEDADE
999 5.82 %	1	07/2023	17.24	RB975242
	2		19.10	
	3		19.31	
	4		18.58	
	5		17.21	
	6		7.68	
	7		23.50	
	8		4.10	
	9		12.32	
	10		9.67	
	11		12.29	
TOTAL PLANTIO			161.00	--------


ÁREAS	(ha)	(%)
PLANTIO	161.00	94.27
CARREADORES	8.29	4.85
OUTROS	0.05	0.03
SUB TOTAL AGRICULTÁVEL	169.34	99.16
AP.P.	0.00	0.00
ÁRVORES	0.31	0.18
OUTROS	1.13	0.66
SUB TOTAL NÃO AGRICULT.	1.44	0.84
ÁREA TOTAL	170.78	100.00

C. NÍVEL: 25586.73 m/l 5.88 ha 3.45 %


LEGENDA

- FAZENDA
- TALHÃO
- CURVA DE NÍVEL
- CARREADOR
- CONFRONTANTE
- REDE ELÉTRICA
- TRAJETO VAZIO
- TRAJETO CARREGADO

PLANTIO MANUAL - ESPAÇAMENTO: 1.50 X 1.50
TIRO MÉDIO ESTIMADO: 362.04m

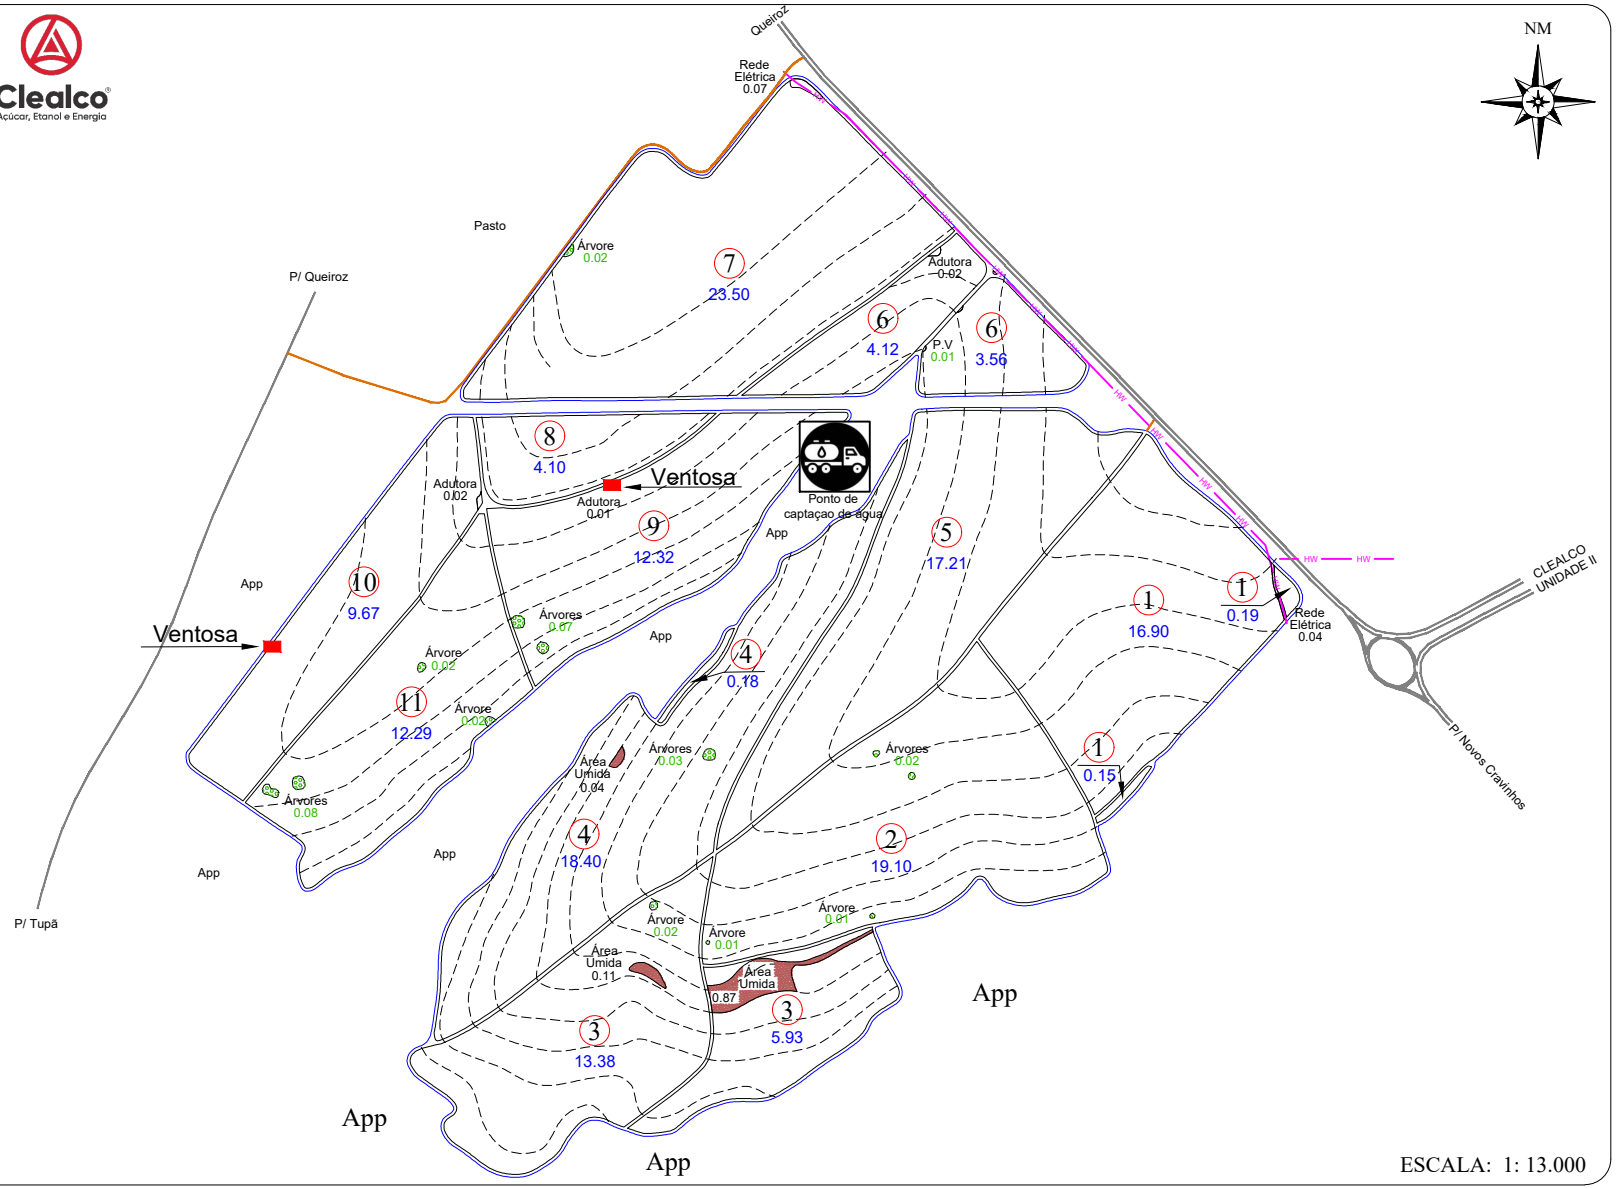

CROQUI DE ACESSO

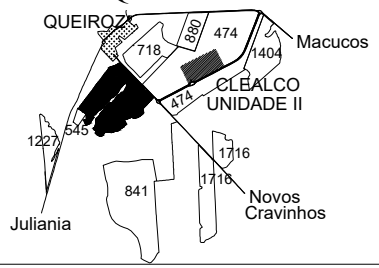

FAZENDA MARIANA

PROPRIETÁRIO: HELIO CESAR F. BARROS
COMPRADOR: CLEALCO S/A
MUNICÍPIO: QUEIROZ - SP

DISTÂNCIAS (km):
UNID. I - Asfalto: 56.00 Terra.: 0.00
UNID.I I - Asfalto: 2.40 Terra.: 0.00
UNID. III -Asfalto: 56.00 Terra.: 0.00

COORDENADAS: E(X): 579059.13 N(Y): 7587636.77
LAT: -21°48'48.0429" LONG: -50°14'6.3290"

CLEALCO - AÇÚCAR E ALCOOL S/A - DEPARTAMENTO DE TOPOGRAFIA

UNIDADE: II
PARTE: A/A
FUNDO AGRÍCOLA: 307479