ZONA D.V.	Nº TAL.	DATA PL.	ÁREA (ha)	VAR.
999 5.98 %	1	05/2022	17.34	CTC 04
	2		9.57	
	3		20.73	
	4		15.78	
TOTAL PLANTIO			63.42	--------


ÁREAS	(ha)	(%)
PLANTIO	63.42	97.12
CARREADORES	1.68	2.57
OUTROS	0.00	0.00
SUB TOTAL AGRICULTÁVEL	65.10	99.69
AP.P.	0.00	0.00
ÁRVORES	0.20	0.31
OUTROS	0.00	0.00
SUB TOTAL NÃO AGRICULT.	0.20	0.31
ÁREA TOTAL	65.30	100.00

C. NÍVEL: 9367.57 m/l 2.15 ha 3.30 %


LEGENDA

- FAZENDA
- TALHÃO
- CURVA DE NÍVEL
- CARREADOR
- CONFRONTANTE
- REDE ELÉTRICA
- TRAJETO VAZIO
- TRAJETO CARREGADO

PLANTIO MANUAL - ESPAÇAMENTO: 1.50 X 1.50
TIRO MÉDIO ESTIMADO: 293.45 m

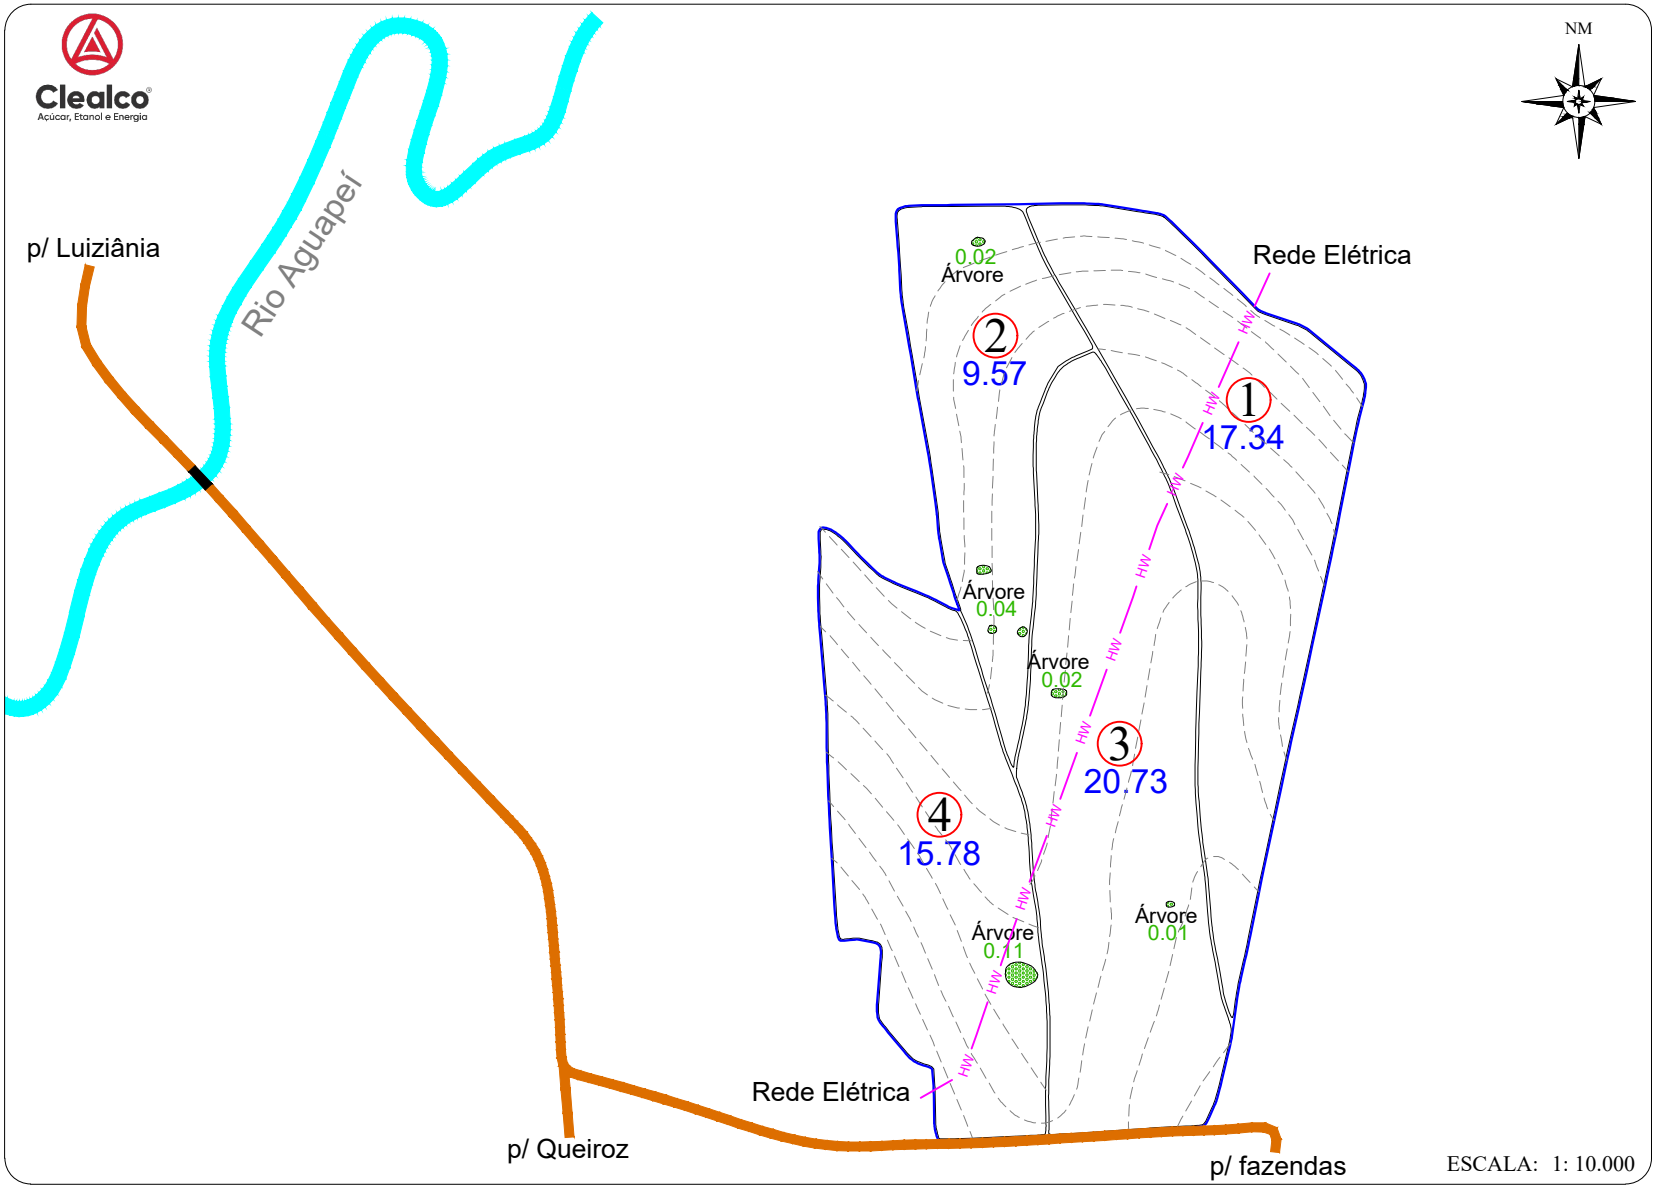

CROQUI DE ACESSO

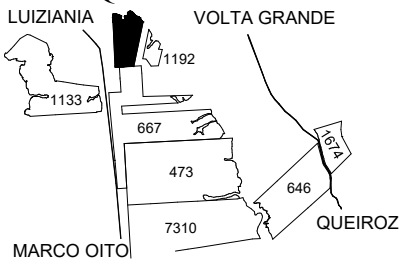

SÍTIO BEIRA RIO

PROPRIETÁRIO: CLÉZIO HUNGARO E OUTROS
COMPRADOR: CLEALCO S/A
MUNICÍPIO: LUIZIÂNIA - SP

DISTÂNCIAS (km):
UNID. I - Asfalto: 32.50 Terra.: 7.00
UNID.I I - Asfalto: 16.50 Terra.: 17.00
UNID. III -Asfalto: 36.50 Terra.: 7.70

COORDENADAS: E(X): 570160.29 N(Y): 7598379.03
LAT: -21°43'0.0265" LONG: -50°19'17.9052"

CLEALCO - AÇÚCAR E ALCOOL S/A - DEPARTAMENTO DE TOPOGRAFIA

UNIDADE: II
PARTE: A/A
FUNDO AGRÍCOLA: 307480