ZONA D.V.	Nº TAL.	DATA PL.	ÁREA (ha)	VARIEDADE
999 5.95 %	1	05/2023	4.30	RB 975201
	2		0.60	
	3		24.79	
TOTAL PLANTIO			29.69	--------

ÁREAS	(ha)	(%)
PLANTIO	29.69	94.93
CARREADORES	1.45	4.62
OUTROS	0.00	0.00
SUB TOTAL AGRICULTÁVEL	31.14	99.55
AP.P.	0.00	0.00
ÁRVORES	0.14	0.45
OUTROS	0.00	0.00
SUB TOTAL NÃO AGRICULT.	0.14	0.45
ÁREA TOTAL	31.28	100.00


C. NÍVEL: 6461.19 m/l 1.49 ha 4.75 %

LEGENDA

- FAZENDA
- TALHÃO
- CURVA DE NÍVEL
- CARREADOR
- CONFRONTANTE
- REDE ELÉTRICA
- TRAJETO VAZIO
- TRAJETO CARREGADO


PLANTIO MANUAL - ESPAÇAMENTO: 1.50 X 1.50
TIRO MÉDIO ESTIMADO: 184.81 m

Clealco
Açúcar, Etanol e Energia

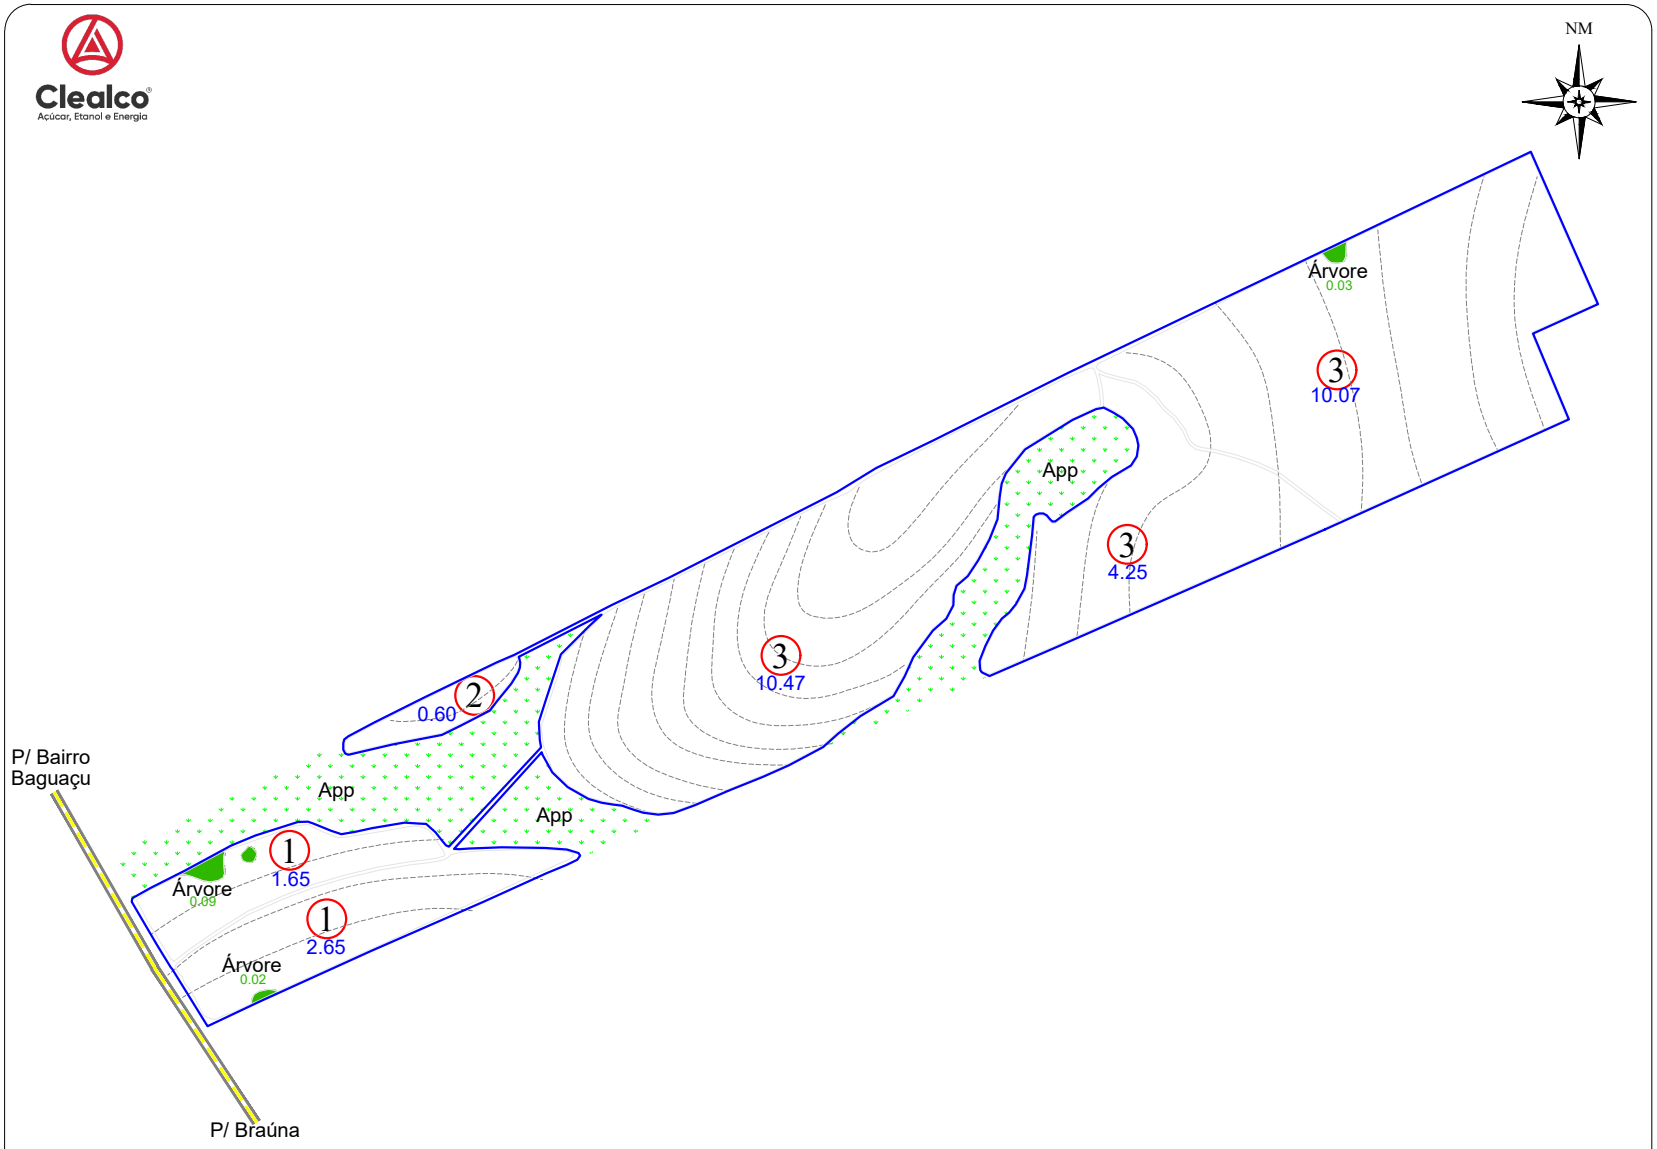

ESCALA: 1: 8.000

CROQUI DE ACESSO

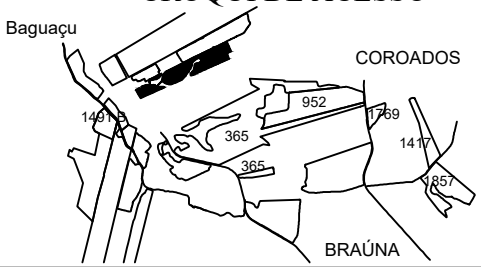

SÍTIO XANDU

PROPRIETÁRIO: THIAGO TUNES DOS SANTOS
COMPRADOR: CLEALCO S/A
MUNICÍPIO: COROADOS

DISTÂNCIAS (km):
UNID. I - Asfalto: 27.00 Terra.: 0.50
UNID.I I - Asfalto: 75.00 Terra.: 0.50
UNID. III -Asfalto: 69.00 Terra.: 0.50

COORDENADAS: E(X): 567338.74 N(Y): 7626711.98
LAT: -21°27'38.9210" LONG: -50°21'0.2270"

CLEALCO - AÇÚCAR E ALCOOL S/A - DEPARTAMENTO DE TOPOGRAFIA

UNIDADE: I
PARTE: A/A
FUNDO AGRÍCOLA: 307481

M:\03-Projetos (Sistematização, Pré, Pós e outros)\Terceiro\2023\Edvaldo\Pós Plantio\307481 - Sítio Xandu (Thiago Tunes dos Santos) - Pós Plantio 2023.dwg

Benati 12/12/2023