ZONA D.V.	Nº TAL.	DATA PL.	ÁREA (ha)	VARIEDADE
999 5.40%	1	05/2023	8.08	RB 975242
	2		20.01	
	3		21.08	
	4		12.67	
TOTAL PLANTIO			61.84	--------


ÁREAS	(ha)	(%)
PLANTIO	61.84	95.84
CARREADORES	2.49	3.87
OUTROS	0.00	0.00
SUB TOTAL AGRICULTÁVEL	64.33	99.71
AP.P.	0.00	0.00
ÁRVORES	0.19	0.29
OUTROS	0.00	0.00
SUB TOTAL NÃO AGRICULT.	0.19	0.29
ÁREA TOTAL	64.52	100.00

C. NÍVEL: 8726.26 m/l 2.01 ha 3.11 %


LEGENDA

- FAZENDA
- TALHÃO
- CURVA DE NÍVEL
- CARREADOR
- CONFRONTANTE
- REDE ELÉTRICA
- TRAJETO VAZIO
- TRAJETO CARREGADO

PLANTIO MANUAL - ESPAÇAMENTO: 1.50 X 1.50

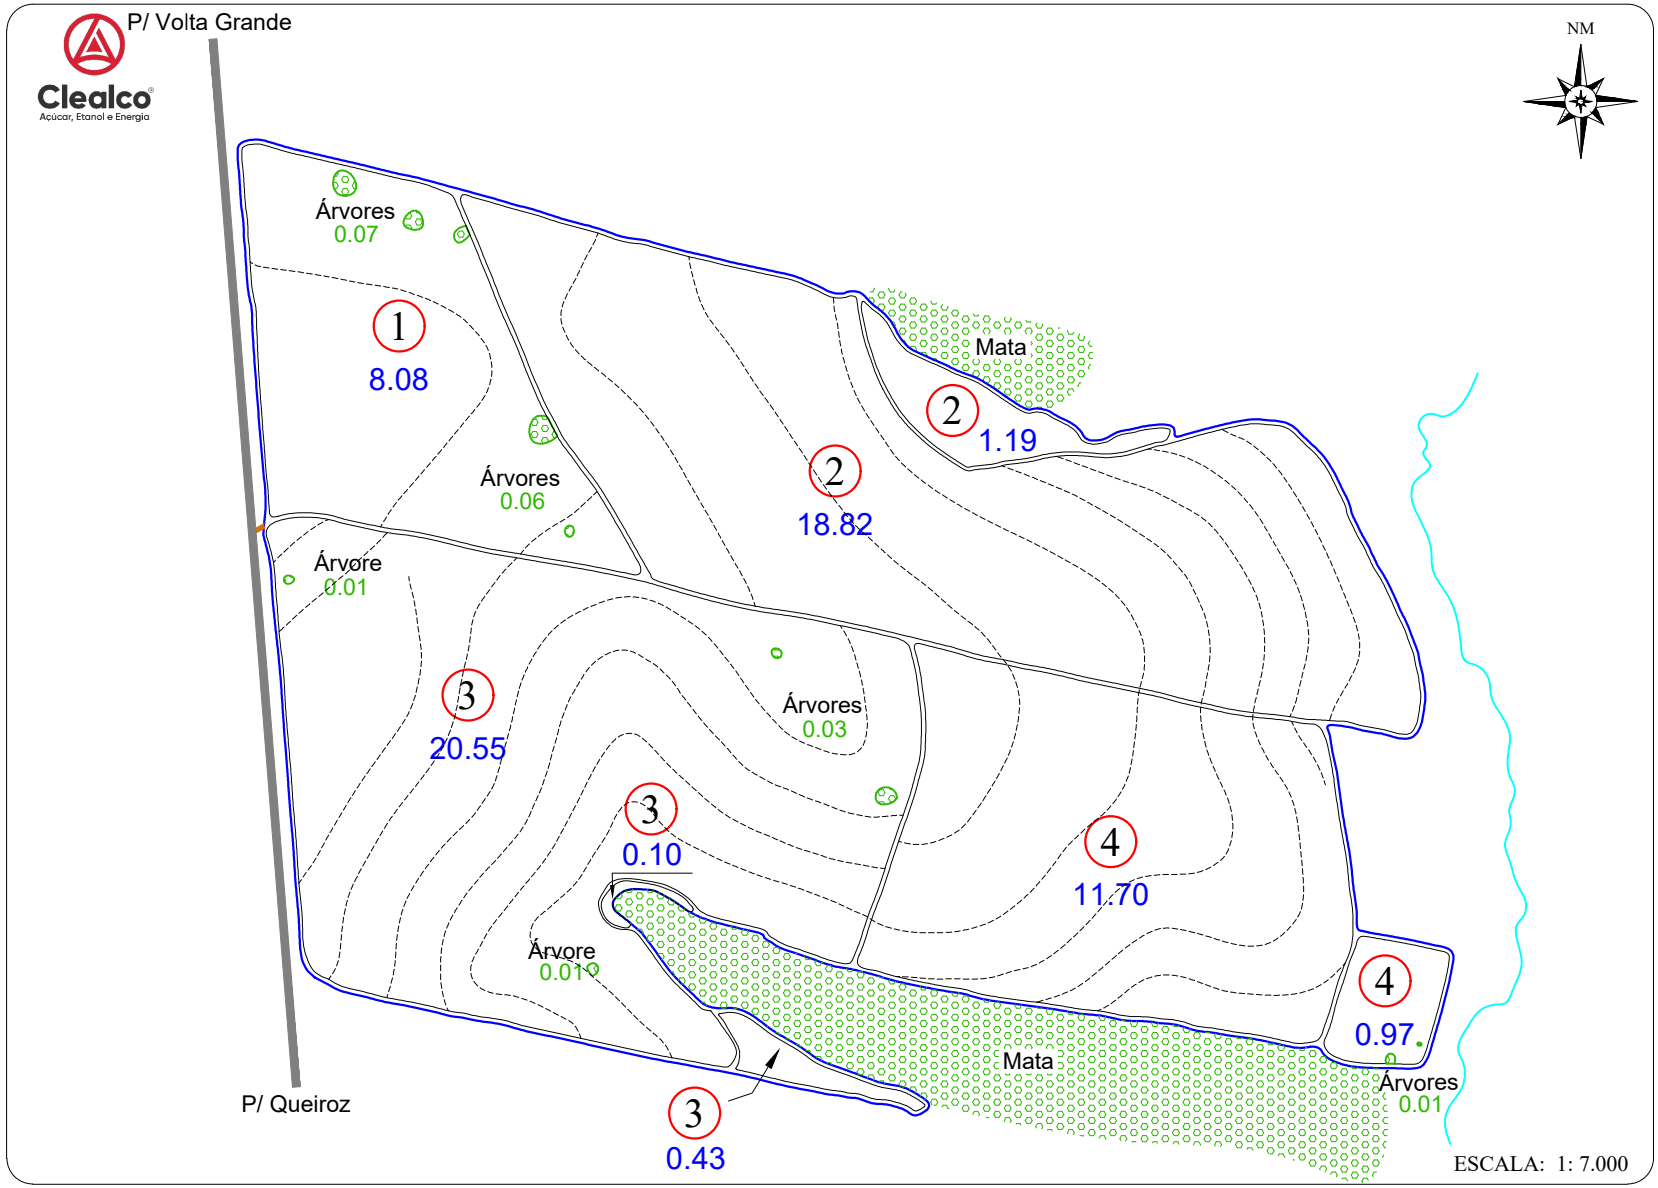

CROQUI DE ACESSO

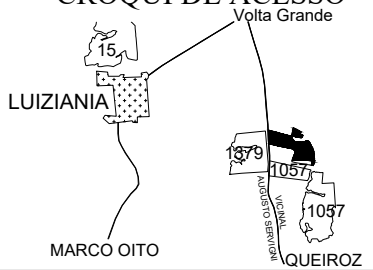

FAZENDA SANTA MARIA

PROPRIETÁRIO: CLEZIO HUNGARO
COMPRADOR: CLEALCO S/A
MUNICÍPIO: LUIZIANIA

DISTÂNCIAS (km):
UNID. I - Asfalto: 35.00 Terra.: 1.00
UNID.I I - Asfalto: 17.00 Terra.: 1.00
UNID. III -Asfalto: 34.50 Terra.: 1.00

COORDENADAS: E(X): 573427.99 N(Y): 7601550.34
LAT: -21°41'16.4092" LONG: -50°17'24.6775"

CLEALCO - AÇÚCAR E ALCOOL S/A - DEPARTAMENTO DE TOPOGRAFIA

UNIDADE: II
PARTE: A/A
FUNDO AGRÍCOLA: 307488