
Clealco
Açúcar, Etanol e Energia

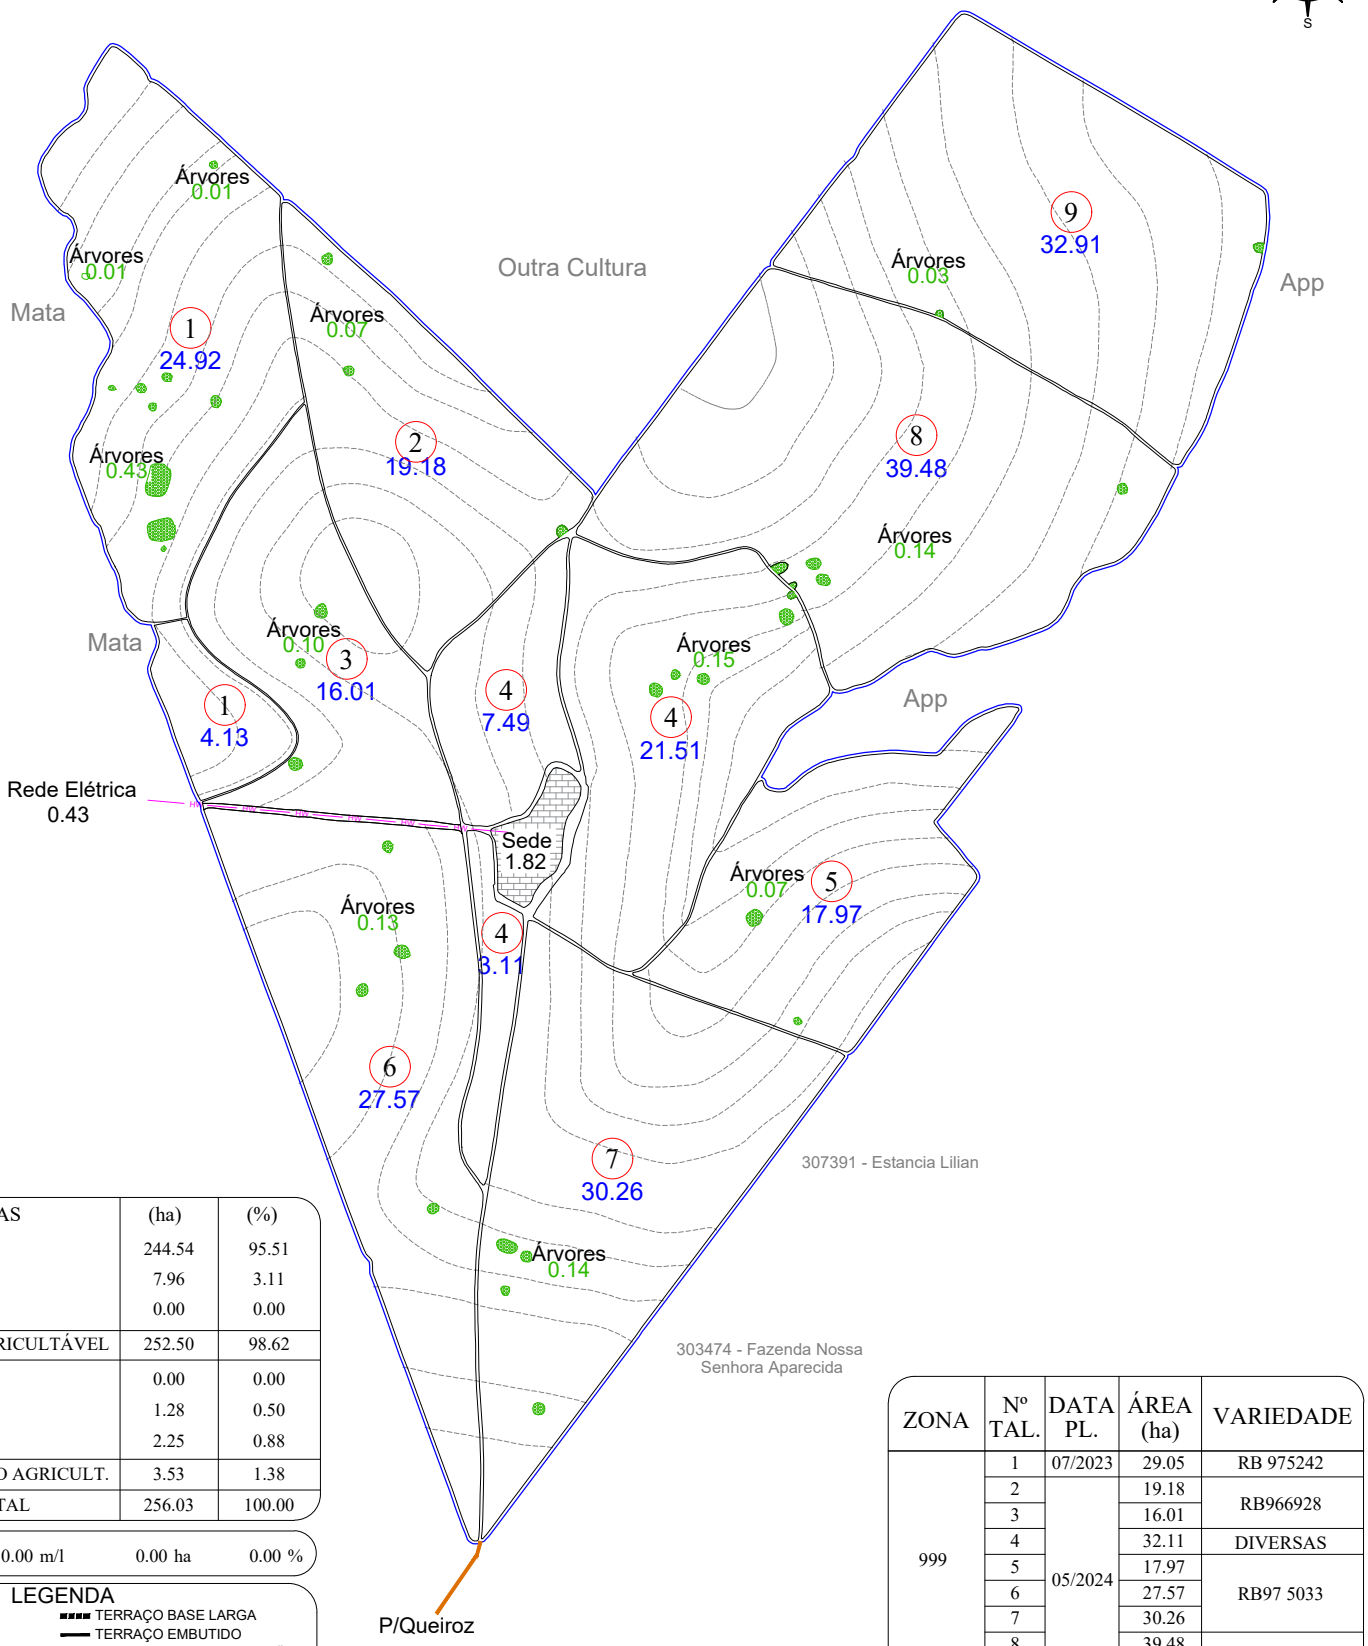

ÁREAS	(ha)	(%)
PLANTIO	244.54	95.51
CARREADORES	7.96	3.11
OUTROS	0.00	0.00
SUB TOTAL AGRICULTÁVEL	252.50	98.62
AP.P.	0.00	0.00
ÁRVORES	1.28	0.50
OUTROS	2.25	0.88
SUB TOTAL NÃO AGRICULT.	3.53	1.38
ÁREA TOTAL	256.03	100.00

C. NÍVEL: 0.00 m/l 0.00 ha 0.00 %

LEGENDA


- FAZENDA
- TALHÃO
- REDE ELÉTRICA
- VAZIO
- TERRAÇO BASE LARGA
- TERRAÇO EMBUTIDO
- (P.O.A) PATIO DE OPERAÇÃO
- CARREGADO

ESPAÇAMENTO: 1.50 x 1.50
TIRO MÉDIO ESTIMADO: 397.08 m
D.V: 4.62 %

ZONA	Nº TAL.	DATA PL.	ÁREA (ha)	VARIEDADE
999	1	07/2023	29.05	RB 975242
	2	05/2024	19.18	RB966928
	3		16.01	
	4		32.11	DIVERSAS
	5		17.97	RB97 5033
	6		27.57	
	7		30.26	
	8		39.48	RB966928
	9		32.91	
TOTAL PLANTIO			244.54	

ESCALA: 1: 13.000

CROQUI DE ACESSO

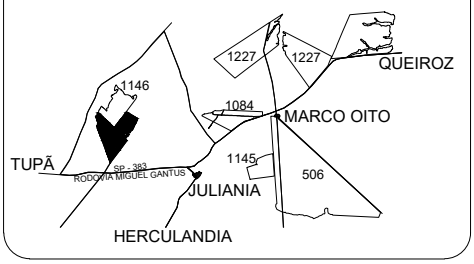

FAZENDA VISTA ALEGRE

PROPRIETÁRIO: CLEZIO HUNGARO E OUTROS
COMPRADOR: CLEALCO
MUNICÍPIO: TUPÃ - SP

DISTÂNCIAS (km):
UNID. I - Asfalto: 83.80 Terra.: 0.40
UNID.I I - Asfalto: 24.00 Terra.: 0.40

COORDENADAS: E(X): 561122.44 N(Y): 7579883.49
LAT: -21°53'2.7710" LONG: -50°24'30.0062"

CLEALCO - AÇÚCAR E ALCOOL S/A - DEPARTAMENTO DE GEOTECNOLOGIA

LEVANTAMENTO VIA:
- SATÉLITE
- GPS / VANT
- GOOGLE

UNIDADE: II
PARTE: A/A
FUNDO AGRÍCOLA: 307501

M:\01-Mapa de safra\Mapas Atualizados\Terceiro\307501 - Fazenda Vista Alegre (Clezio Hungaro)\307501 - Fazenda Vista Alegre (Clezio Hungaro).dwg

Bruno Gamboa 26/05/26