ZONA DV	Nº TAL.	DATA PL.	ÁREA (ha)	VARIEDADE
999 4.98 %	1	05/2022	12.31	RB 966928
	2		22.82	
	3		11.36	
TOTAL PLANTIO			46.49	--------

ÁREAS	(ha)	(%)
PLANTIO	46.49	94.22
CARREADORES	2.31	4.69
OUTROS	0.00	0.00
SUB TOTAL AGRICULTÁVEL	48.80	98.91
AP.P.	0.00	0.00
ÁRVORES	0.32	0.65
OUTROS	0.22	0.45
SUB TOTAL NÃO AGRICULT.	0.54	1.09
ÁREA TOTAL	49.34	100.00


C. NÍVEL: 5378.01 m/l 1.24 ha 2.51 %

LEGENDA

- FAZENDA
- TALHÃO
- CURVA DE NÍVEL
- CARREADOR
- CONFRONTANTE
- REDE ELÉTRICA
- TRAJETO VAZIO
- TRAJETO CARREGADO


PLANTIO MANUAL - ESPAÇAMENTO: 1.50 X 1.50
TIRO MÉDIO ESTIMADO: 439.53 m

Clealco
Açúcar, Etanol e Energia

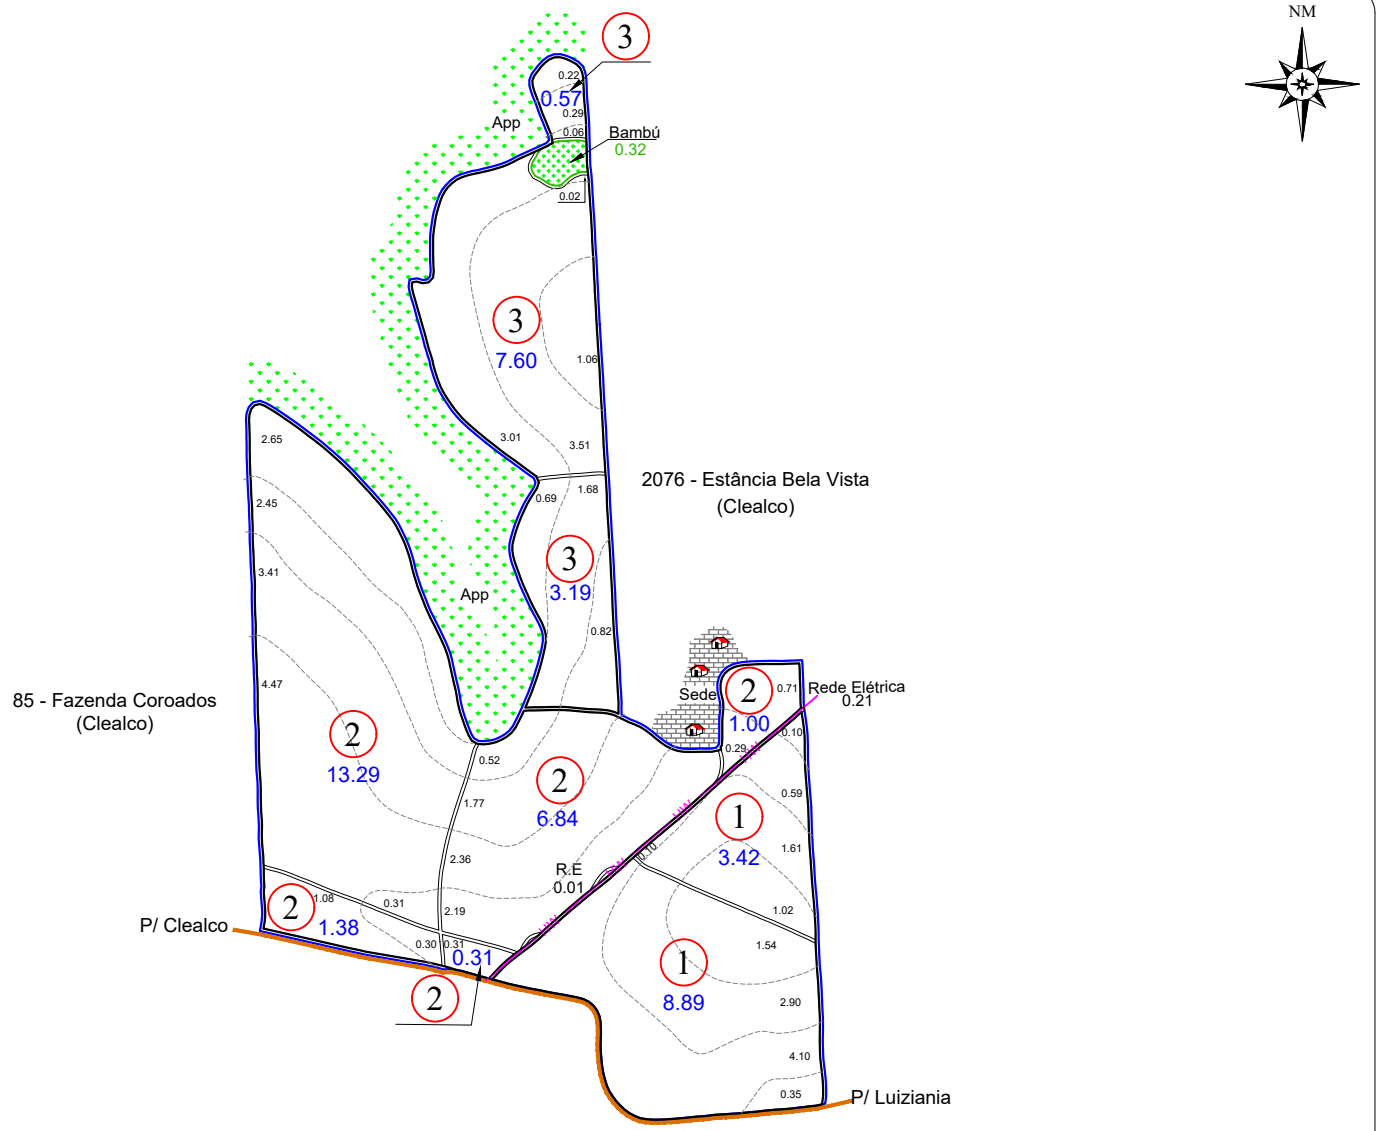

ESCALA: 1: 10.000

CROQUI DE ACESSO

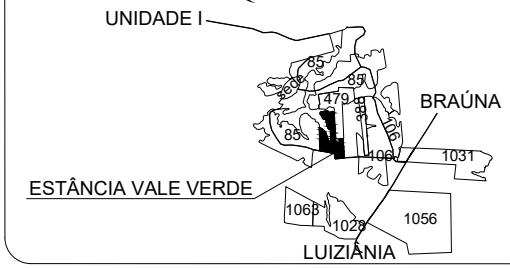

ESTÂNCIA VALE VERDE

PROPRIETÁRIO: CLEBER AMARAL HÚNGARO
COMPRADOR: CLEALCO S/A
MUNICÍPIO: BRAÚNA

DISTÂNCIAS (km):
UNID. I - Asfalto: 0.50 Terra.: 50.00
UNID.I I - Asfalto: 25.00 Terra.: 9.50
UNID. III -Asfalto: 50.00 Terra.: 1.00

COORDENADAS: E(X): 562946.70 N(Y): 7609314.33
LAT: -21°37'5.3428" LONG: -50°23'30.4718"

CLEALCO - AÇÚCAR E ALCOOL S/A - DEPARTAMENTO DE TOPOGRAFIA

UNIDADE: I
PARTE: A/A
FUNDO AGRÍCOLA: 307503

Fernanda Bezerra 22/08/22