ZONA D.V.	Nº TAL.	DATA PL.	ÁREA (ha)	VARIEDADE
999 6.02 %	1	05/2023	12.87	RB 975201
TOTAL PLANTIO			12.87	--------

ÁREAS	(ha)	(%)
PLANTIO	12.87	93.63
CARREADORES	0.83	6.01
OUTROS	0.00	0.00
SUB TOTAL AGRICULTÁVEL	13.70	99.64
AP.P.	0.00	0.00
ÁRVORES	0.05	0.36
OUTROS	0.00	0.00
SUB TOTAL NÃO AGRICULT.	0.05	0.36
ÁREA TOTAL	13.75	100.00

C. NÍVEL:	0.00 m/l	0.00 ha	0.00 %

LEGENDA

▬ FAZENDA	▬ CONFRONTANTE
▬ TALHÃO	-·- REDE ELÉTRICA
▪▪▪ CURVA DE NÍVEL	—▷ TRAJETO VAZIO
— CARREADOR	—► TRAJETO CARREGADO

PLANTIO MANUAL - ESPAÇAMENTO: 1.50 X 1.50
TIRO MÉDIO ESTIMADO: 167.32 m

Clealco®
Açúcar, Etanol e Energia

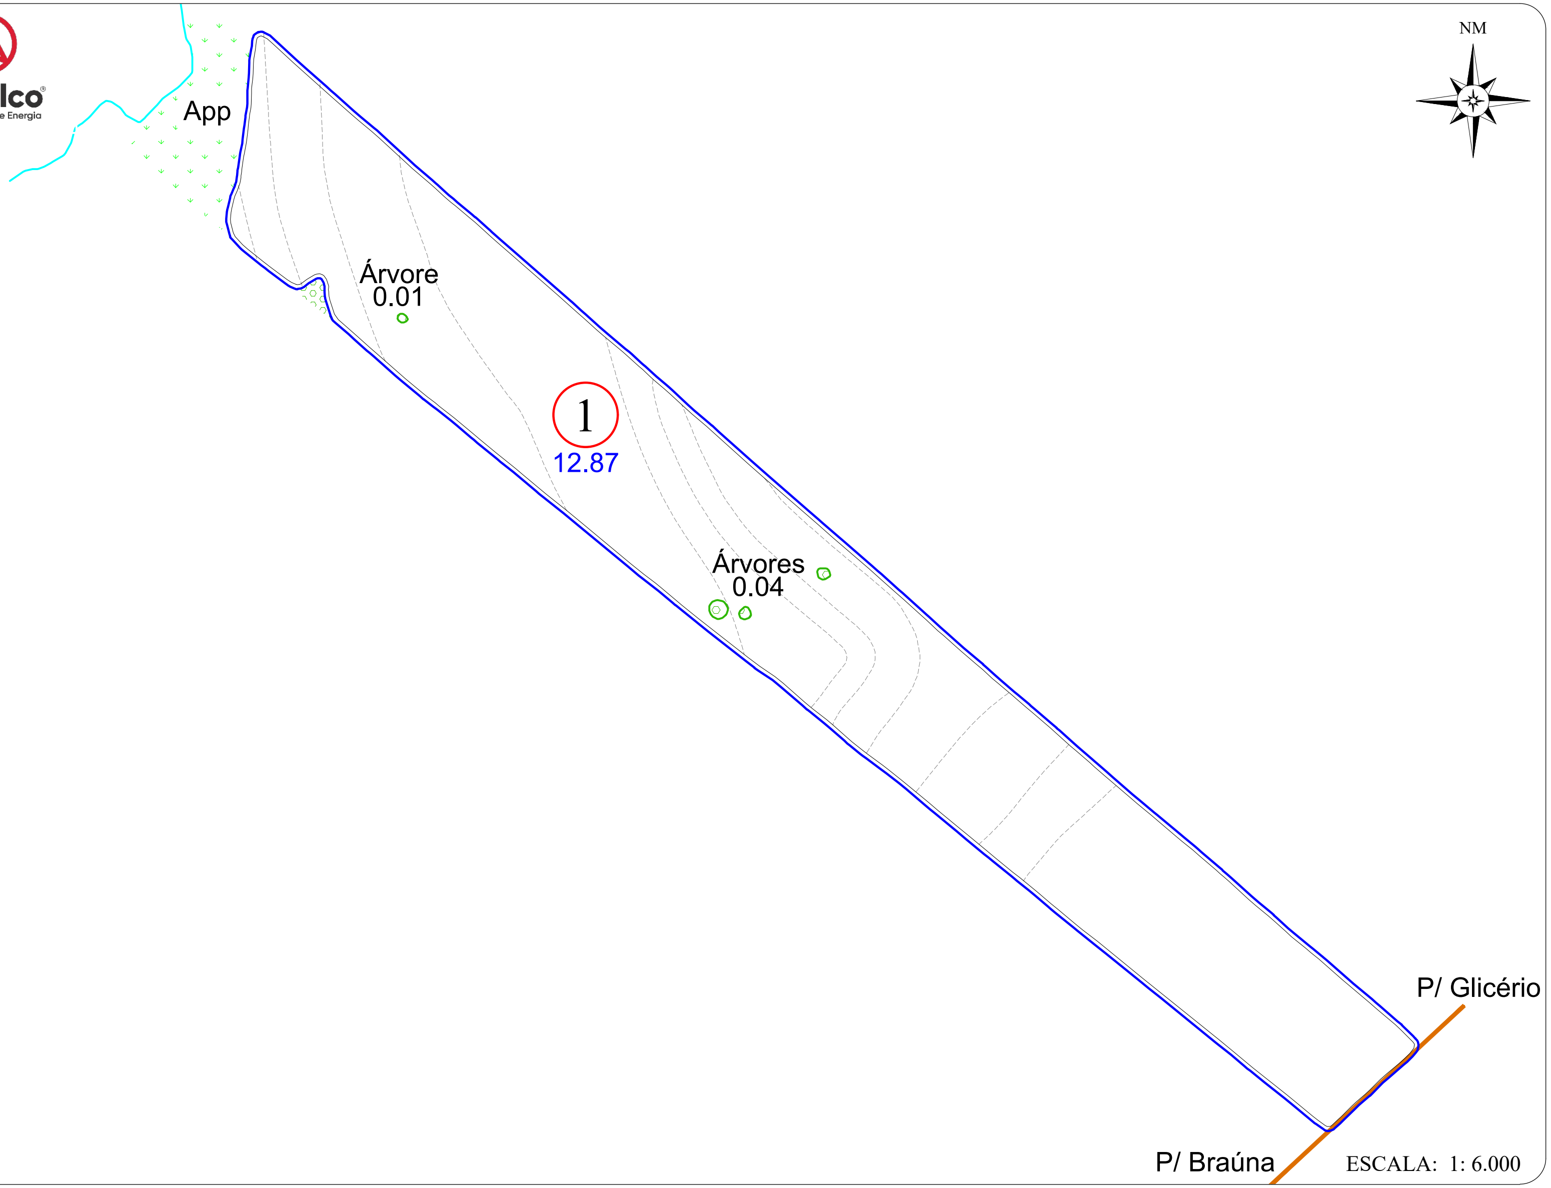

ESCALA: 1: 6.000

CROQUI DE ACESSO

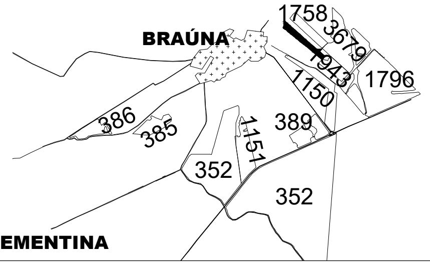

SÍTIO SANTO ANTONIO

PROPRIETÁRIO: FERNANDO BOUGO AVELHAN
COMPRADOR: CLEALCO S/A
MUNICÍPIO: BRAÚNA

DISTÂNCIAS (km):

	Asfalto:	Terra.:
UNID. I -	18.00	1.00
UNID.I I -	78.00	1.50
UNID. III -	10.50	12.50

COORDENADAS: E(X): 572036.70 N(Y): 7622440.58
LAT: -21°29'57.1878" LONG: -50°18'16.3397"

CLEALCO - AÇÚCAR E ALCOOL S/A - DEPARTAMENTO DE TOPOGRAFIA

UNIDADE:
I

PARTE:
A/A

FUNDO AGRÍCOLA:
307511

M:\03-Projetos (Sistematização, Pré, Pós e outros)\Terceiro\2023\Edvaldo\Pós Plantio\307511 - Sítio Santo Antonio (Fernando Bougo Avelhan) Pos Plantio - 2023.dwg

Bruno Gamboa 19/12/23