ZONA D.V.	Nº TAL.	DATA PL.	ÁREA (ha)	VARIEDADE
999 4.82 %	1	05/2023	14.60	RB 975242
	2		4.64	
	3	05/2021	35.56	
TOTAL PLANTIO			54.80	--------


ÁREAS	(ha)	(%)
PLANTIO	54.80	95.73
CARREADORES	2.44	4.27
OUTROS	0.00	0.00
SUB TOTAL AGRICULTÁVEL	57.24	100.00
AP.P.	0.00	0.00
ÁRVORES	0.00	0.00
OUTROS	0.00	0.00
SUB TOTAL NÃO AGRICULT.	0.00	0.00
ÁREA TOTAL	57.24	100.00

C. NÍVEL: 7816.50 m/l 1.80 ha 3.14 %


LEGENDA

- FAZENDA
- TALHÃO
- CURVA DE NÍVEL
- CARREADOR
- CONFRONTANTE
- REDE ELÉTRICA
- TRAJETO VAZIO
- TRAJETO CARREGADO

PLANTIO MANUAL - ESPAÇAMENTO: 1.50 X 1.50
TIRO MÉDIO ESTIMADO: 297.44 m

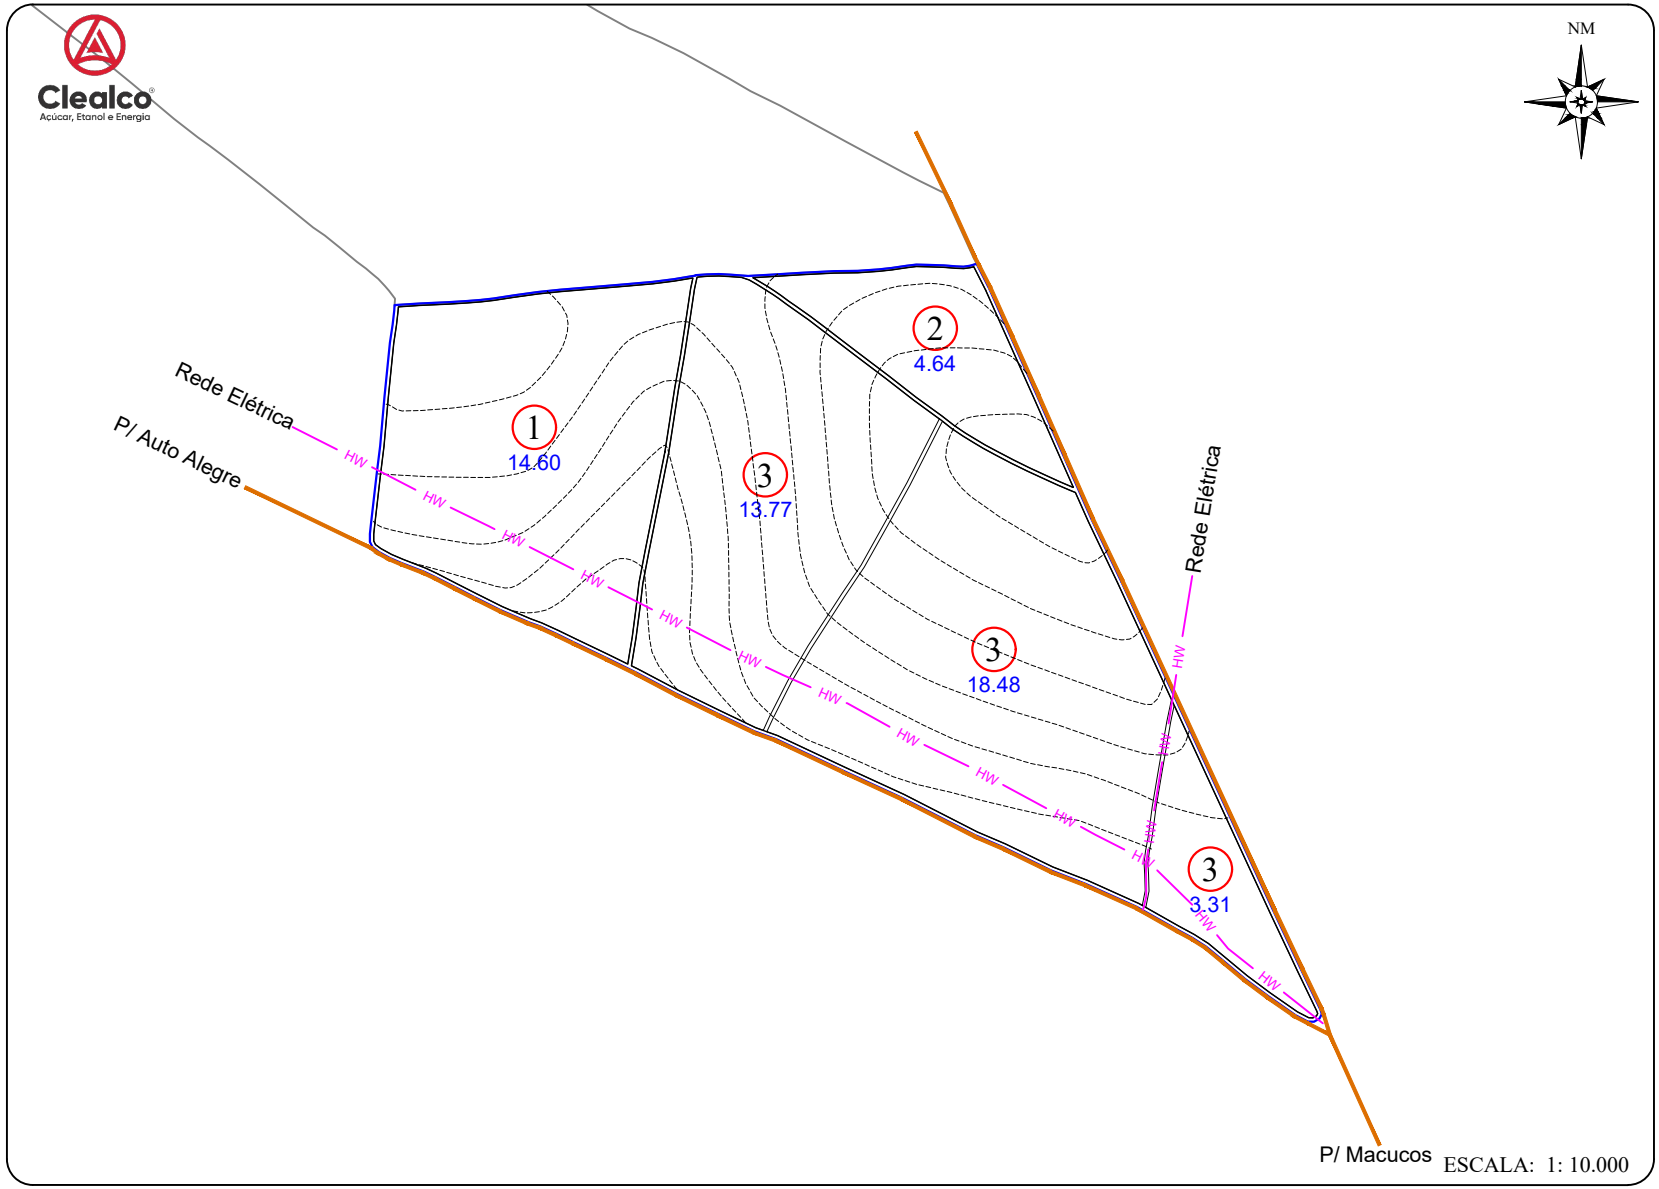

CROQUI DE ACESSO

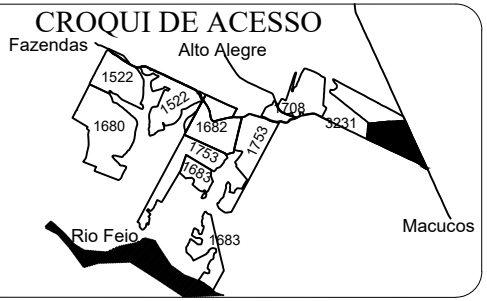

SITIO MACUCOS

PROPRIETÁRIO: JULIO CESAR DAS NEVES
COMPRADOR: CLEALCO S/A
MUNICÍPIO: GETULINA

DISTÂNCIAS (km):
UNID. I - Asfalto: 71.00 Terra.: 3.00
UNID.I I - Asfalto: 14.20 Terra.: 1.80
UNID. III -Asfalto: 16.00 Terra.: 20.00

COORDENADAS: E(X): 588894.59 N(Y): 7595207.67
LAT: -21°44'40.1393" LONG: -50°8'25.2506"

CLEALCO - AÇÚCAR E ALCOOL S/A - DEPARTAMENTO DE TOPOGRAFIA

UNIDADE: II
PARTE: A/A
FUNDO AGRÍCOLA: 307523