ZONA D.V.	Nº TAL.	DATA PL.	ÁREA (ha)	VARIEDADE
1 5.60%	1	04/2024	12.89	RB97 5201
	2		13.52	
	3		19.98	
	4		7.54	
TOTAL PLANTIO			53.93	--------


ÁREAS	(ha)	(%)
PLANTIO	53.93	94.93
CARREADORES	2.88	5.07
OUTROS	0.00	0.00
SUB TOTAL AGRICULTÁVEL	56.81	100.00
AP.P.	0.00	0.00
ÁRVORES	0.00	0.00
OUTROS	0.00	0.00
SUB TOTAL NÃO AGRICULT.	0.00	0.00
ÁREA TOTAL	56.81	100.00

C. NÍVEL: 10969.17 m/l 2.52 ha 4.44 %


LEGENDA

- FAZENDA
- TALHÃO
- CURVA DE NÍVEL
- CARREADOR
- CONFRONTANTE
- REDE ELÉTRICA
- TRAJETO VAZIO
- TRAJETO CARREGADO

PLANTIO MANUAL - ESPAÇAMENTO: 1.50 X 1.50
TIRO MÉDIO ESTIMADO: 115.65m

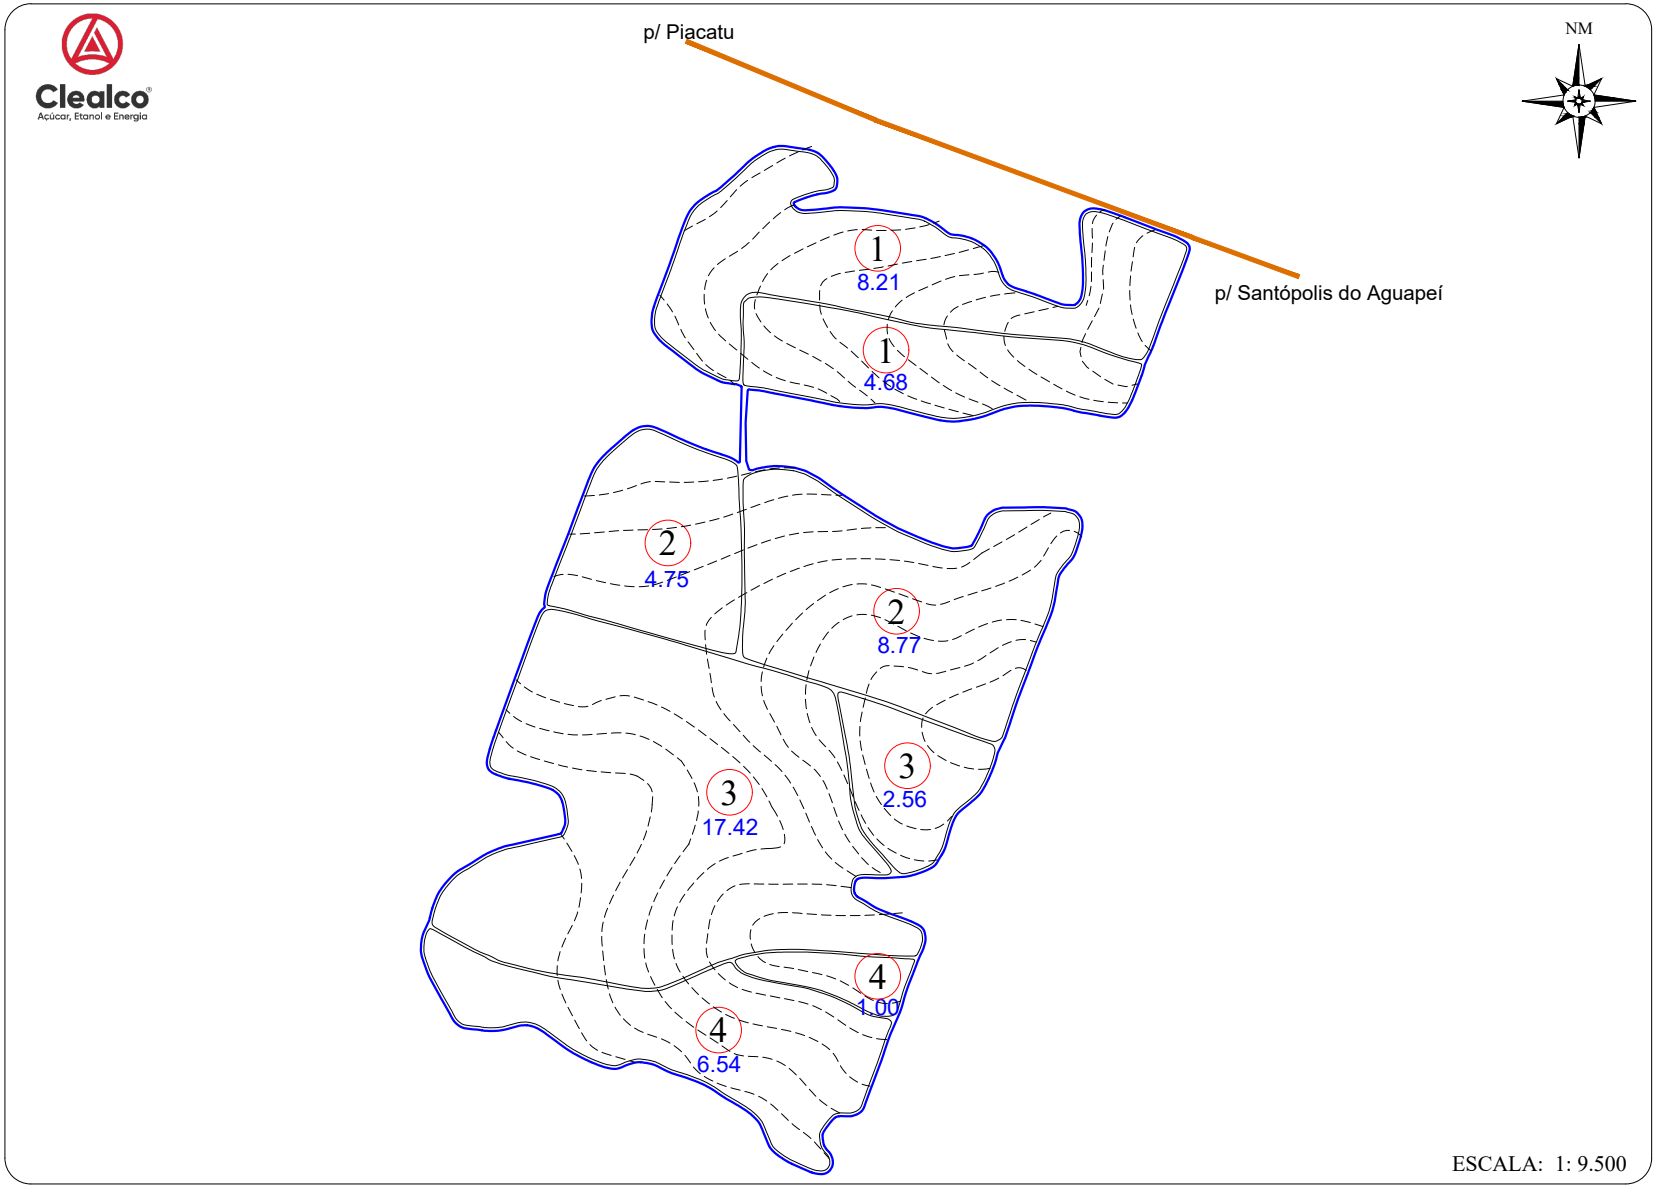

CROQUI DE ACESSO

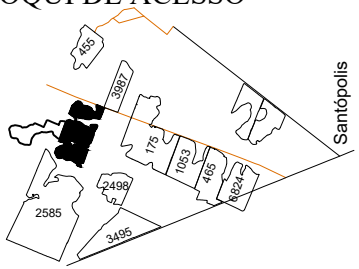

SÍTIO SANTA TEREZINHA

PROPRIETÁRIO: BRUNO MATEUS VENDRAME
COMPRADOR: CLEALCO S/A
MUNICÍPIO: SANTÓPOLIS - SP

DISTÂNCIAS (km):
UNID. I - Asfalto: 17.50 Terra.: 4.50
UNID.I I - Asfalto: 52.00 Terra.: 4.50
UNID. III -Asfalto: 56.00 Terra.: 4.50

COORDENADAS: E(X): 545685.75 N(Y): 7606729.52
LAT: -21°38'31.3080" LONG: -50°33'30.6023"

CLEALCO - AÇÚCAR E ALCOOL S/A - DEPARTAMENTO DE TOPOGRAFIA

UNIDADE: I
PARTE: A/A
FUNDO AGRÍCOLA: 307531

M:\01-Mapa de safra\Mapas Atualizados\Terceiro\307531 - Santa Terezinha (Bruno Mateus Vendrame)\307531 - Santa Terezinha (Bruno Mateus Vendrame).dwg

Benati 03/10/2024