D.V.	Nº TAL.	DATA PL.	ÁREA (ha)	VARIEDADE
%	1	04/2024	15.15	CTC 04
	2		13.34	
	3		8.75	
	4		7.86	
TOTAL PLANTIO			45.10	

ÁREAS	(ha)	(%)
PLANTIO	45.10	93.55
CARREADORES	2.85	5.91
OUTROS	0.00	0.00
SUB TOTAL AGRICULTÁVEL	47.95	99.46
AP.P.	0.00	0.00
ÁRVORES	0.26	0.54
OUTROS	0.09	0.00
SUB TOTAL NÃO AGRICULT.	0.35	0.54
ÁREA TOTAL	48.56	100.00


C. NÍVEL: 508.34 m/l 0.12 ha 0.24 %

LEGENDA


- FAZENDA
- TALHÃO
- REDE ELÉTRICA
- TERRAÇO BASE LARGA
- TERRAÇO EMBUTIDO

ESPAÇAMENTO: 0.00 x 0.00

TIRO MÉDIO ESTIMADO: 287.36 m

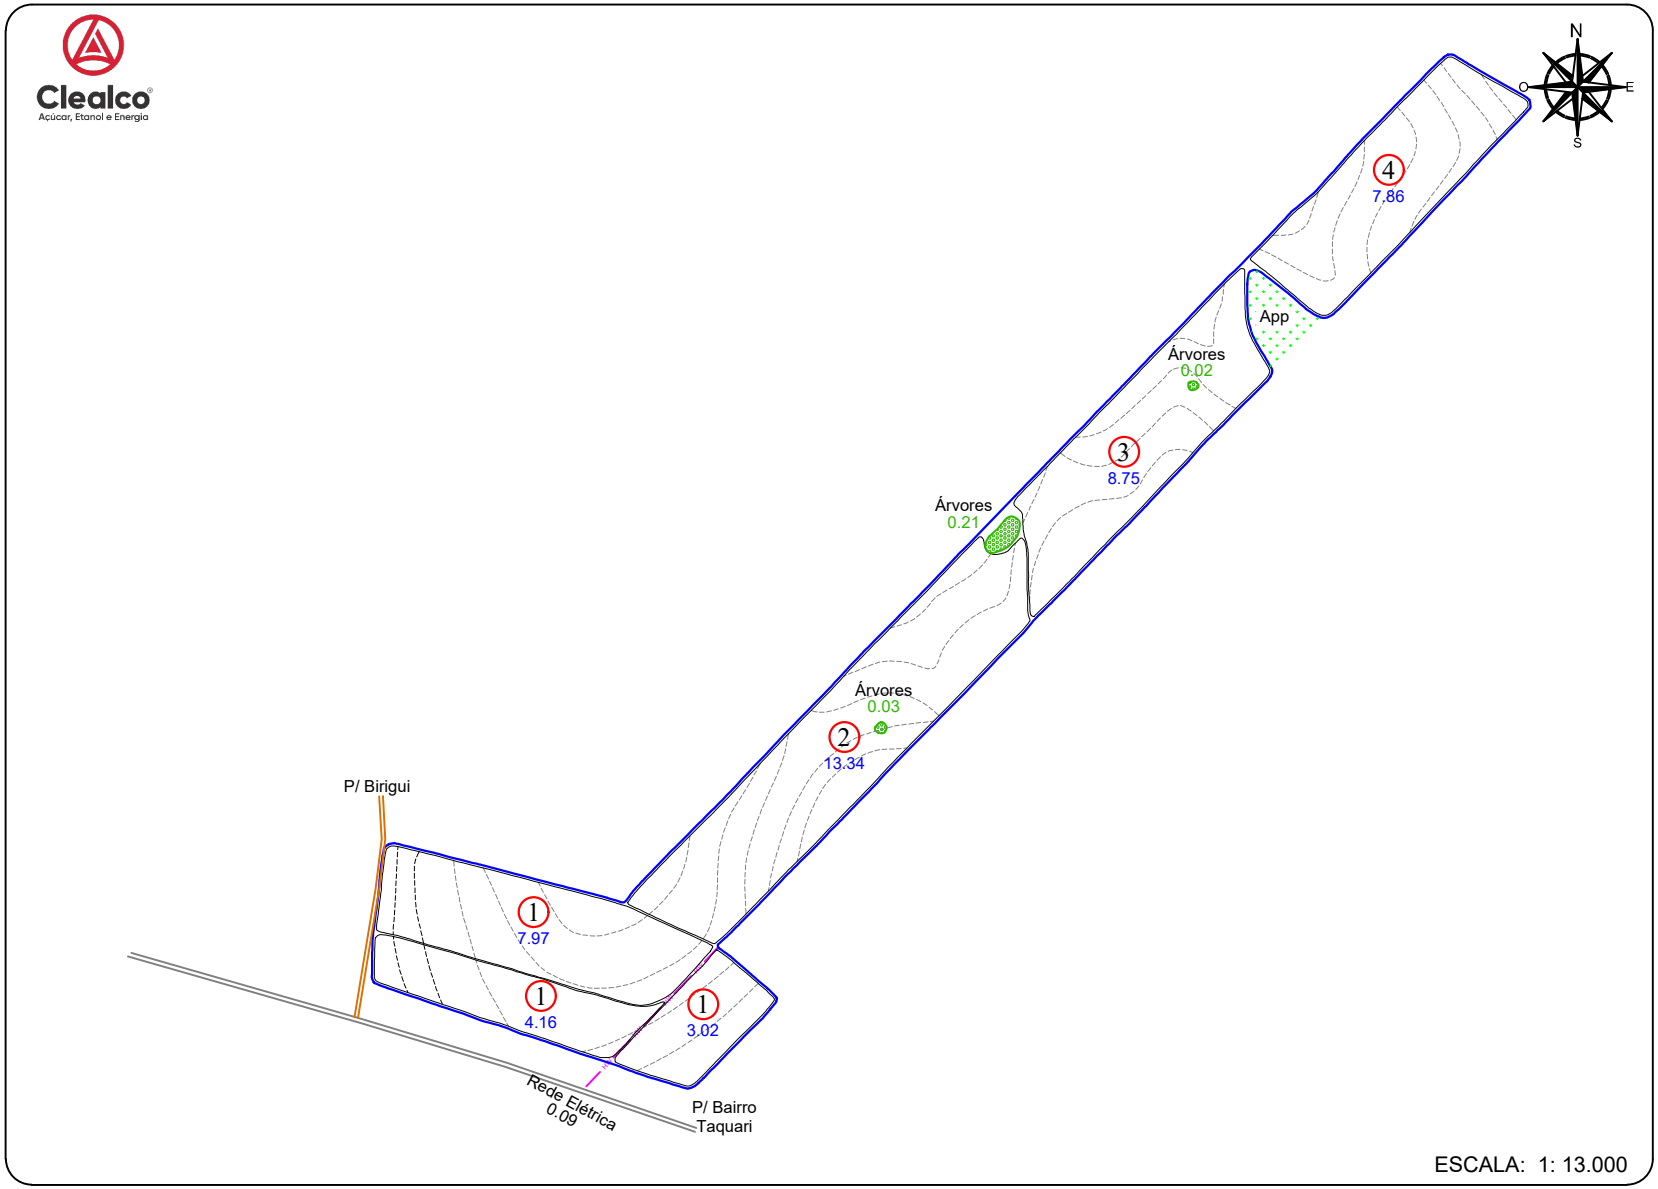

CROQUI DE ACESSO

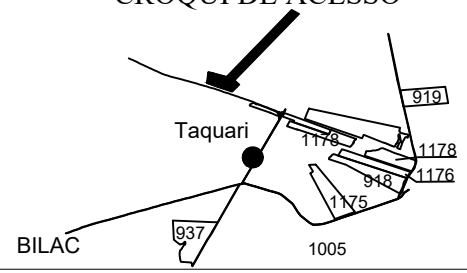

ESTÂNCIA BRISA

PROPRIETÁRIO: LUIZ LUCHETI
COMPRADOR: CLEALCO S/A
MUNICÍPIO: BIRIGUI

DISTÂNCIAS (km):
UNID. I - Asfalto: 28.00 Terra.: 1.50
UNID.I I - Asfalto: 83.50 Terra.: 4.50
UNID. III -Asfalto: 36.00 Terra.: 11.00

COORDENADAS: E(X): 561871.96 N(Y): 7637877.81
LAT: -21°21'36.4604" LONG: -50°24'11.6446"

CLEALCO - AÇÚCAR E ALCOOL S/A - DEPARTAMENTO DE TOPOGRAFIA

UNIDADE: I

PARTE: A/A

FUNDO AGRÍCOLA: 307544

M:\01-Mapa de safra\Mapas Atualizados\Terceiro\307544 - Estancia Brisa (Luiz Lucheti)\307544 - Estancia Brisa (Luiz Lucheti).dwg

Bruno Gamboa 02/07/25