ZONA D.V.	Nº TAL.	DATA PL.	ÁREA (ha)	VARIEDADE
1 5.60 %	1	04/2024	39.23	CTC 04
	2		26.85	
TOTAL PLANTIO			66.08	--------

ÁREAS	(ha)	(%)
PLANTIO	66.08	95.28
CARREADORES	1.87	2.69
OUTROS	0.00	0.00
SUB TOTAL AGRICULTÁVEL	67.95	97.97
AP.P.	0.00	0.00
ÁRVORES	0.00	0.00
OUTROS	1.41	2.03
SUB TOTAL NÃO AGRICULT.	1.41	2.03
ÁREA TOTAL	69.36	100.00

C. NÍVEL:	9393.55 m/l	2.16 ha	3.12 %

LEGENDA

▬ FAZENDA	▬ CONFRONTANTE
▬ TALHÃO	-·- REDE ELÉTRICA
▪▪▪ CURVA DE NÍVEL	─▷ TRAJETO VAZIO
─ CARREADOR	─► TRAJETO CARREGADO

PLANTIO MANUAL - ESPAÇAMENTO: 1.50 X 1.50
TIRO MÉDIO ESTIMADO: 266.71 m

Clealco
Açúcar, Etanol e Energia

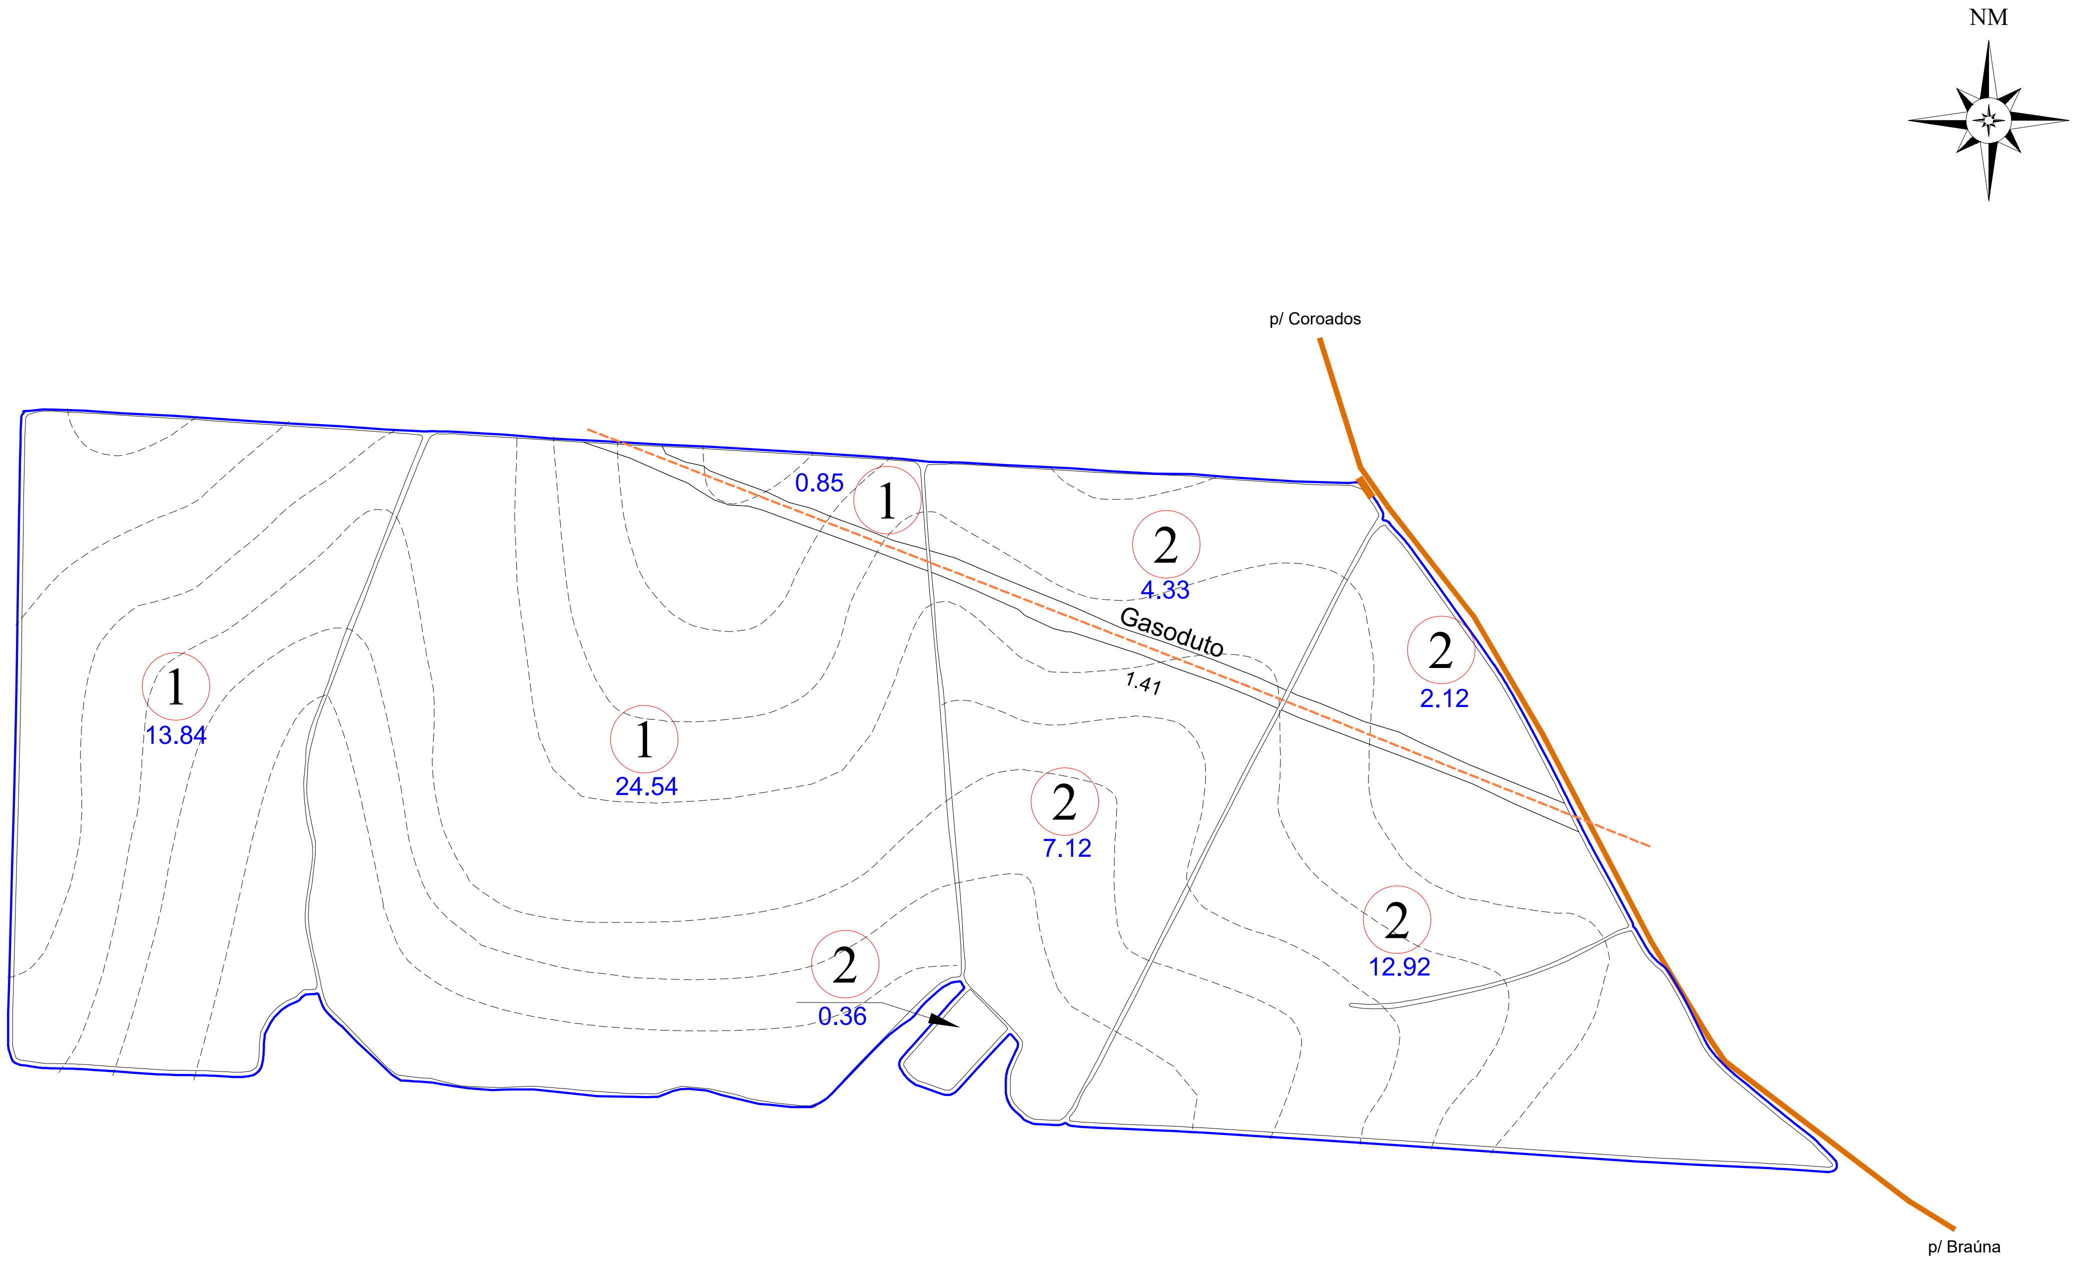

ESCALA: 1: 10.000

CROQUI DE ACESSO

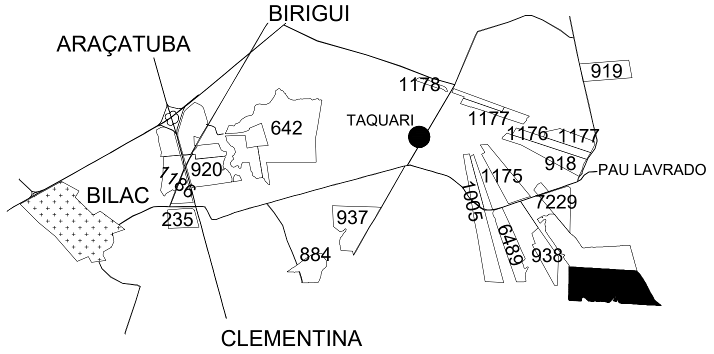

FAZENDA CONQUISTA

PROPRIETÁRIO:	MILTON LUCHETI
COMPRADOR:	CLEALCO S/A
MUNICÍPIO:	BIRIGUI

DISTÂNCIAS (km):

UNID. I -	Asfalto:	30.50	Terra.:	0.10
UNID.I I -	Asfalto:	85.50	Terra.:	0.10
UNID. III -	Asfalto:	40.00	Terra.:	0.10

COORDENADAS:				
	E(X):	564506.74	N(Y):	7632257.15
	LAT:	-21°24'38.9398"	LONG:	-50°22'39.3890"

CLEALCO - AÇÚCAR E ALCOOL S/A - DEPARTAMENTO DE TOPOGRAFIA

UNIDADE:
I

PARTE:
A/A

FUNDO AGRÍCOLA:
307549