ZONA D.V.	Nº TAL.	DATA PL.	ÁREA (ha)	VARIEDADE
999 6.17%	1	04/2023	17.67	RB 966928
TOTAL PLANTIO			17.67	--------

ÁREAS	(ha)	(%)
PLANTIO	17.67	95.63
CARREADORES	0.70	3.77
OUTROS	0.00	0.00
SUB TOTAL AGRICULTÁVEL	18.37	99.40
AP.P.	0.00	0.00
ÁRVORES	0.11	0.60
OUTROS	0.00	0.00
SUB TOTAL NÃO AGRICULT.	0.11	0.60
ÁREA TOTAL	18.48	100.00

C. NÍVEL: 1469.32 m/l 0.34 ha 1.83 %

LEGENDA

▬ FAZENDA	▬ CONFRONTANTE
▬ TALHÃO	-·- REDE ELÉTRICA
▪▪▪ CURVA DE NÍVEL	→ TRAJETO VAZIO
— CARREADOR	→ TRAJETO CARREGADO

PLANTIO MANUAL - ESPAÇAMENTO: 1.50 X 1.50
TIRO MÉDIO ESTIMADO: 000.00m

Clealco®
Açúcar, Etanol e Energia

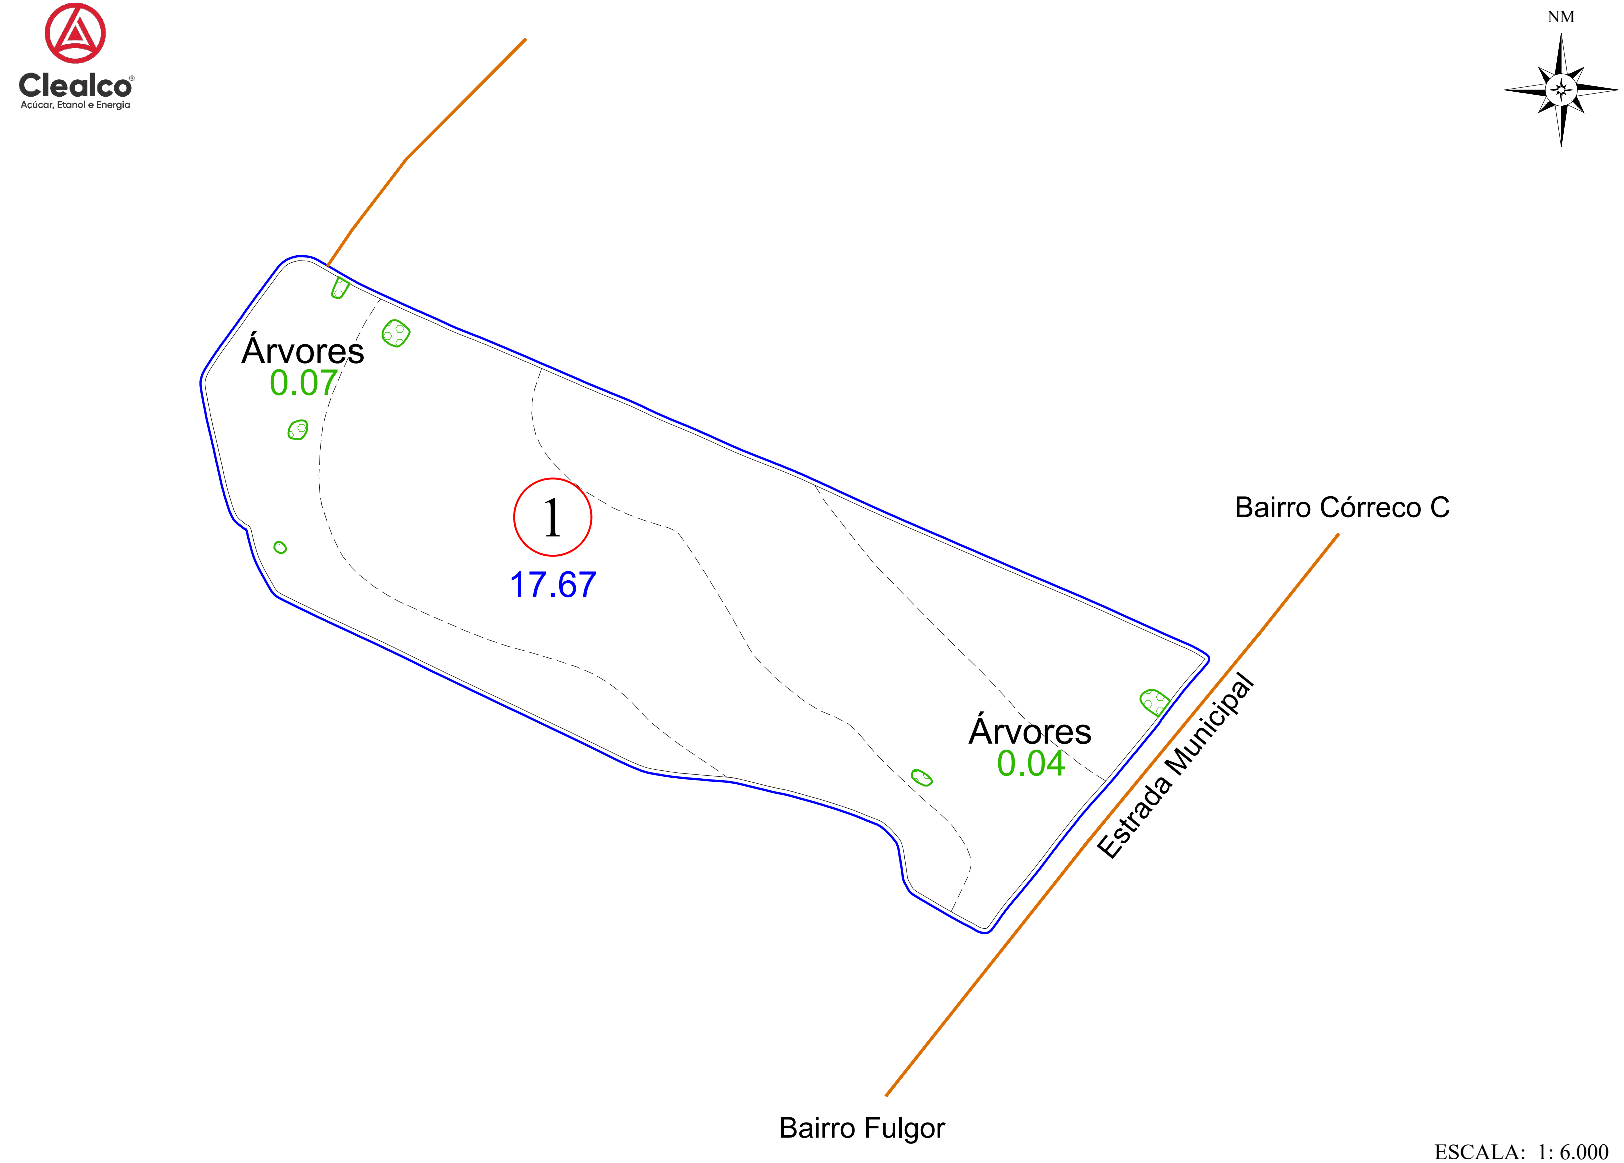

ESCALA: 1: 6.000

CROQUI DE ACESSO

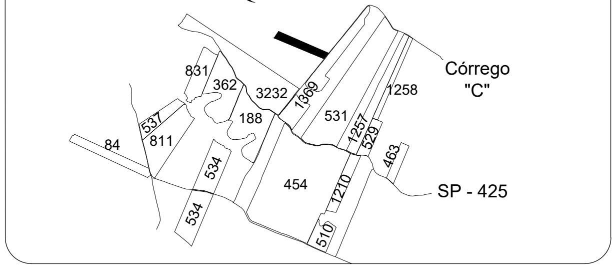

SÍTIO LOPES

PROPRIETÁRIO: CSAGRO ADM DE IMOVEIS PROPRIOS
COMPRADOR: CLEALCO S/A
MUNICÍPIO: CLEMENTINA

DISTÂNCIAS (km):

UNID. I -	Asfalto:	3.50	Terra.:	7.00
UNID.I I -	Asfalto:	53.00	Terra.:	7.00
UNID. III -	Asfalto:	40.00	Terra.:	7.00

COORDENADAS: E(X): 550757.79 N(Y): 7614409.06
LAT: -21°34'21.0378" LONG: -50°30'34.9939"

CLEALCO - AÇÚCAR E ALCOOL S/A - DEPARTAMENTO DE TOPOGRAFIA

UNIDADE:
I
PARTE:
A/A
FUNDO AGRÍCOLA:
307554

M:\01-Mapa de safra\Mapas Atualizados\Terceiro\307554 - Sítio Lopes (CSAgro Administração)\307554 - Sítio Lopes (CSAgro Administração).dwg

Bruno Gamboa 15/09/23