
Clealco
Açúcar, Etanol e Energia

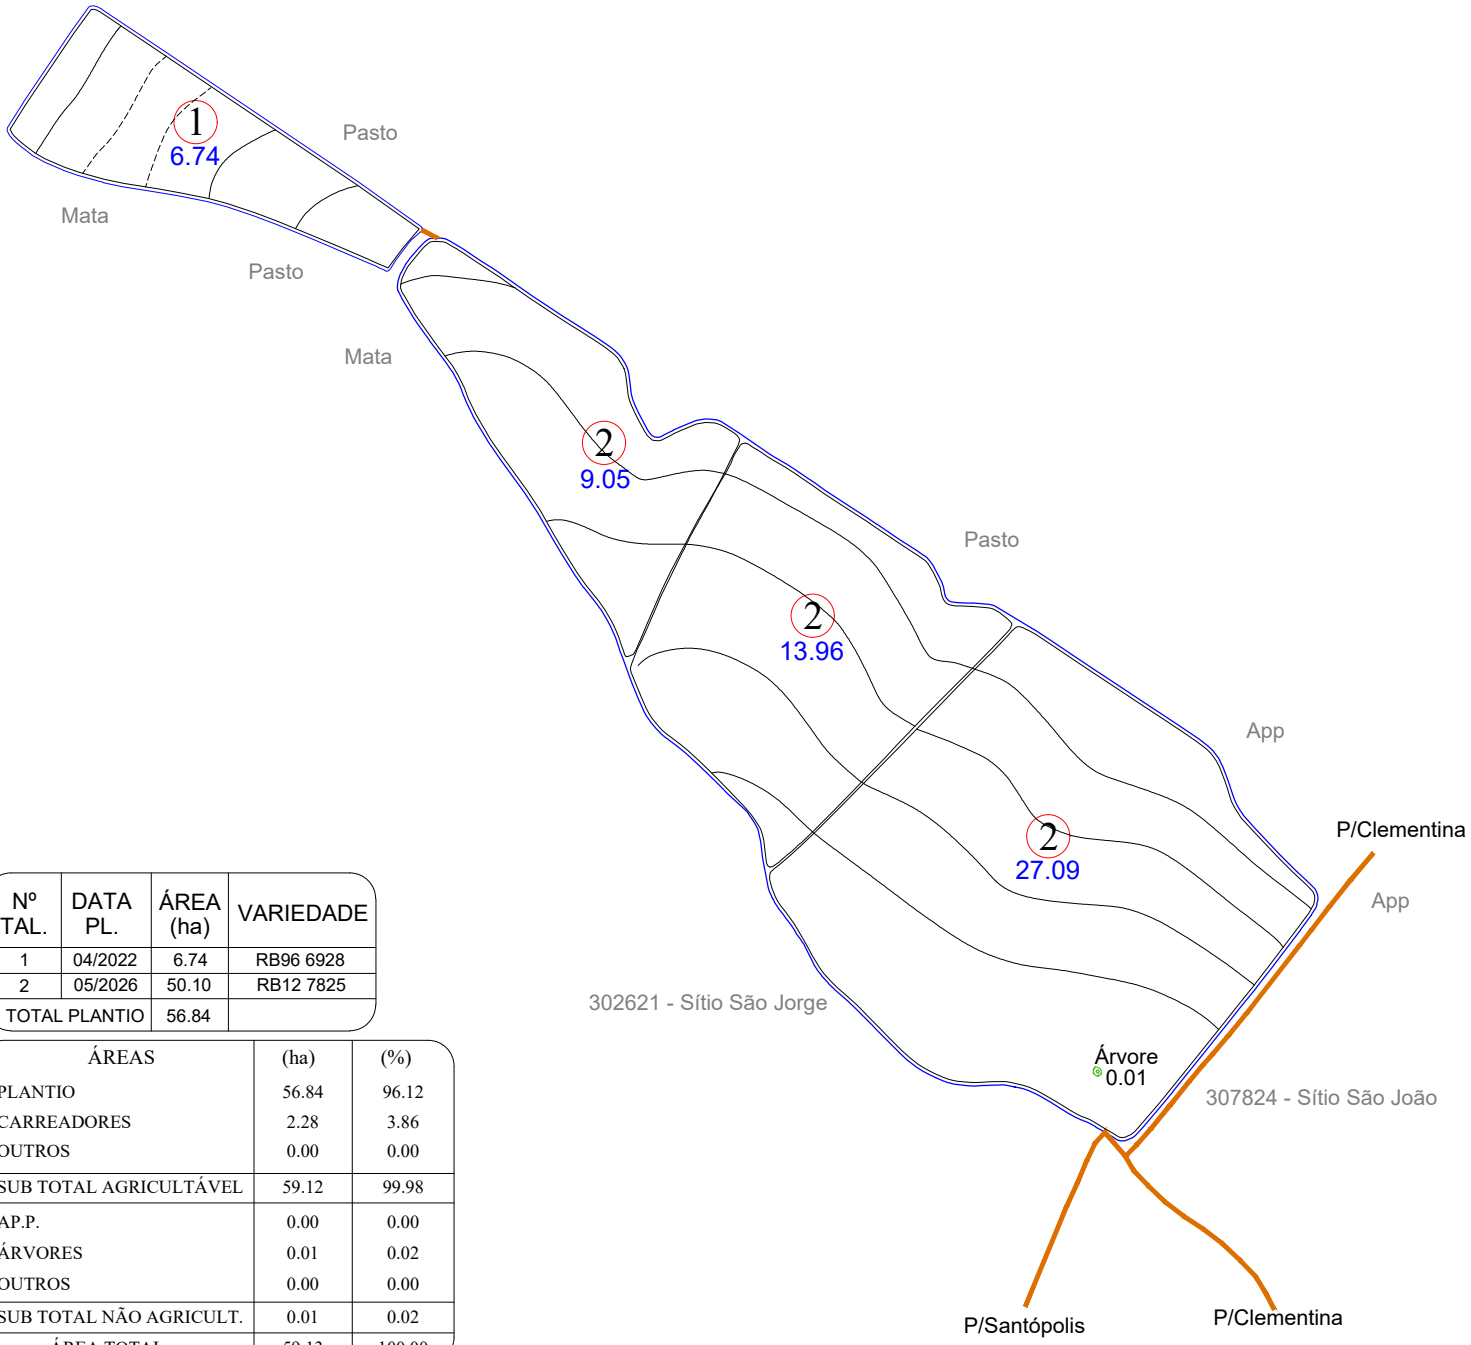

Nº TAL.	DATA PL.	ÁREA (ha)	VARIEDADE
1	04/2022	6.74	RB96 6928
2	05/2026	50.10	RB12 7825
TOTAL PLANTIO		56.84	

ÁREAS	(ha)	(%)
PLANTIO	56.84	96.12
CARREADORES	2.28	3.86
OUTROS	0.00	0.00
SUB TOTAL AGRICULTÁVEL	59.12	99.98
AP.P.	0.00	0.00
ÁRVORES	0.01	0.02
OUTROS	0.00	0.00
SUB TOTAL NÃO AGRICULT.	0.01	0.02
ÁREA TOTAL	59.13	100.00

C. NÍVEL:	4838.87 m/l	1.11 ha	1.88 %


LEGENDA

- FAZENDA
- TALHÃO
- REDE ELÉTRICA
- TERRAÇO BASE LARGA
- TERRAÇO EMBUTIDO
- (P.O.A) PATIO DE OPERAÇÃO

ESPAÇAMENTO: 1.50 x 1.50
TIRO MÉDIO ESTIMADO: 340.97 m
D.V: 5.00 %

ESCALA: 1: 10.000

CROQUI DE ACESSO

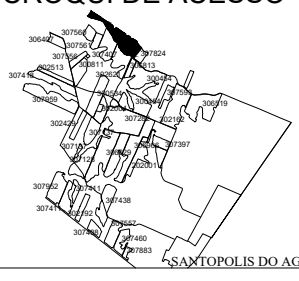

SÍTIO LOPES I

PROPRIETÁRIO: CS AGRO ADMINISTRAÇÃO
COMPRADOR: CLEALCO
MUNICÍPIO: CLEMENTINA- SP

DISTÂNCIAS (km):
UNID. I - Asfalto: 11.50 Terra.: 6.50
UNID.I I - Asfalto: 53.00 Terra.: 6.00

COORDENADAS: E(X): 549792.66 N(Y): 7614038.87
LAT: -21°34'33.1760" LONG: -50°31'8.5137"
CLEALCO - AÇÚCAR E ALCOOL S/A - DEPARTAMENTO DE GEOTECNOLOGIA

LEVANTAMENTO VIA:
- SATÉLITE
- GPS / VANT
- GOOGLE

UNIDADE: I
PARTE: A/A
FUNDO AGRÍCOLA: 307559

M:\01-Mapa de safra\Mapas Atualizados\Terceiro\307559 - Sítio Lopes I (CsAgro Administração de Moveis Proprios)\307559 - Sítio Lopes I (CsAgro Administração de Moveis Proprios).dwg

Bruno Gamboa 22/09/26