
Clealco
Açúcar, Etanol e Energia

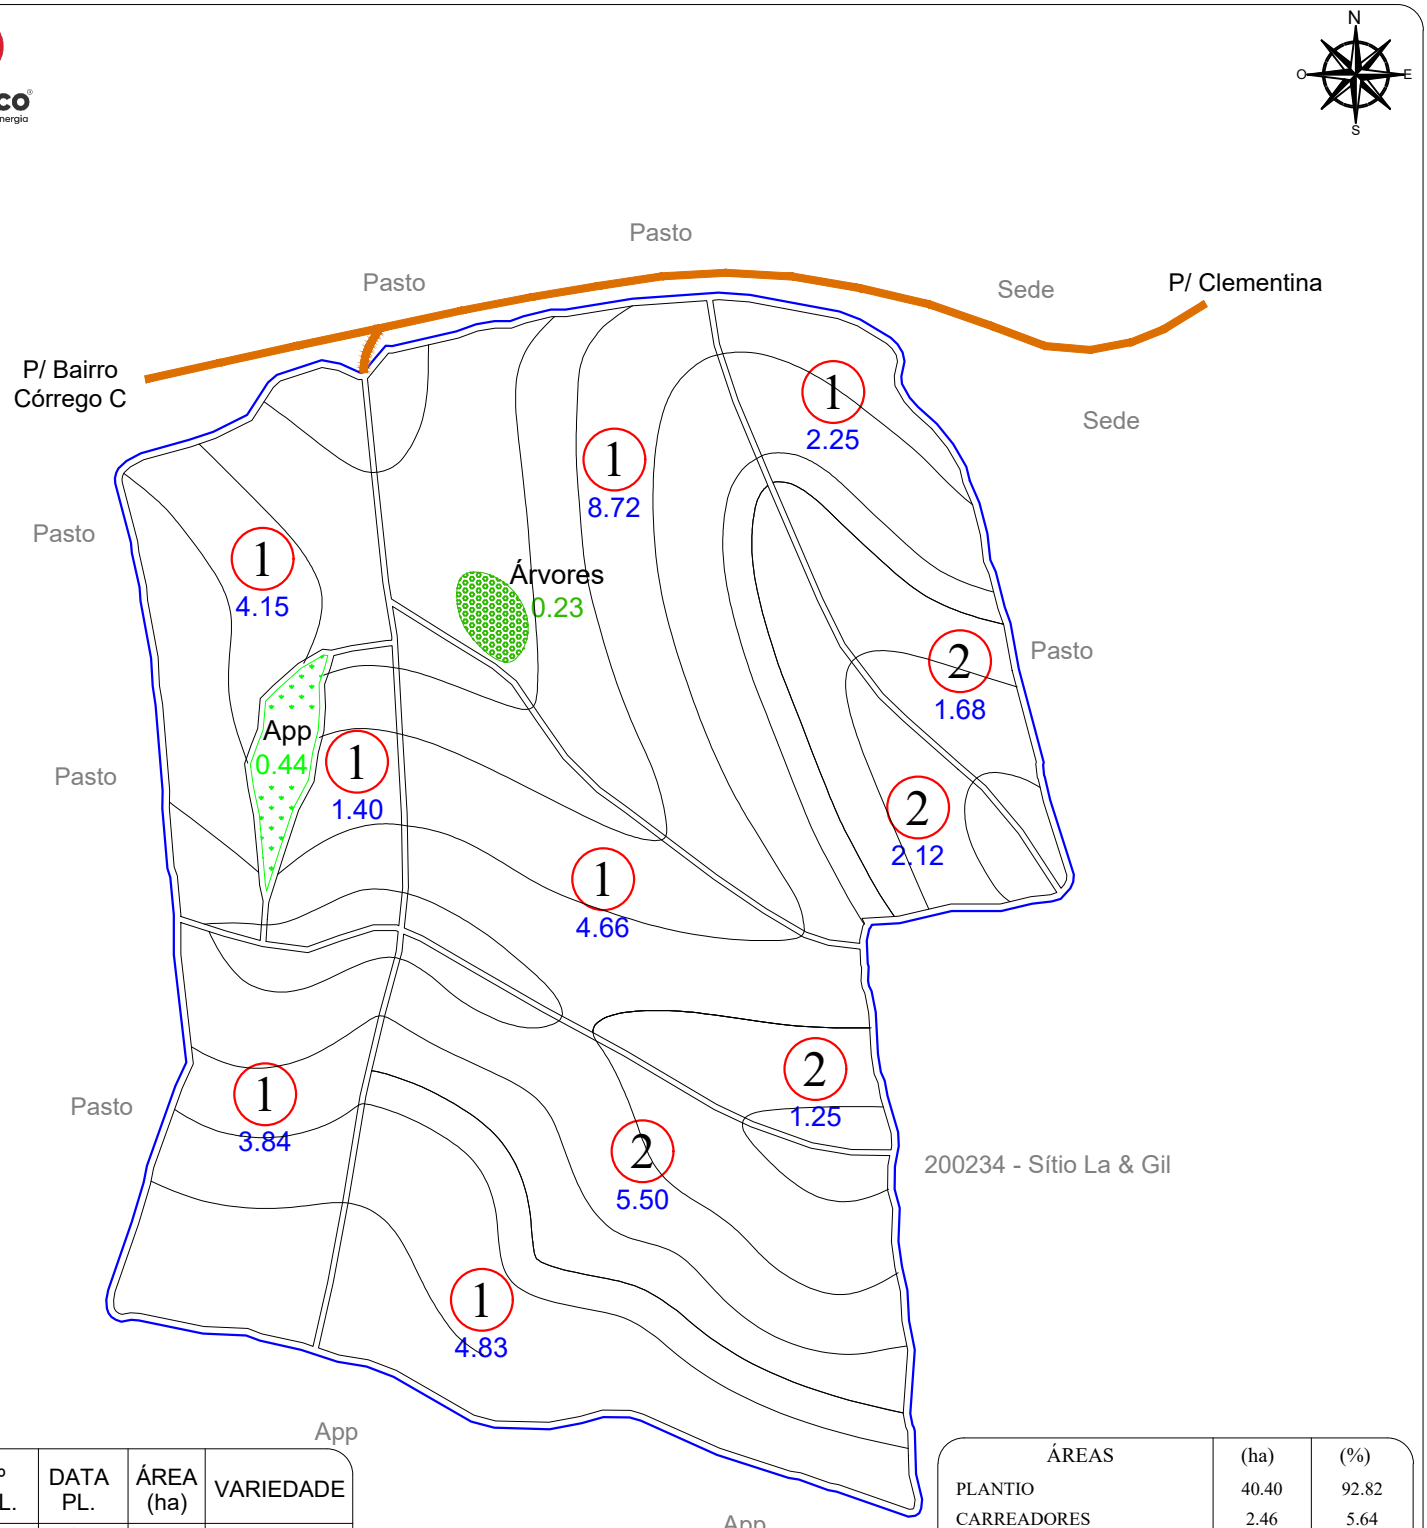

ZONA	Nº TAL.	DATA PL.	ÁREA (ha)	VARIEDADE
1	1	05/2026	29.85	RB98 5033
	2	05/2025	10.55	RB96 6928
TOTAL PLANTIO			40.40	

LEGENDA

- FAZENDA
- TALHÃO
- REDE ELÉTRICA
- TERRAÇO BASE LARGA
- TERRAÇO EMBUTIDO
- (P.O.A) PATIO DE OPERAÇÃO


ESPAÇAMENTO: 1.50 x 1.50
TIRO MÉDIO ESTIMADO: 181.80 m
D.V: 6.85 %

ÁREAS	(ha)	(%)
PLANTIO	40.40	92.82
CARREADORES	2.46	5.64
OUTROS	0.00	0.00
SUB TOTAL AGRICULTÁVEL	42.86	98.46
AP.P.	0.44	1.01
MATA	0.23	0.53
OUTROS	0.00	0.00
SUB TOTAL NÃO AGRICULT.	0.67	1.54
ÁREA TOTAL	43.53	100.00

C. NÍVEL: 6803.73 m/l 1.56 ha 3.60 %

ESCALA: 1: 5.500

CROQUI DE ACESSO

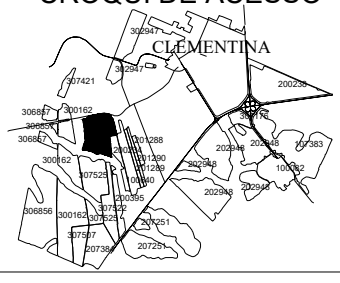

SÍTIO GUAPORÉ

PROPRIETÁRIO: CSAGRO ADM. DE IMÓVEIS PRÓPRIOS
COMPRADOR: CLEALCO
MUNICÍPIO: CLEMENTINA - SP

DISTÂNCIAS (km):
UNID. I - Asfalto: 5.00 Terra.: 1.00
UNID.I I - Asfalto: 53.00 Terra.: 6.00

COORDENADAS: E(X): 555199.73 N(Y): 7614140.31
LAT: -21°34'29.3044" LONG: -50°28'0.5066"

CLEALCO - AÇÚCAR E ALCOOL S/A - DEPARTAMENTO DE GEOTECNOLOGIA

LEVANTAMENTO VIA:
- SATÉLITE
- GPS / VANT
- GOOGLE

UNIDADE: I
PARTE: A/A
FUNDO AGRÍCOLA: 307562

M:\01-Mapa de safra\Mapas Atualizados\Terceiro\307562 - Sitio Guaporé (CSAgro Administração)\307562 - Sitio Guaporé (CSAgro Administração).dwg

Bruno Gamboa 26/06/26