ZONA D.V.	Nº TAL.	DATA PL.	ÁREA (ha)	VARIEDADE
999 3.81 %	1	00/2024	20.95	VARIEDADE
	2		22.06	
	3		20.01	
	4		22.55	
	5		12.92	
	6		23.60	
	7		10.54	
	8		3.50	
	9	04/2023	19.42	DIVERSAS
TOTAL PLANTIO			155.55	--------

ÁREAS	(ha)	(%)
PLANTIO	155.55	96.88
CARREADORES	5.01	3.12
OUTROS	0.00	0.00
SUB TOTAL AGRICULTÁVEL	160.56	100.00
AP.P.	0.00	0.00
ÁRVORES	0.00	0.00
OUTROS	0.00	0.00
SUB TOTAL NÃO AGRICULT.	0.00	0.00
ÁREA TOTAL	160.56	100.00


C. NÍVEL: 3229.32 m/l 0.74 ha 0.46 %

LEGENDA

- FAZENDA
- TALHÃO
- CURVA DE NÍVEL
- CARREADOR
- CONFRONTANTE
- REDE ELÉTRICA
- TRAJETO VAZIO
- TRAJETO CARREGADO


PLANTIO MANUAL - ESPAÇAMENTO: 1.50 X 1.50
TIRO MÉDIO ESTIMADO: 363.14 m

Clealco
Açúcar, Etanol e Energia

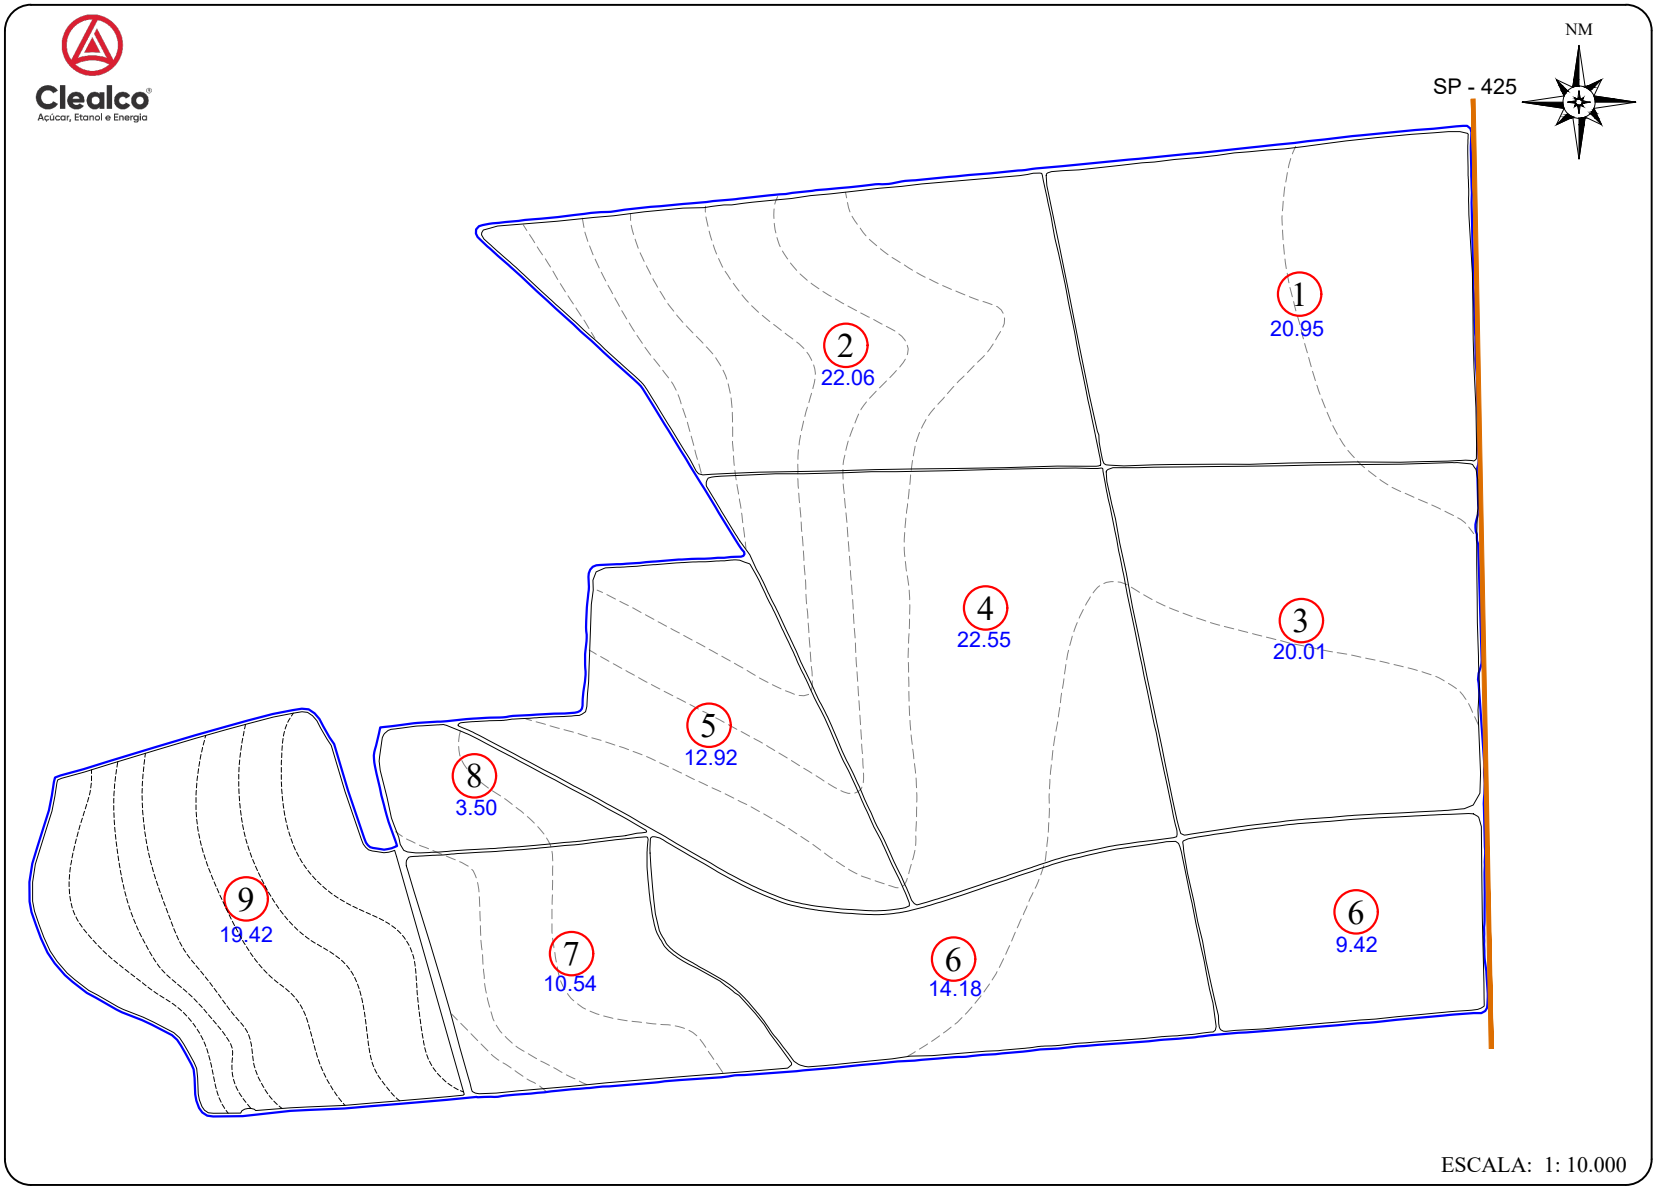

ESCALA: 1: 10.000

CROQUI DE ACESSO

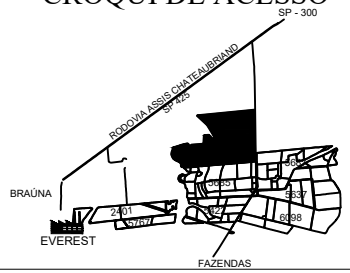

FAZENDA SÃO PEDRO

PROPRIETÁRIO: JOÃO FÁBIO CARRIJO BLACO
COMPRADOR: CLEALCO S/A
MUNICÍPIO: PENÁPOLIS

DISTÂNCIAS (km):
UNID. I - Asfalto: 34.80 Terra.: 1.50
UNID.I I - Asfalto: 63.30 Terra.: 1.50
UNID. III -Asfalto: 11.10 Terra.: 1.50

COORDENADAS: E(X): 587078.39 N(Y): 7625861.65
LAT: -21°28'3.5211" LONG: -50°9'34.2383"

CLEALCO - AÇÚCAR E ALCOOL S/A - DEPARTAMENTO DE TOPOGRAFIA

UNIDADE: I
PARTE: A/A
FUNDO AGRÍCOLA: 307571