ZONA D.V.	Nº TAL.	DATA PL.	ÁREA (ha)	VARIEDADE
999 6.36 %	1	05/2023	9.12	CTC 04
TOTAL PLANTIO			9.12	--------

ÁREAS	(ha)	(%)
PLANTIO	9.12	91.09
CARREADORES	0.89	8.91
OUTROS	0.00	0.00
SUB TOTAL AGRICULTÁVEL	10.01	100.00
AP.P.	0.00	0.00
ÁRVORES	0.00	0.00
OUTROS	0.00	0.00
SUB TOTAL NÃO AGRICULT.	0.00	0.00
ÁREA TOTAL	10.01	100.00

C. NÍVEL:	1132.56 m/l	0.26 ha	2.60 %

LEGENDA

▬ FAZENDA	▬ CONFRONTANTE
▬ TALHÃO	-·- REDE ELÉTRICA
▪▪▪ CURVA DE NÍVEL	—▷ TRAJETO VAZIO
— CARREADOR	—➤ TRAJETO CARREGADO

PLANTIO MANUAL - ESPAÇAMENTO: 1.50 X 1.50
TIRO MÉDIO ESTIMADO: 157.95 m

Clealco®
Açúcar, Etanol e Energia

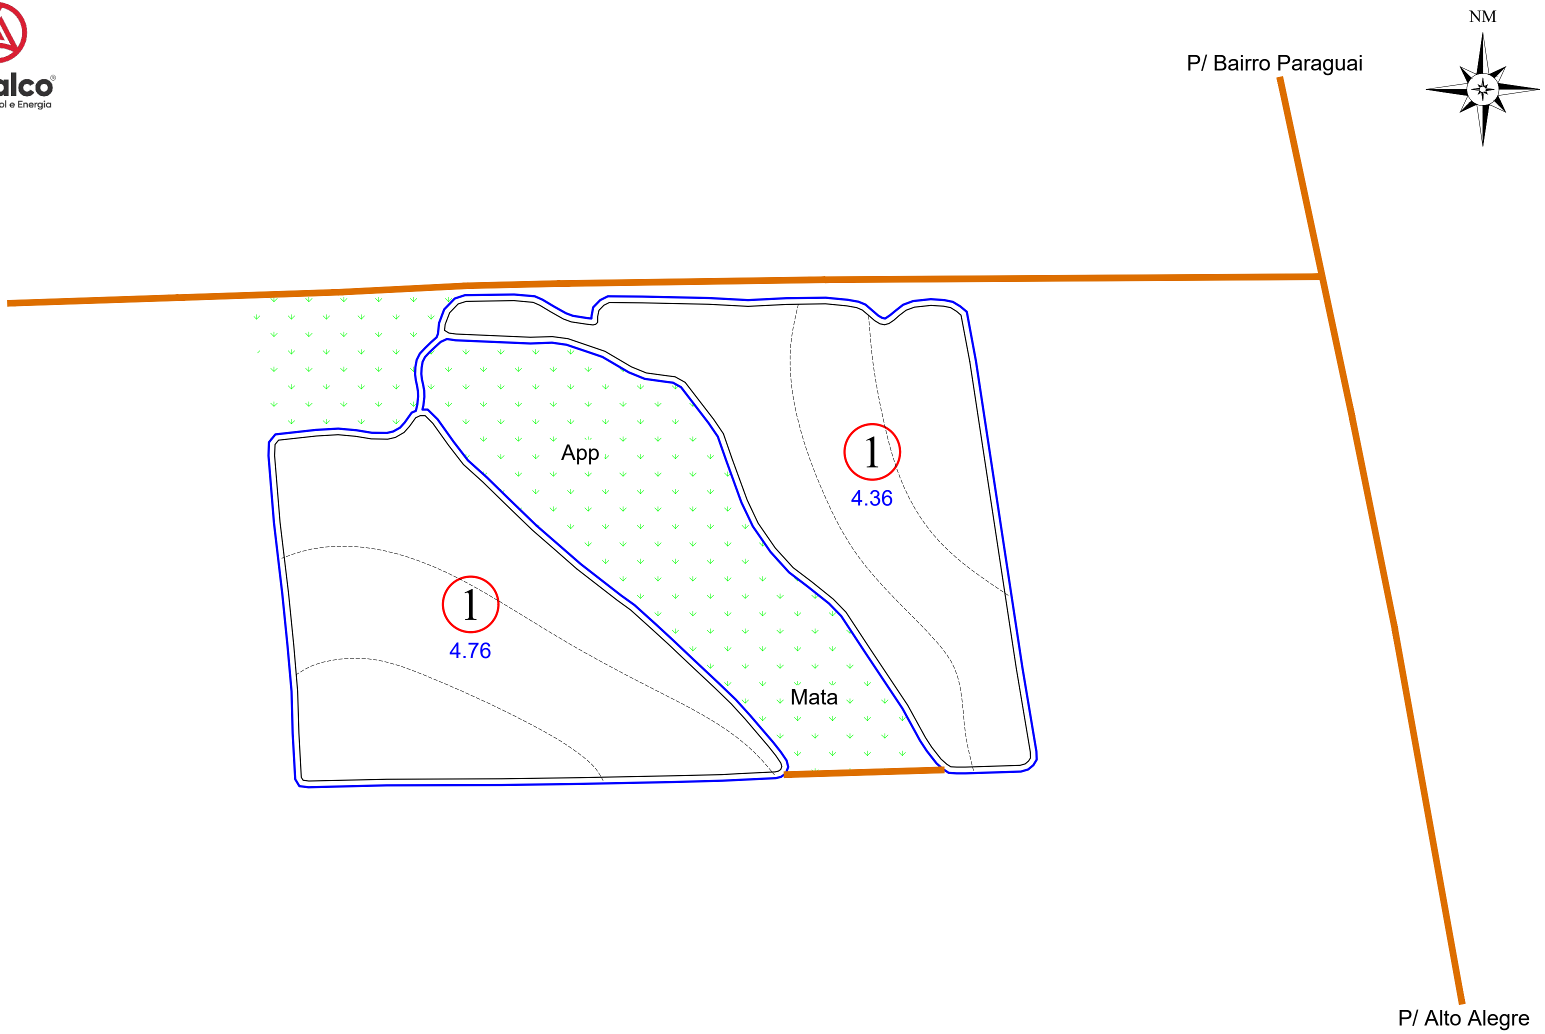

ESCALA: 1: 5.000

CROQUI DE ACESSO

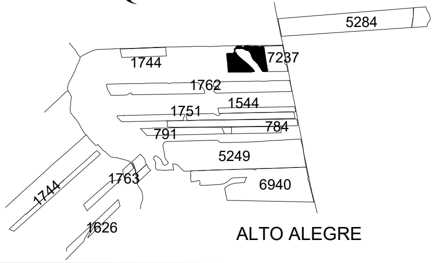

SÍTIO NOSSA SENHORA DE FÁTIMA

PROPRIETÁRIO: RAFAEL CAPUTO
COMPRADOR: CLEALCO S/A
MUNICÍPIO: ALTO ALEGRE

DISTÂNCIAS (km):

UNID. I -	Asfalto:	53.90	Terra.:	5.60
UNID.I I -	Asfalto:	42.10	Terra.:	5.60
UNID. III -	Asfalto:	0.00	Terra.:	11.50

COORDENADAS: E(X): 586068.10 N(Y): 7617205.08
LAT: -21°32'45.2337" LONG: -50°10'7.7408"

CLEALCO - AÇÚCAR E ALCOOL S/A - DEPARTAMENTO DE TOPOGRAFIA

UNIDADE:
I

PARTE:
A/A

FUNDO AGRÍCOLA:
307585

M:\01-Mapa de safra\Mapas Atualizados\Terceiro\307585 - Sítio Nossa Senhora de Fátima (Rafael Caputo)\307585 - Sítio Nossa Senhora de Fátima (Rafael Caputo).dwg

Fernanda Bezerra 15/02/24