ZONA D.V.	Nº TAL.	DATA PL.	ÁREA (ha)	VARIEDADE
999 5.60 %	1	04/2021	9.89	RB 975201
TOTAL PLANTIO			9.89	--------

ÁREAS	(ha)	(%)
PLANTIO	9.89	91.19
CARREADORES	0.96	8.81
OUTROS	0.00	0.00
SUB TOTAL AGRICULTÁVEL	10.85	100.00
AP.P.	0.00	0.00
ÁRVORES	0.00	0.00
OUTROS	0.00	0.00
SUB TOTAL NÃO AGRICULT.	0.00	0.00
ÁREA TOTAL	10.85	100.00

C. NÍVEL: 1256.27 m/l 0.29 ha 2.66 %

LEGENDA

▬ FAZENDA	▬ CONFRONTANTE
▬ TALHÃO	— REDE ELÉTRICA
▬ CURVA DE NÍVEL	—▷ TRAJETO VAZIO
— CARREADOR	—► TRAJETO CARREGADO

PLANTIO MANUAL - ESPAÇAMENTO: 1.50 X 1.50
TIRO MÉDIO ESTIMADO: 121.54 m

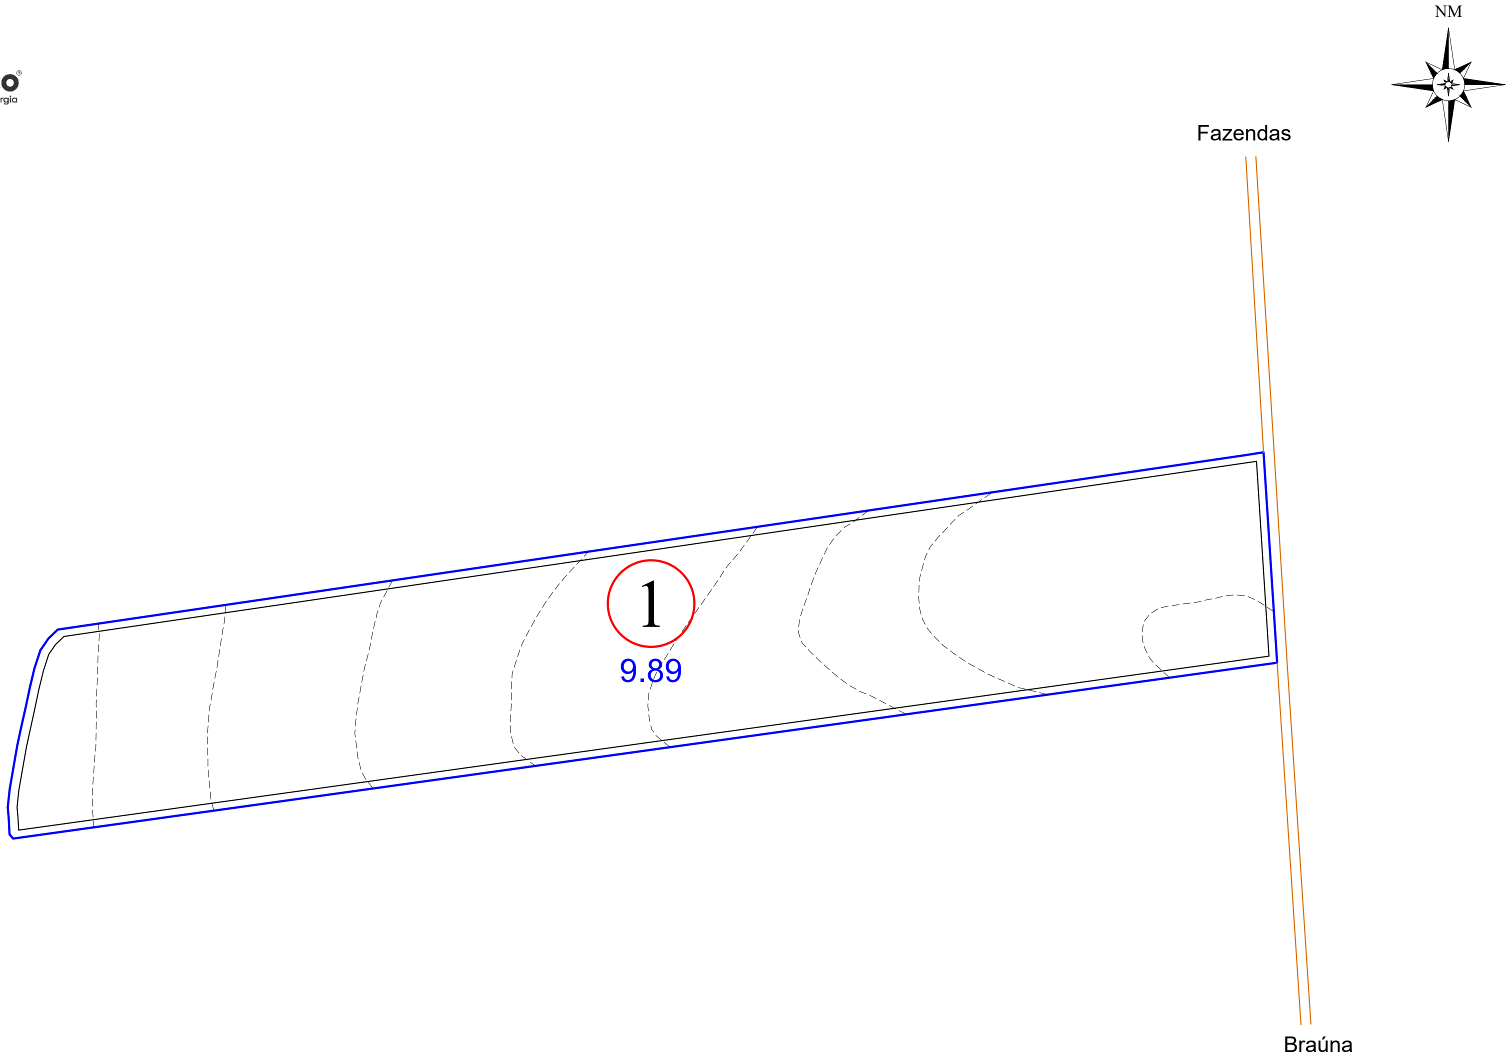

ESCALA: 1: 5.000

CROQUI DE ACESSO

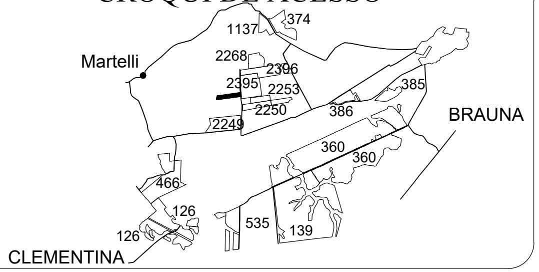

SÍTIO SANTO ANTÔNIO

PROPRIETÁRIO: VIVALDO GASTALDI
COMPRADOR: CLEALCO S/A
MUNICÍPIO: BRAÚNA - SP

DISTÂNCIAS (km):

	Asfalto:	Terra.:
UNID. I -	6.00	7.50
UNID.I I -	66.00	7.00
UNID. III -	38.00	7.00

COORDENADAS: E(X): 563346.92 N(Y): 7620484.47
LAT: -21°31'1.9911" LONG: -50°23'18.0757"

CLEALCO - AÇÚCAR E ALCOOL S/A - DEPARTAMENTO DE TOPOGRAFIA

UNIDADE:
I

PARTE:
A/A

FUNDO AGRÍCOLA:
307594

M:\01-Mapa de safra\Mapas Atualizados\Terceiro\307594 - Sítio Santo Antônio (Vivaldo Gastaldi)\307594 - Sítio Santo Antônio (Vivaldo Gastaldi).dwg