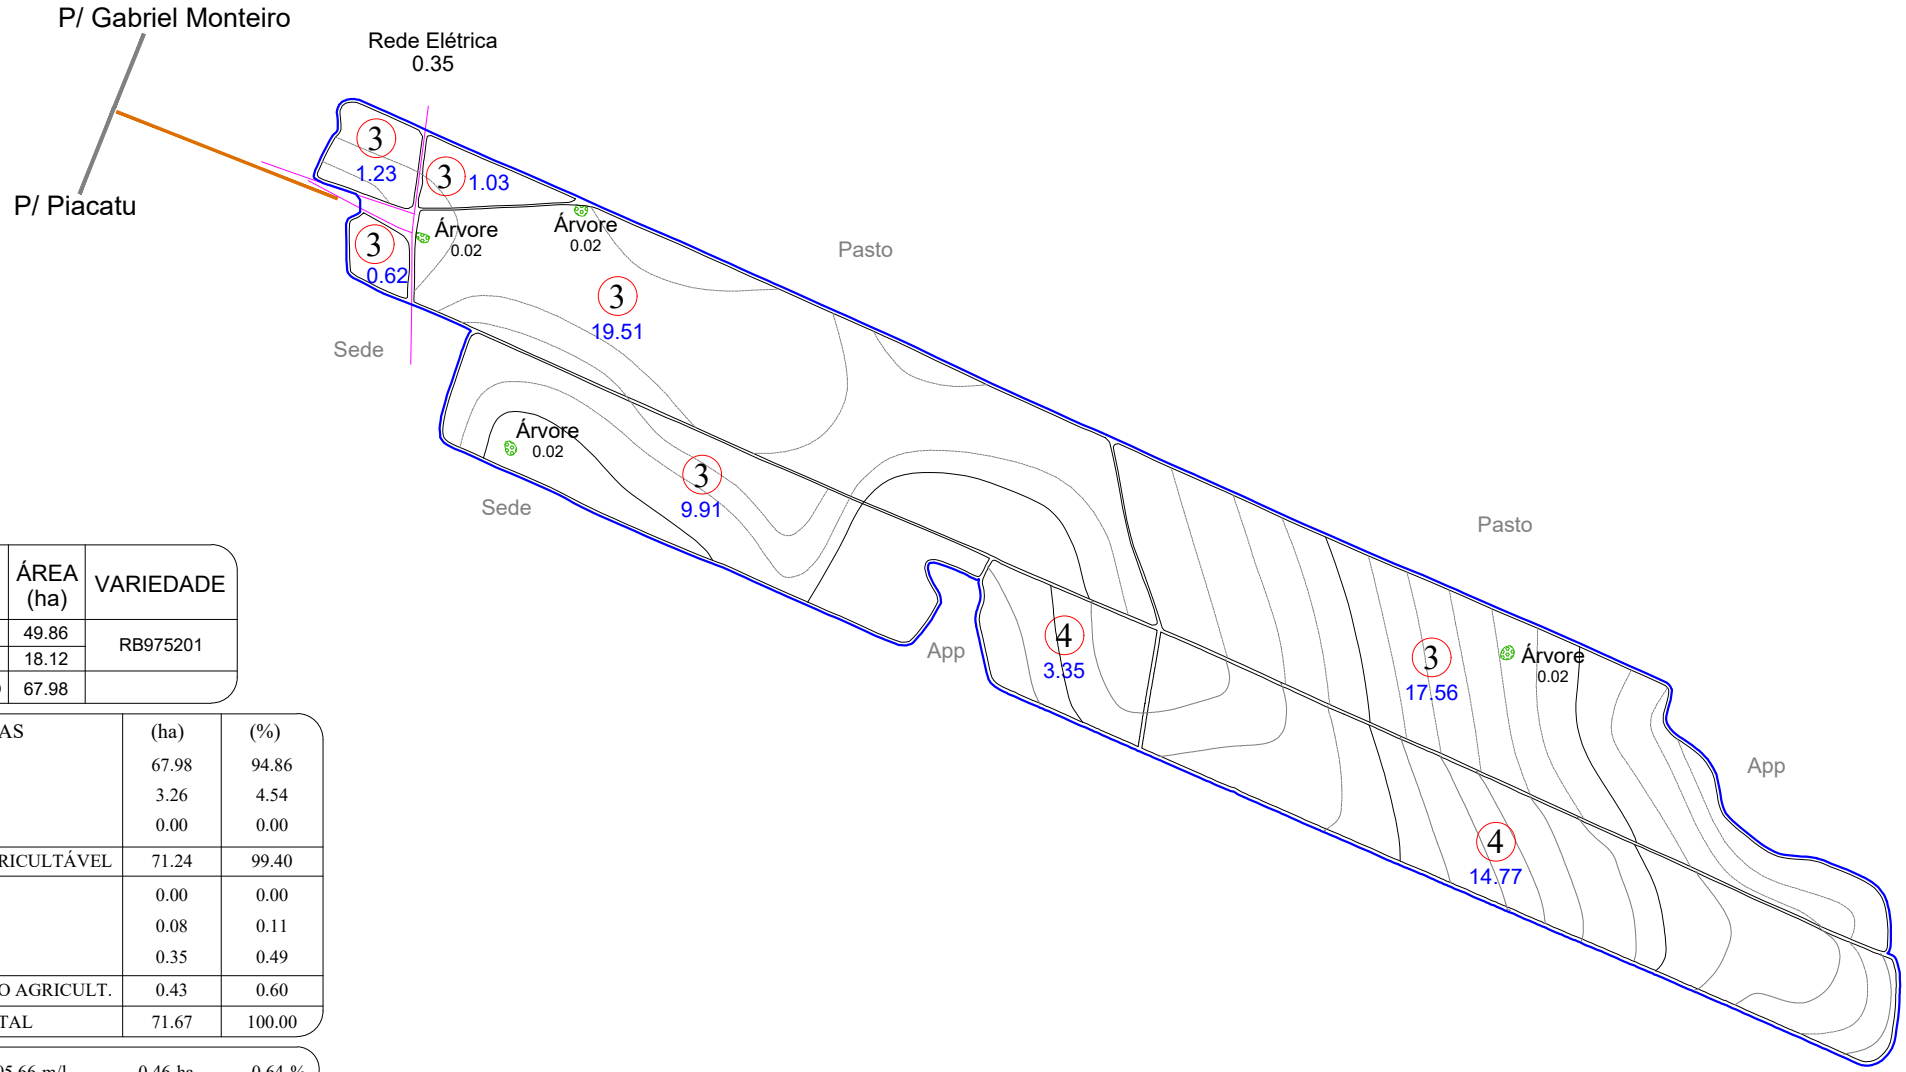


Nº TAL.	DATA PL.	ÁREA (ha)	VARIEDADE
3	05/2025	49.86	RB975201
4	05/2026	18.12	
TOTAL PLANTIO		67.98	

ÁREAS	(ha)	(%)
PLANTIO	67.98	94.86
CARREADORES	3.26	4.54
OUTROS	0.00	0.00
SUB TOTAL AGRICULTÁVEL	71.24	99.40
AP.P.	0.00	0.00
ÁRVORES	0.08	0.11
OUTROS	0.35	0.49
SUB TOTAL NÃO AGRICULT.	0.43	0.60
ÁREA TOTAL	71.67	100.00

C. NÍVEL: 2005.66 m/l 0.46 ha 0.64 %


ESCALA: 1: 10.000

LEGENDA

- FAZENDA
- TALHÃO
- REDE ELÉTRICA
- TERRAÇO BASE LARGA
- TERRAÇO EMBUTIDO

ESPAÇAMENTO: 1.50 x 1.50
TIRO MÉDIO ESTIMADO: 279.82
D.V: 4.47 %

CROQUI DE ACESSO

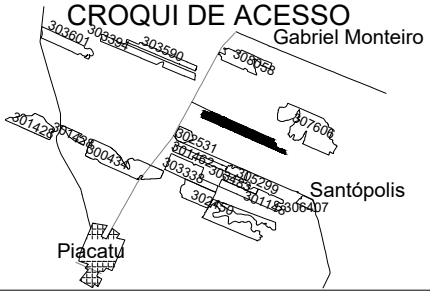

SÍTIO NOVO PROGRESSO

PROPRIETÁRIO: ROBERLEI BUENO
COMPRADOR: CLEALCO
MUNICÍPIO: PIACATU - SP

DISTÂNCIAS (km):
UNID. I - Asfalto: 6.00 Terra.: 5.50
UNID.I I - Asfalto: 53.00 Terra.: 6.00

COORDENADAS: E(X): 546038.78 N(Y): 7615851.94
LAT: -21°33'34.5685" LONG: -50°33'19.2277"

CLEALCO - AÇÚCAR E ALCOOL S/A - DEPARTAMENTO DE GEOTECNOLOGIA

LEVANTAMENTO VIA:
SATÉLITE
GPS / VANT
GOOGLE

UNIDADE: I
PARTE: B/B
FUNDO AGRÍCOLA: 307605

M:\01-Mapa de safra\Mapas Atualizados\Terceiro\307605 - Sítio Novo Progresso (Roberlei Bueno de Oliveira)\307605 B - Sítio Novo Progresso (Roberlei Bueno de Oliveira).dwg

Benati 05/05/26