
Clealco
Açúcar, Etanol e Energia

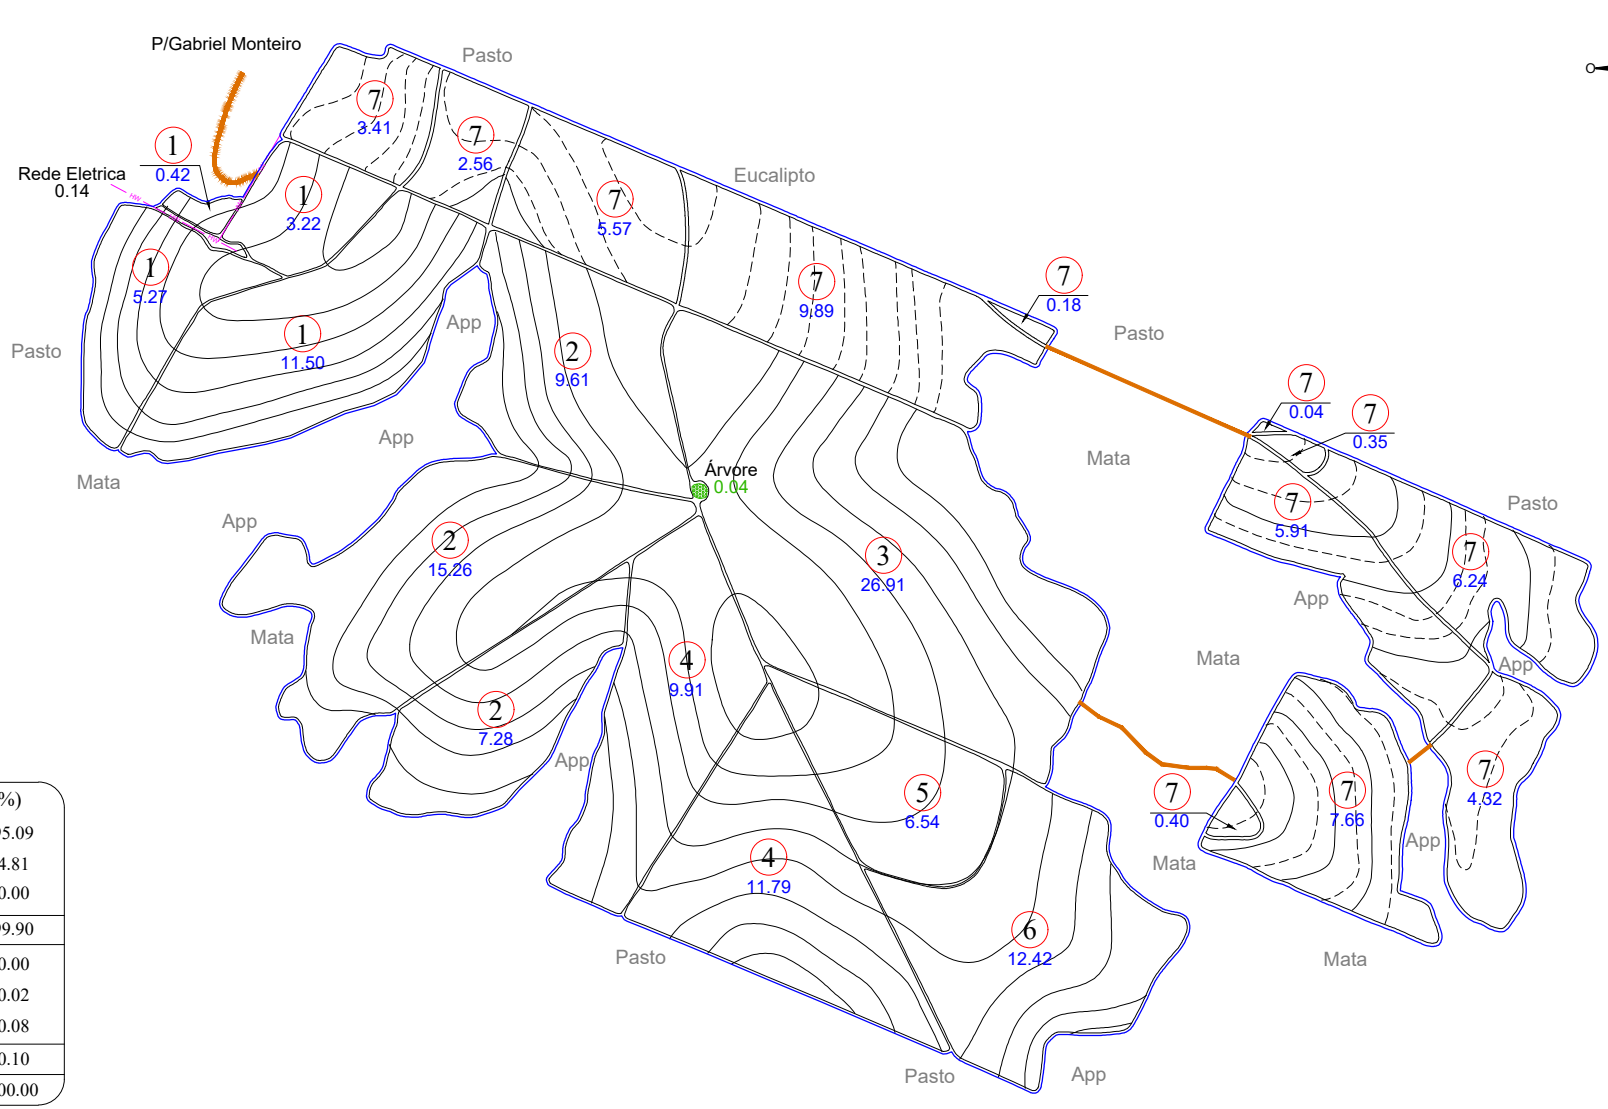

N
O E
S

Nº TAL.	DATA PL.	ÁREA (ha)	VARIEDADE
1	05/2024	20.41	RB97 5201
2		32.15	
3		26.91	
4		21.70	
5		6.54	
6		12.42	
7	2026	46.53	PRÉ PLANTIO
TOTAL PLANTIO		166.66	

ÁREAS	(ha)	(%)
PLANTIO	166.66	95.09
CARREADORES	8.42	4.81
OUTROS	0.00	0.00
SUB TOTAL AGRICULTÁVEL	175.08	99.90
AP.P.	0.00	0.00
ÁRVORES	0.04	0.02
OUTROS	0.14	0.08
SUB TOTAL NÃO AGRICULT.	0.18	0.10
ÁREA TOTAL	175.26	100.00

C. NÍVEL:	23370.18 m/l	5.38 ha	3.07 %


ESCALA: 1: 12.000

LEGENDA

- FAZENDA
- TALHÃO
- REDE ELÉTRICA
- TERRAÇO BASE LARGA
- TERRAÇO EMBUTIDO
- VAZIO
- CARREGADO

ESPAÇAMENTO: 1.50 x 1.50
TIRO MÉDIO ESTIMADO: 000.00 m
D.V: 4.78 %

CROQUI DE ACESSO

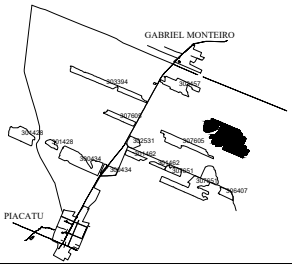

FAZENDA JANGADA

PROPRIETÁRIO: ROBERLEI BUENO DE OLIVEIRA
COMPRADOR: CLEALCO
MUNICÍPIO: GABRIEL MONTEIRO - SP

DISTÂNCIAS (km):
UNID. I - Asfalto: 6.00 Terra.: 5.50
UNID.I I - Asfalto: 53.00 Terra.: 5.50

COORDENADAS: E(X): 547840.68 N(Y): 7616093.76
LAT: -21°33'26.5328" LONG: -50°32'16.6019"

CLEALCO - AÇÚCAR E ALCOOL S/A - DEPARTAMENTO DE GEOTECNOLOGIA

LEVANTAMENTO VIA:
SATÉLITE
GPS / VANT
GOOGLE

UNIDADE: I
PARTE: A/A
FUNDO AGRÍCOLA: 307606