
Clealco
Açúcar, Etanol e Energia

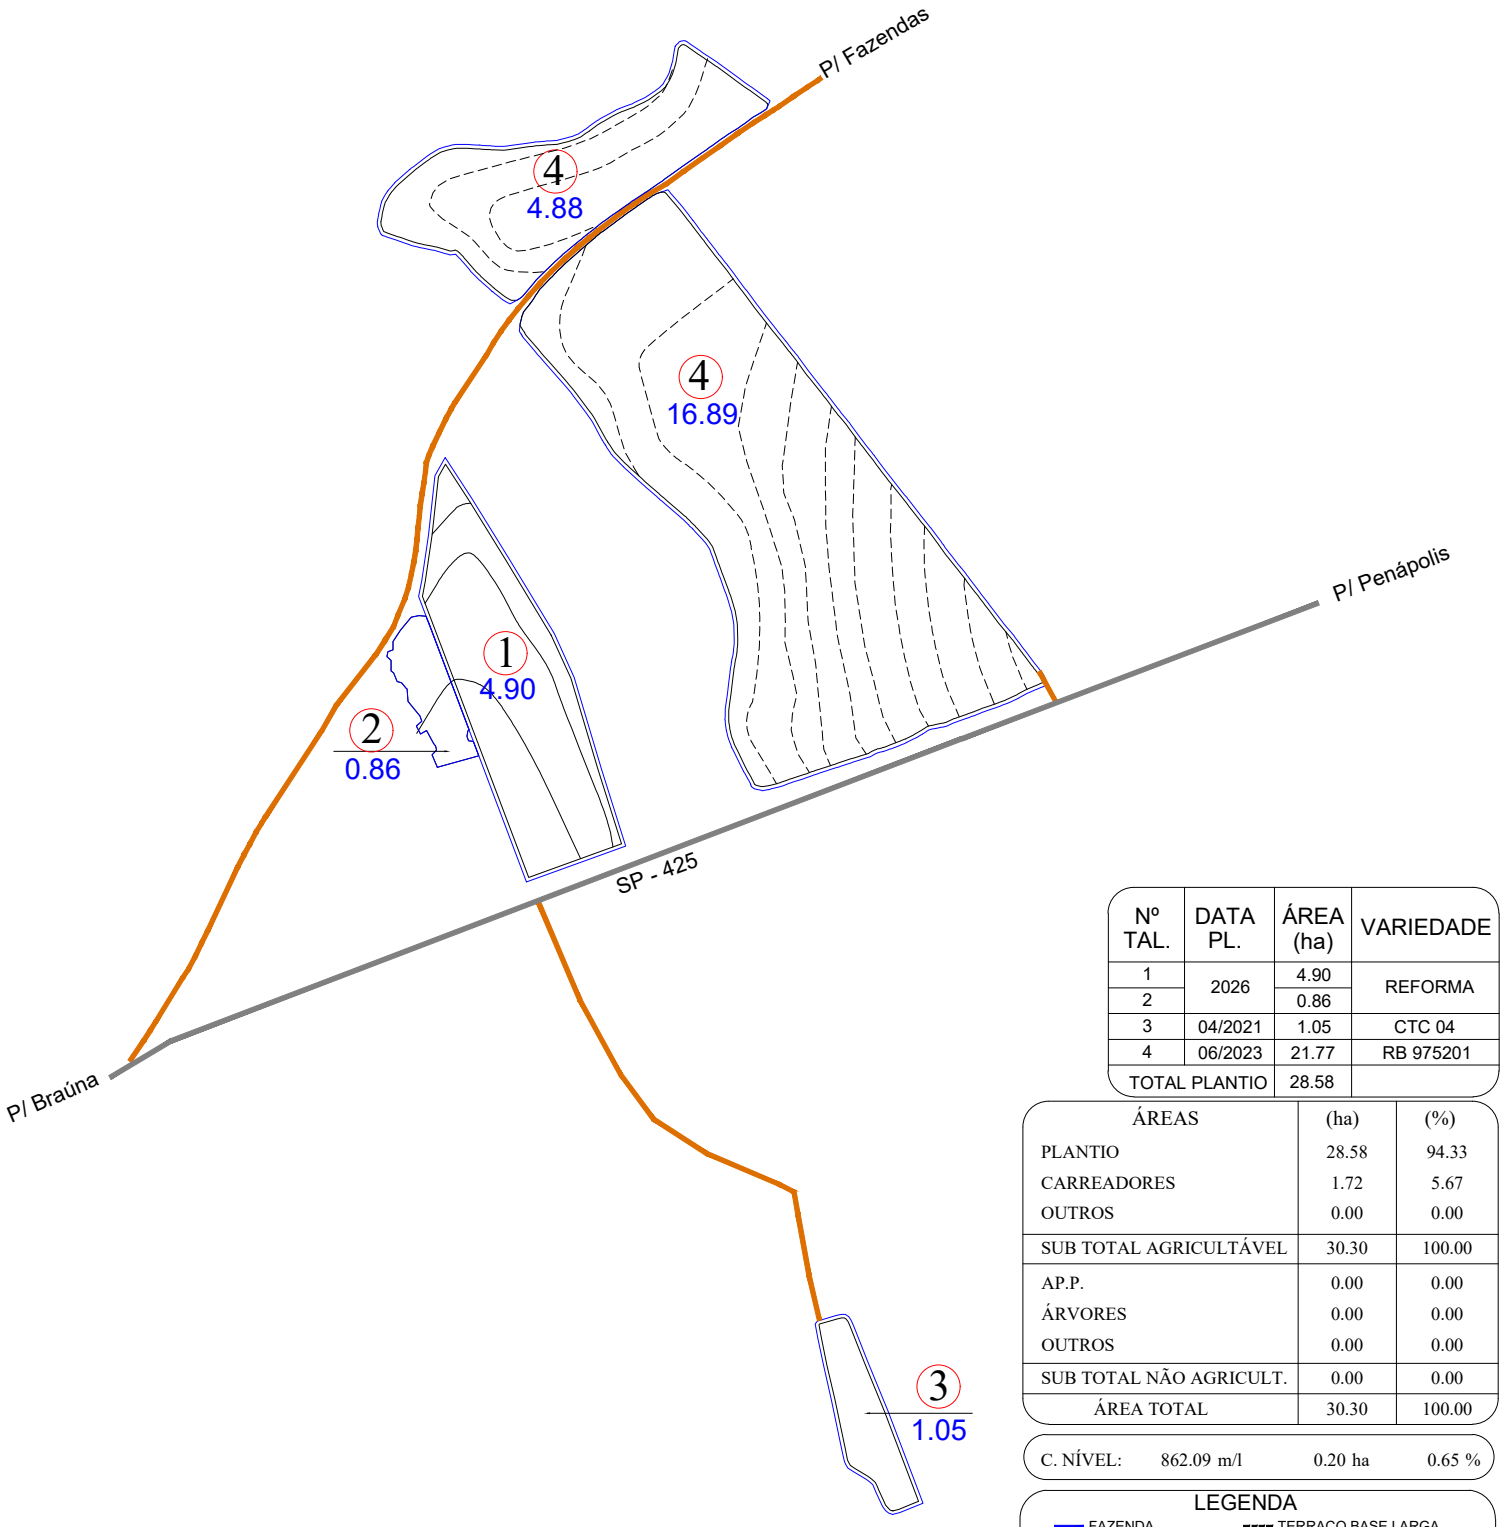

Nº TAL.	DATA PL.	ÁREA (ha)	VARIEDADE
1	2026	4.90	REFORMA
2		0.86	
3	04/2021	1.05	CTC 04
4	06/2023	21.77	RB 975201
TOTAL PLANTIO		28.58	

ÁREAS	(ha)	(%)
PLANTIO	28.58	94.33
CARREADORES	1.72	5.67
OUTROS	0.00	0.00
SUB TOTAL AGRICULTÁVEL	30.30	100.00
AP.P.	0.00	0.00
ÁRVORES	0.00	0.00
OUTROS	0.00	0.00
SUB TOTAL NÃO AGRICULT.	0.00	0.00
ÁREA TOTAL	30.30	100.00

C. NÍVEL: 862.09 m/l 0.20 ha 0.65 %


LEGENDA

- FAZENDA
- TALHÃO
- REDE ELÉTRICA
- TERRAÇO BASE LARGA
- TERRAÇO EMBUTIDO
- (P.O.A) PATIO DE OPERAÇÃO

ESPAÇAMENTO: 1.50 x 1.50
TIRO MÉDIO ESTIMADO: 000.00 m
D.V: 6.44 %

ESCALA: 1: 10.000

CROQUI DE ACESSO

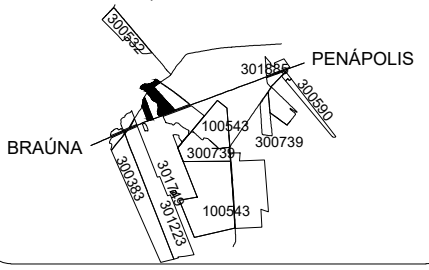

FAZENDA FLORESTA

PROPRIETÁRIO: VALCIR PERES BATISTA
COMPRADOR: CLEALCO
MUNICÍPIO: PENÁPOLIS - SP

DISTÂNCIAS (km):
UNID. I - Asfalto: 23.50 Terra.: 0.00
UNID.I I - Asfalto: 30.90 Terra.: 19.00

COORDENADAS: E(X): 576964.28 N(Y): 7622486.24
LAT: -21°29'54.9654" LONG: -50°15'25.0979"

CLEALCO - AÇÚCAR E ALCOOL S/A - DEPARTAMENTO DE GEOTECNOLOGIA

LEVANTAMENTO VIA:
SATÉLITE
GPS / VANT
GOOGLE

UNIDADE: I
PARTE: A/A
FUNDO AGRÍCOLA: 307609

M:\01-Mapa de safra\Mapas Atualizados\Terceiro\307609 - Fazenda Floresta (Valcir Peres Batista)\307609 - Fazenda Floresta (Valcir Peres Batista).dwg

Benati 24/02/2026