
Clealco
Açúcar, Etanol e Energia

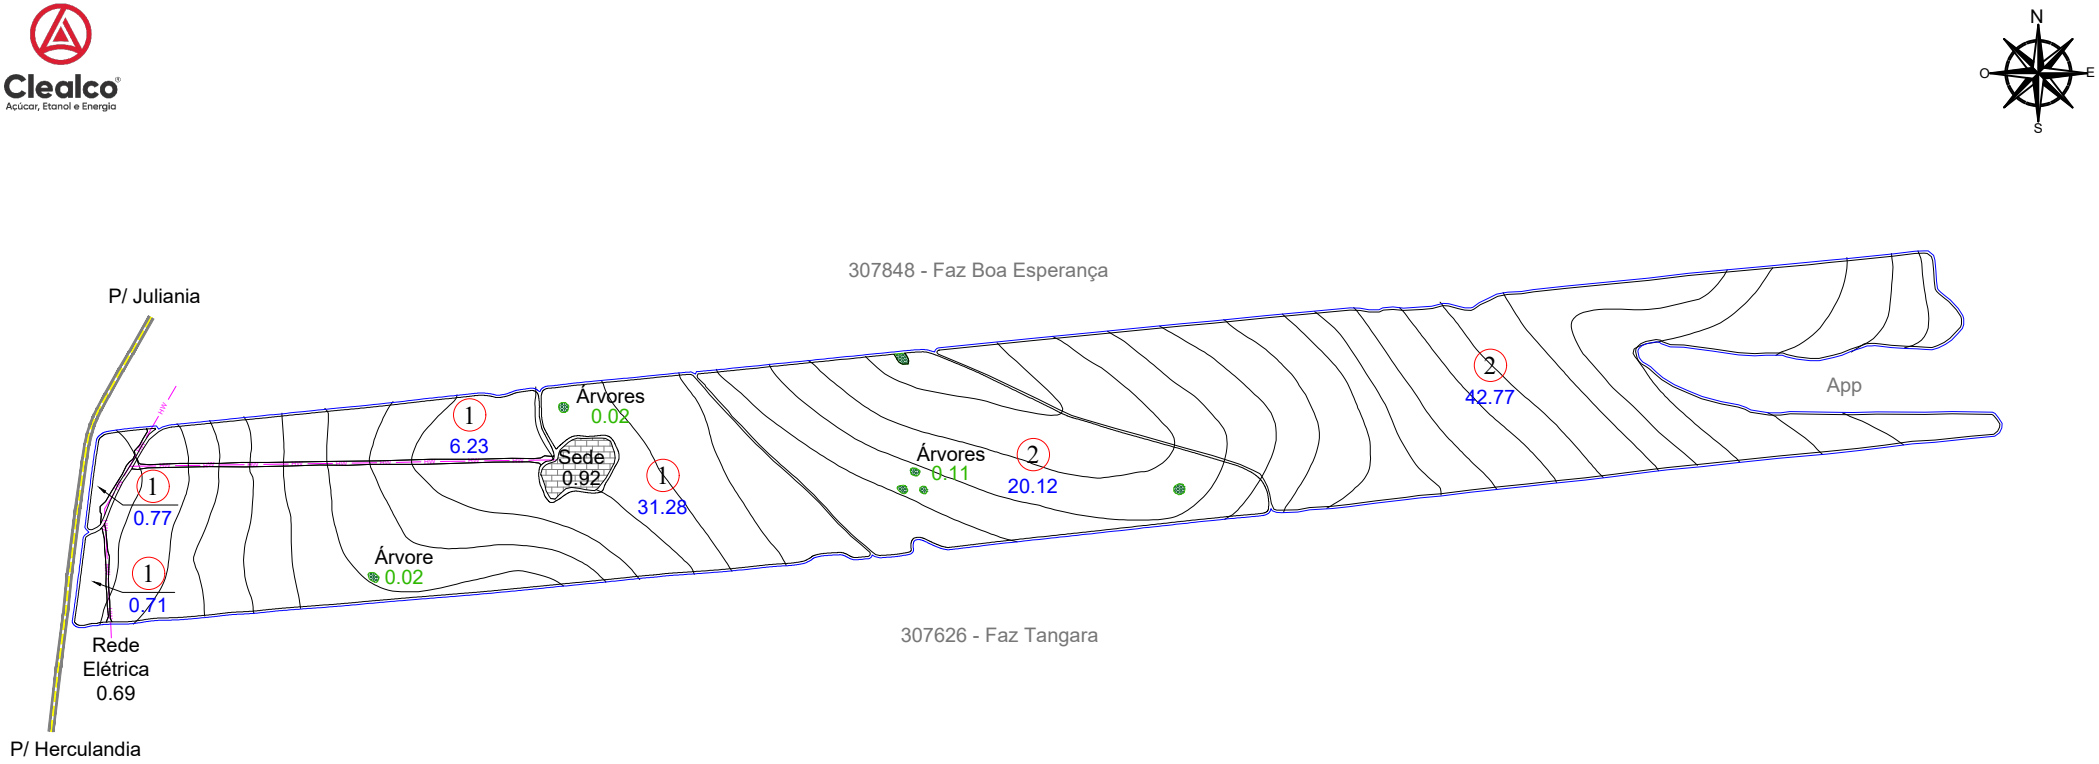

ÁREAS	(ha)	(%)
PLANTIO	101.88	94.51
CARREADORES	5.77	5.35
OUTROS	0.00	0.00
SUB TOTAL AGRICULTÁVEL	107.65	99.86
AP.P.	0.00	0.00
ÁRVORES	0.15	0.14
OUTROS	0.00	0.00
SUB TOTAL NÃO AGRICULT.	0.15	0.14
ÁREA TOTAL	107.80	100.00

C. NÍVEL: 13717.01 m/l 3.15 ha 2.93 %


Nº TAL.	DATA PL.	ÁREA (ha)	VARIEDADE
1	05/2024	38.99	RB867515
2		62.89	
TOTAL PLANTIO		101.88	

ESCALA: 1: 13.500

LEGENDA
- FAZENDA
- TALHÃO
- REDE ELÉTRICA
- TERRAÇO BASE LARGA
- TERRAÇO EMBUTIDO

ESPAÇAMENTO: 1.50 x 1.50
TIRO MÉDIO ESTIMADO: 201.11 m
D.V: 4.90 %

CROQUI DE ACESSO

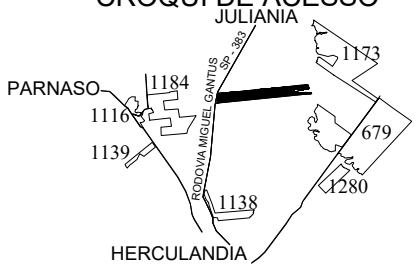

FAZENDA BEM TE VI

PROPRIETÁRIO: REGINALDO VIANA RODRIGUES
COMPRADOR: CLEALCO
MUNICÍPIO: HERCULÂNDIA - SP

DISTÂNCIAS (km):
UNID. I - Asfalto: 43.80 Terra.: 31.40
UNID.I I - Asfalto: 29.10 Terra.: 1.30

COORDENADAS: E(X): 564218.43 N(Y): 7572859.61
LAT: -21°56'50.8102" LONG: -50°22'41.1305"
CLEALCO - AÇÚCAR E ALCOOL S/A - DEPARTAMENTO DE GEOTECNOLOGIA

LEVANTAMENTO VIA:
- SATÉLITE
- GPS / VANT
- GOOGLE

UNIDADE: II
PARTE: A/A
FUNDO AGRÍCOLA: 307610

M:\01-Mapa de safra\Mapas Atualizados\Terceiro\307610 - Fazenda Bem te vi (Reginaldo Viana Rodrigues)\307610 - Fazenda Bem te vi (Reginaldo Viana Rodrigues).dwg

Peterson Santos 00/00/25