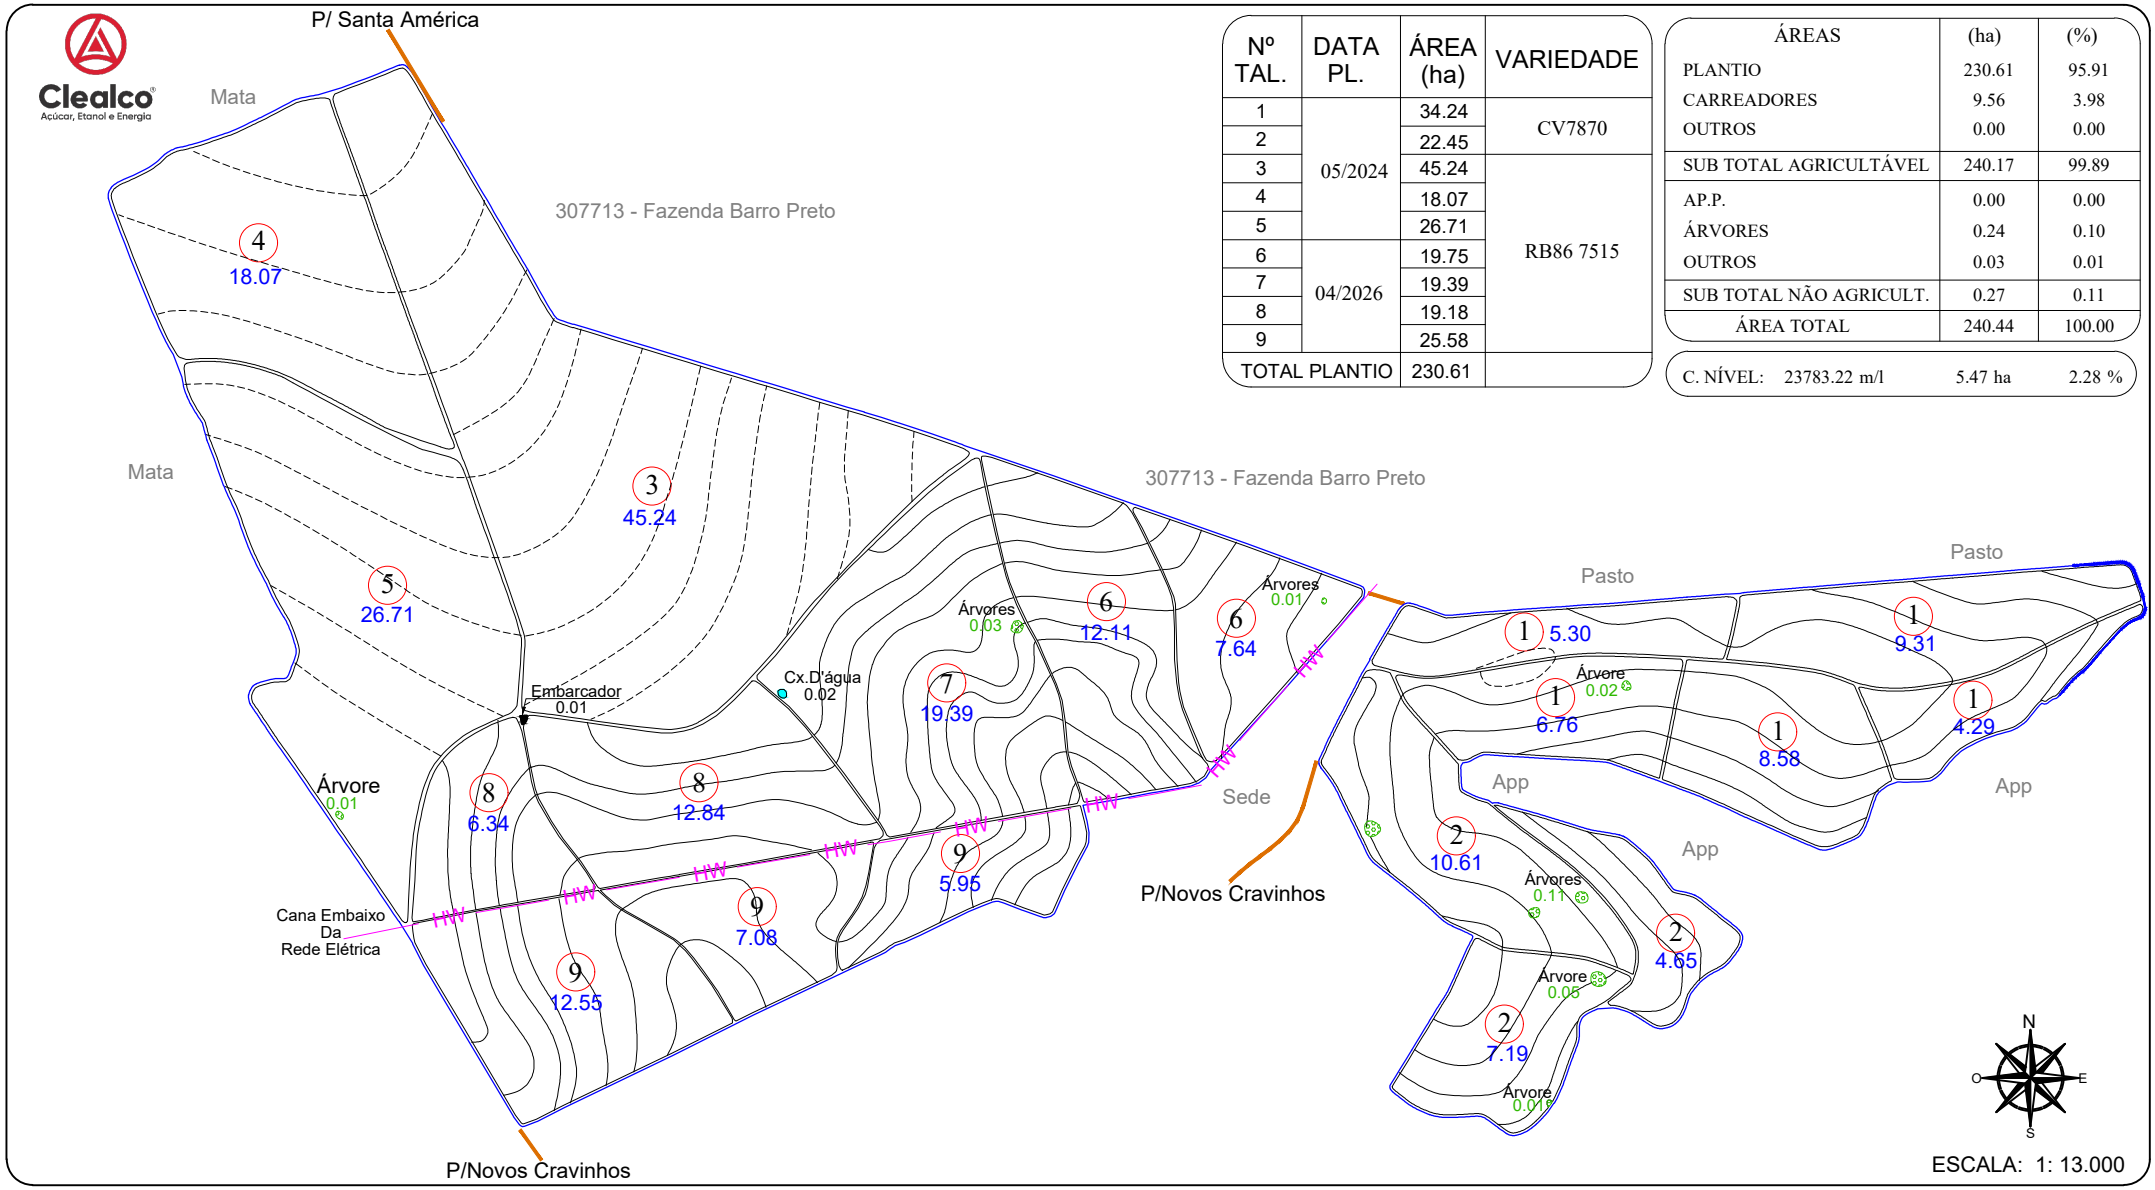


ESCALA: 1: 13.000

Nº TAL.	DATA PL.	ÁREA (ha)	VARIEDADE
1	05/2024	34.24	CV7870
2		22.45	
3		45.24	RB86 7515
4		18.07	
5		26.71	
6	04/2026	19.75	
7		19.39	
8		19.18	
9		25.58	
TOTAL PLANTIO		230.61	

ÁREAS	(ha)	(%)
PLANTIO	230.61	95.91
CARREADORES	9.56	3.98
OUTROS	0.00	0.00
SUB TOTAL AGRICULTÁVEL	240.17	99.89
AP.P.	0.00	0.00
ÁRVORES	0.24	0.10
OUTROS	0.03	0.01
SUB TOTAL NÃO AGRICULT.	0.27	0.11
ÁREA TOTAL	240.44	100.00

C. NÍVEL: 23783.22 m/l 5.47 ha 2.28 %

LEGENDA

- FAZENDA
- TALHÃO
- REDE ELÉTRICA
- TERRAÇO BASE LARGA
- TERRAÇO EMBUTIDO

ESPAÇAMENTO: 1.50 x 1.50
TIRO MÉDIO ESTIMADO: 292.83 m
D.V: 3.97 %

CROQUI DE ACESSO



FAZENDA PAU D'ALHO

PROPRIETÁRIO: ANA LUCIA ALVES GILBERTO
COMPRADOR: CLEALCO
MUNICÍPIO: POMPÉIA - SP

DISTÂNCIAS (km):
UNIDADE I - 91.50
UNIDADE I I - 26.65

COORDENADAS: E(X): 593092.24 N(Y): 7575928.72
LAT: -21°55'6.3346" LONG: -50°5'55.2018"

CLEALCO - AÇÚCAR E ALCOOL S/A - DEPARTAMENTO DE GEOTECNOLOGIA

LEVANTAMENTO VIA:
SATÉLITE
GPS / VANT
GOOGLE

UNIDADE: II
PARTE: A/A
FUNDO AGRÍCOLA: 307615

M:\01-Mapa de safra\Mapas Atualizados\Terceiro\307615 - Fazenda Pau D'Alho (Ana Lucia Alves Gilberto)\307615 - Fazenda Pau D'Alho (Ana Lucia Alves Gilberto).dwg

Bruno Gamboa 22/09/26