D.V.	Nº TAL.	DATA PL.	ÁREA (ha)	VARIEDADE
3.48 %	1	06/2024	49.84	XXXX
TOTAL PLANTIO			49.84	--------

ÁREAS	(ha)	(%)
PLANTIO	49.84	94.93
CARREADORES	2.35	4.48
OUTROS	0.00	0.00
SUB TOTAL AGRICULTÁVEL	52.19	99.41
AP.P.	0.00	0.00
ÁRVORES	0.04	0.08
OUTROS	0.27	0.51
SUB TOTAL NÃO AGRICULT.	0.31	0.59
ÁREA TOTAL	52.50	100.00

C. NÍVEL: 5380.48 m/l 1.24 ha 2.36 %

LEGENDA

FAZENDA	CONFRONTANTE
TALHÃO	REDE ELÉTRICA
CURVA DE NÍVEL	TRAJETO VAZIO
CARREADOR	TRAJETO CARREGADO

PLANTIO MANUAL - ESPAÇAMENTO: 1.50 X 1.50
TIRO MÉDIO ESTIMADO: 363.65 m

Clealco®
Açúcar, Etanol e Energia

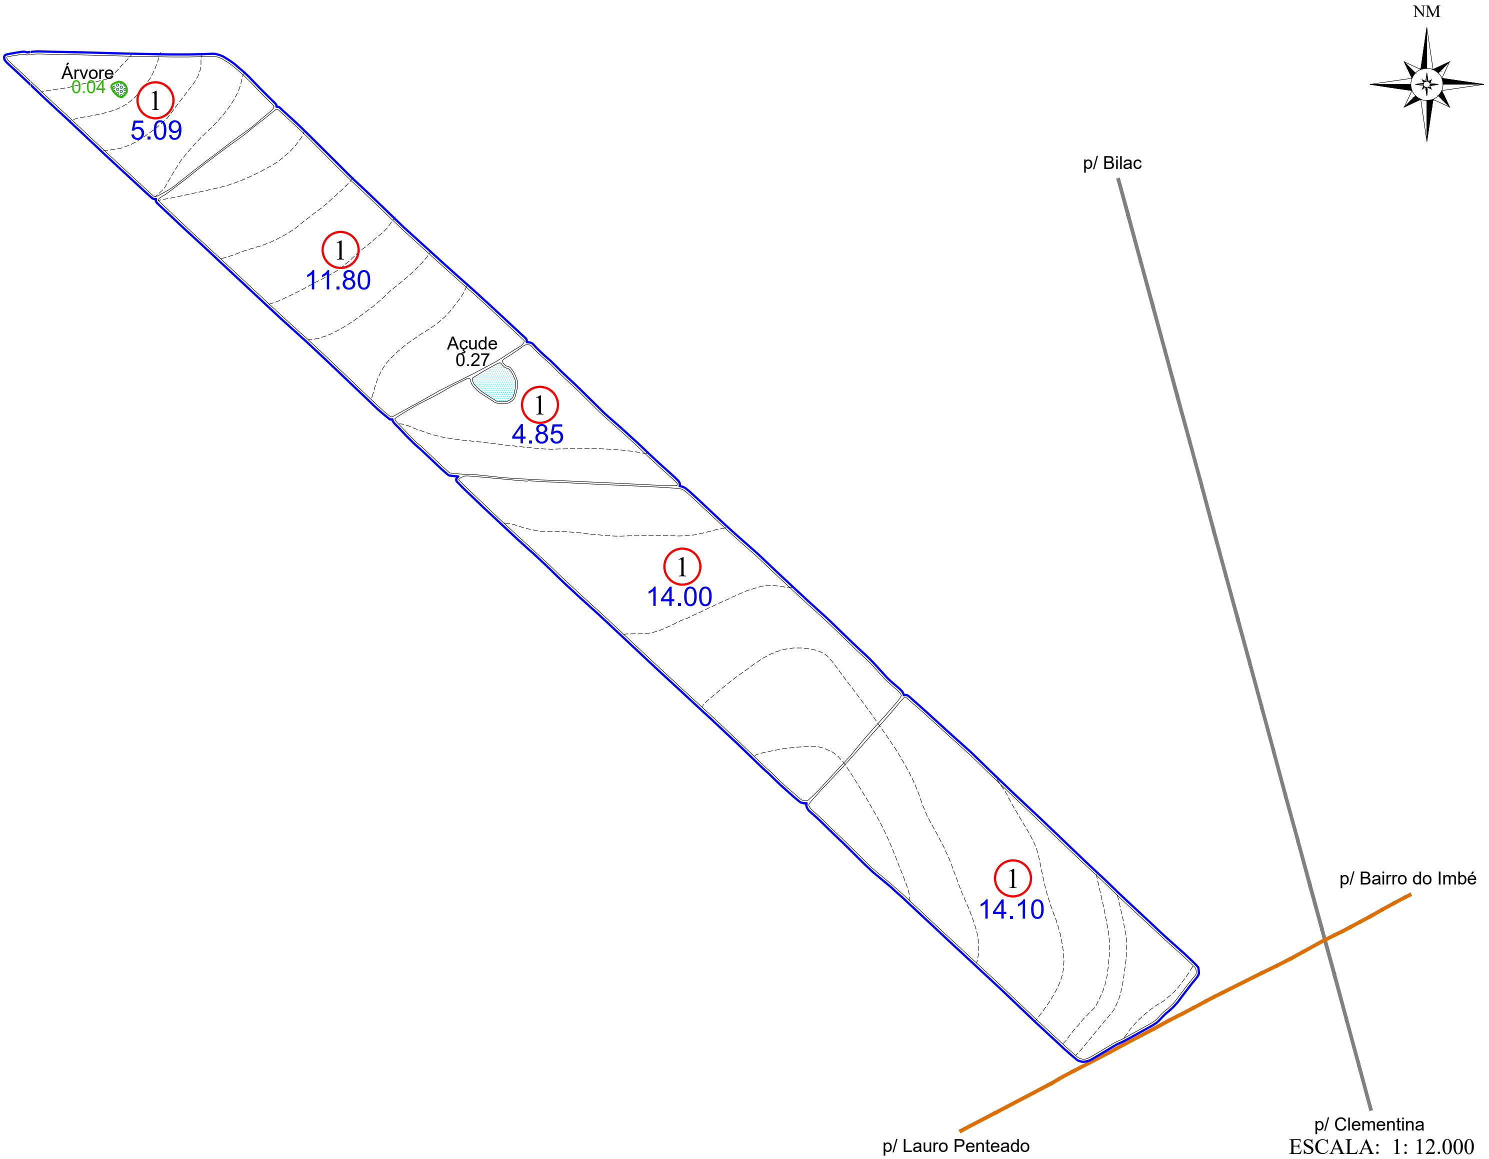
NM
Árvore
0.04
1
5.09
1
11.80
Açude
0.27
1
4.85
1
14.00
1
14.10
p/ Bilac
p/ Bairro do Imbé
p/ Clementina
p/ Lauro Penteado

ESCALA: 1: 12.000

CROQUI DE ACESSO

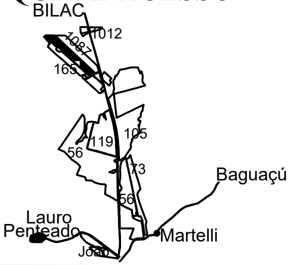
BILAC
1012
1087
165
105
119
56
73
56
Baguaçú
Lauro Penteado
Martelli
João

SÍTIO NOSSA SENHORA APARECIDA

PROPRIETÁRIO: ANTONIO ROBERTO GENARI
COMPRADOR: CLEALCO S/A
MUNICÍPIO: BILAC

DISTÂNCIAS (km):

UNID. I -	Asfalto:	14.20	Terra.:	1.00
UNID.I I -	Asfalto:	72.20	Terra.:	1.00
UNID. III -	Asfalto:	52.00	Terra.:	1.00

COORDENADAS: E(X):	557345.87	N(Y):	7627951.41
LAT:	-21°26'59.8572"	LONG:	-50°26'47.5815"

CLEALCO - AÇÚCAR E ALCOOL S/A - DEPARTAMENTO DE TOPOGRAFIA

UNIDADE:
I

PARTE:
A/A

FUNDO AGRÍCOLA:
307694