ZONA D.V.	Nº TAL.	DATA PL.	ÁREA (ha)	VARIEDADE
999 4.95 %	1	05/2024	12.97	xxxxxxx
TOTAL PLANTIO			12.97	--------

ÁREAS	(ha)	(%)
PLANTIO	12.97	91.43
CARREADORES	1.06	7.45
OUTROS	0.00	0.00
SUB TOTAL AGRICULTÁVEL	14.03	98.87
AP.P.	0.00	0.00
ÁRVORES	0.16	1.13
OUTROS	0.00	0.00
SUB TOTAL NÃO AGRICULT.	0.16	1.13
ÁREA TOTAL	14.19	100.00

C. NÍVEL: 1598.14 m/l 0.37 ha 2.59 %

LEGENDA

▬ FAZENDA	▬ CONFRONTANTE
▬ TALHÃO	-·- REDE ELÉTRICA
▪▪▪ CURVA DE NÍVEL	—▷ TRAJETO VAZIO
— CARREADOR	—► TRAJETO CARREGADO

PLANTIO MANUAL - ESPAÇAMENTO: 1.50 X 1.50
TIRO MÉDIO ESTIMADO: 159.94 m

Clealco
Açúcar, Etanol e Energia

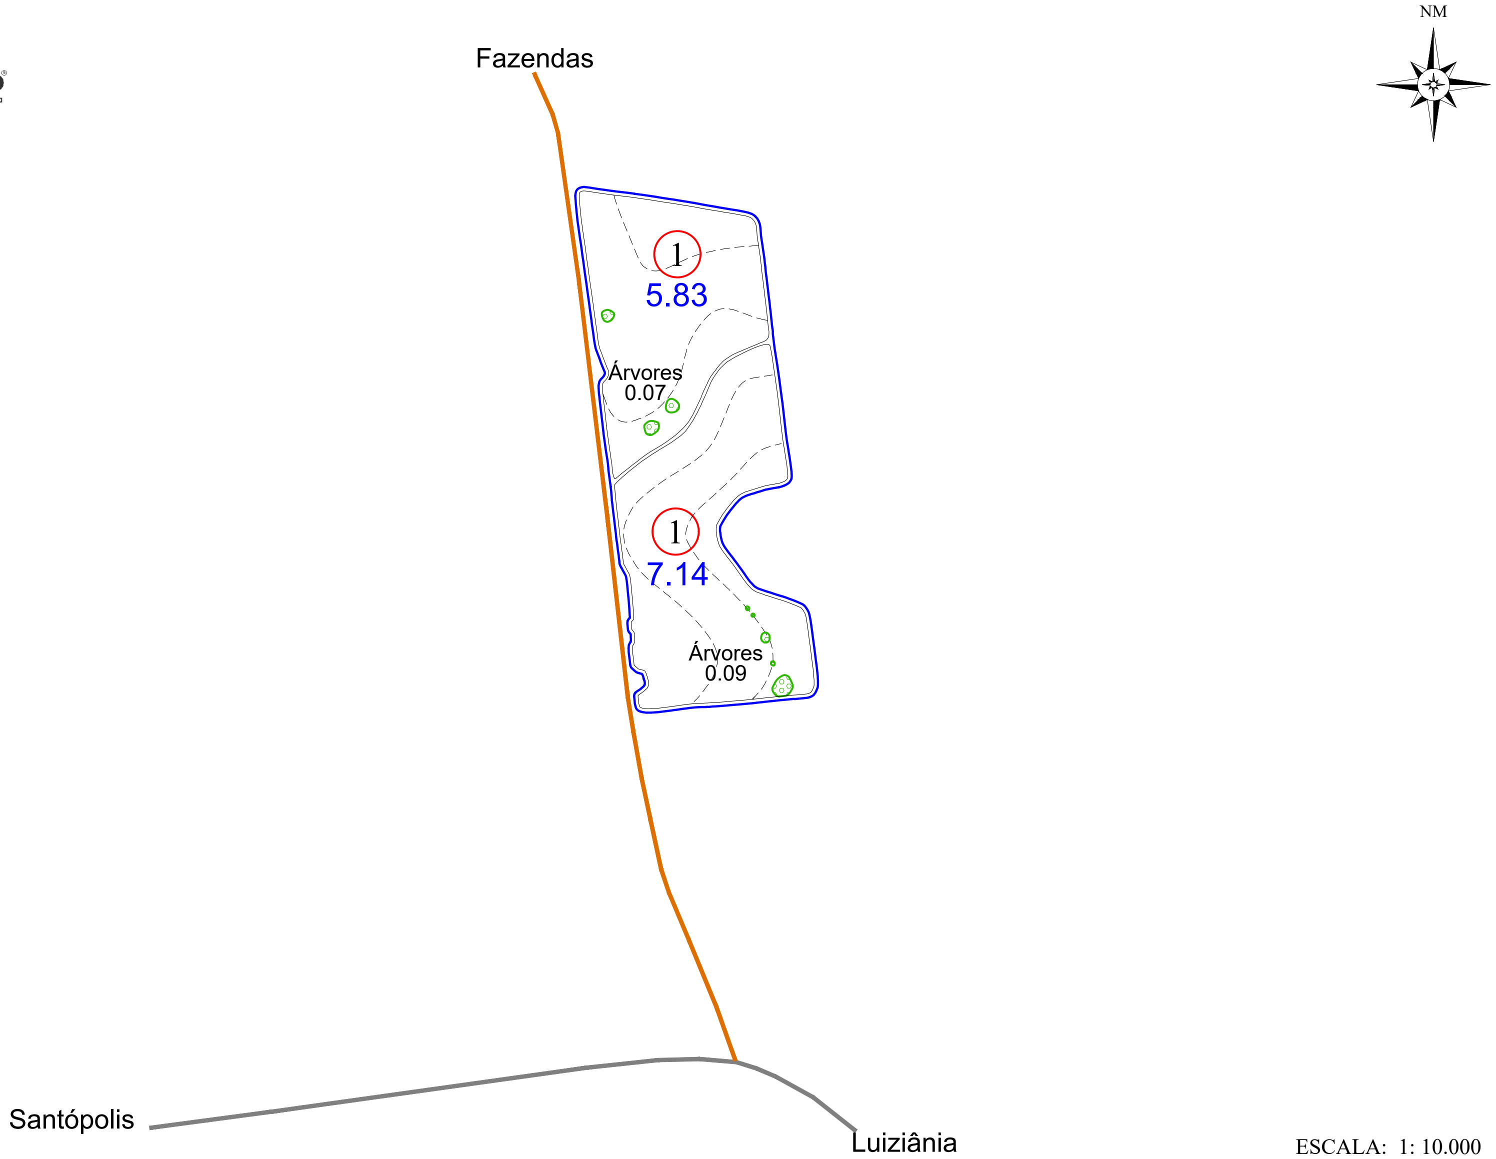

ESCALA: 1: 10.000

CROQUI DE ACESSO

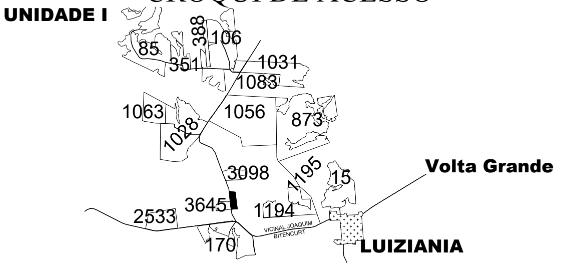

SÍTIO VOPORANGA

PROPRIETÁRIO:	JOSE SOARES
COMPRADOR:	CLEALCO S/A
MUNICÍPIO:	LUIZIÂNIA

DISTÂNCIAS (km):

UNID. I -	Asfalto:	27.50	Terra.:	0.50
UNID.I I -	Asfalto:	32.10	Terra.:	0.50
UNID. III -	Asfalto:	40.50	Terra.:	0.50

COORDENADAS: E(X): 565164.90 N(Y): 7603771.46
LAT: -21°40'5.3314" LONG: -50°22'12.5358"

CLEALCO - AÇÚCAR E ALCOOL S/A - DEPARTAMENTO DE TOPOGRAFIA

UNIDADE:
I

PARTE:
A/A

FUNDO AGRÍCOLA:
307695

M:\01-Mapa de safra\Mapas Atualizados\Terceiro\307695 - Sítio Voporanga (José Soares)\307695 - Sítio Voporanga (José Soares).dwg

Bruno Gamboa 11/11/24