

Clealco
Açúcar, Etanol e Energia

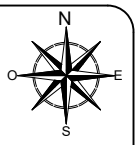

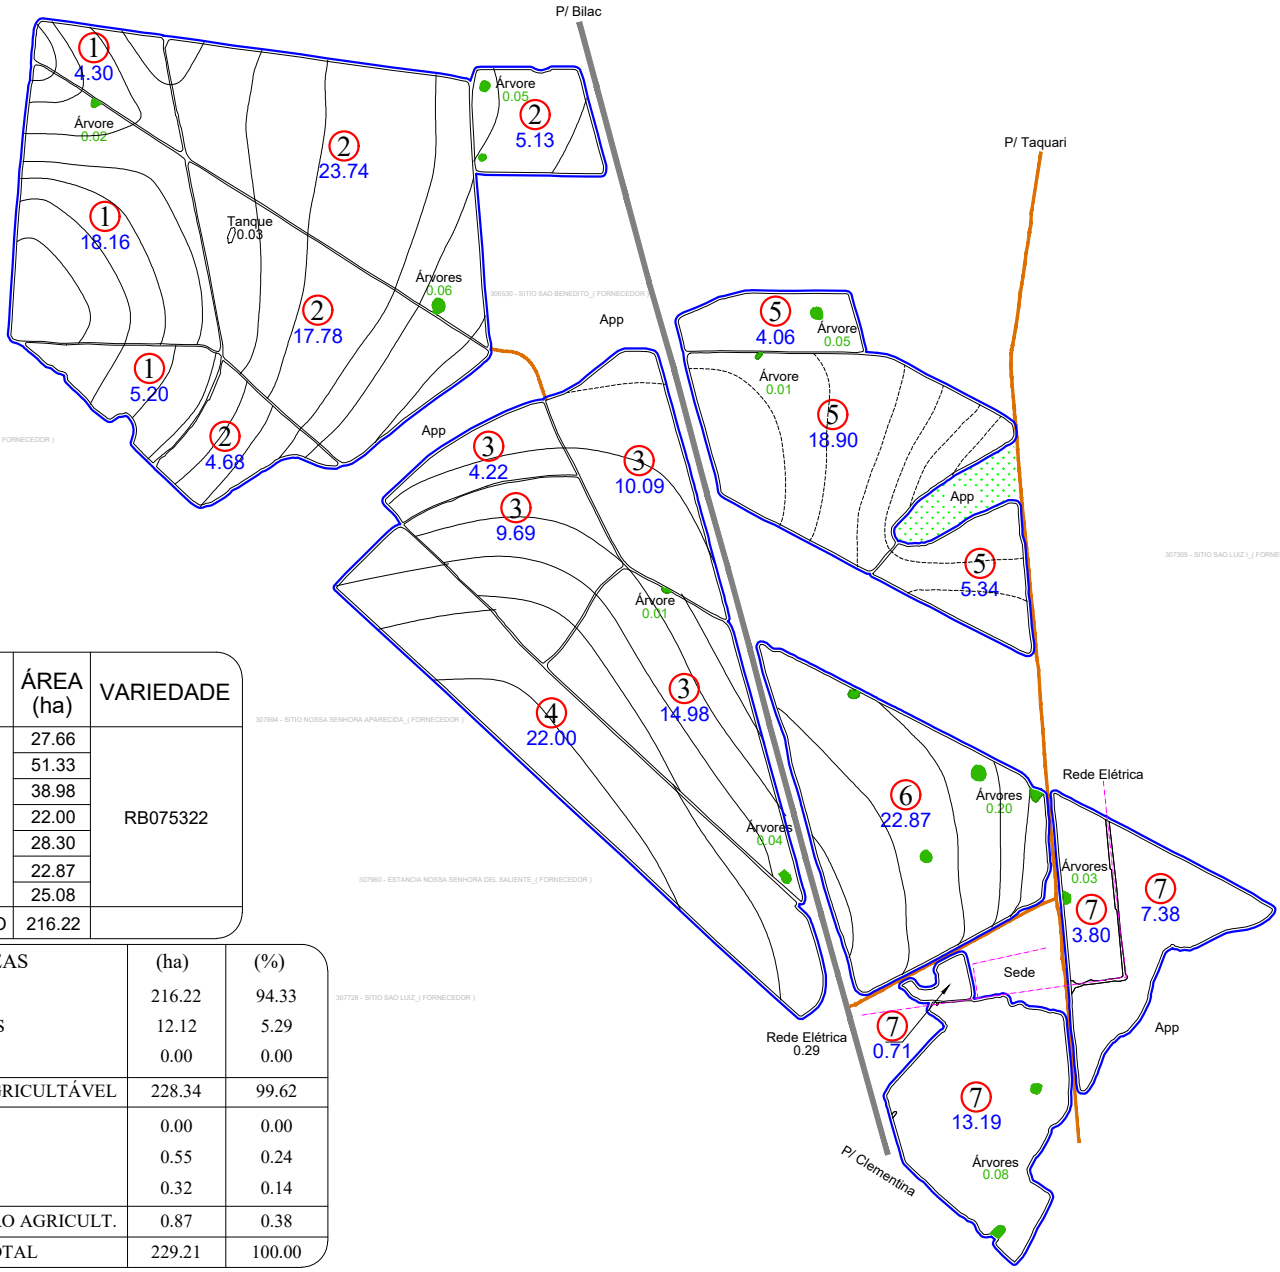

Nº TAL.	DATA PL.	ÁREA (ha)	VARIEDADE
1	04/2025	27.66	RB075322
2		51.33	
3		38.98	
4		22.00	
5		28.30	
6		22.87	
7		25.08	
TOTAL PLANTIO		216.22	

ÁREAS	(ha)	(%)
PLANTIO	216.22	94.33
CARREADORES	12.12	5.29
OUTROS	0.00	0.00
SUB TOTAL AGRICULTÁVEL	228.34	99.62
AP.P.	0.00	0.00
ÁRVORES	0.55	0.24
OUTROS	0.32	0.14
SUB TOTAL NÃO AGRICULT.	0.87	0.38
ÁREA TOTAL	229.21	100.00

C. NÍVEL: 15610.07 m/l 3.59 ha 1.57 %


LEGENDA

- FAZENDA
- TALHÃO
- REDE ELÉTRICA
- TERRAÇO BASE LARGA
- TERRAÇO EMBUTIDO
- (P.O.A) PATIO DE OPERAÇÃO

ESPAÇAMENTO: 1.50 x 1.50
TIRO MÉDIO ESTIMADO: 359.72 m
D.V: 3.65 %

ESCALA: 1: 16.000

CROQUI DE ACESSO

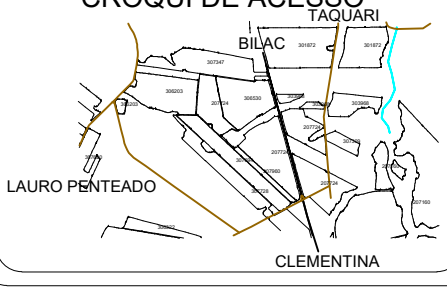

SÍTIO SÃO BENEDITO

PROPRIETÁRIO: RODOLFO SERISAVA PITTA
COMPRADOR: CLEALCO
MUNICÍPIO: BILAC - SP

DISTÂNCIAS (km):
UNID. I - Asfalto: 20.00 Terra.: 0.00
UNID.I I - Asfalto: 75.50 Terra.: 0.00

COORDENADAS: E(X): 558369.40 N(Y): 7628464.74
LAT: -21°26'43.0426" LONG: -50°26'12.0853"

CLEALCO - AÇÚCAR E ALCOOL S/A - DEPARTAMENTO DE GEOTECNOLOGIA

LEVANTAMENTO VIA:
- SATÉLITE
- GPS / VANT
- GOOGLE

UNIDADE: I
PARTE: A/A
FUNDO AGRÍCOLA: 307724

M:\01-Mapa de safra\Mapas Atualizados\Terceiro\307724 - Sítio São Benedito (Rodolfo Serisava Pitta)\307724 - Sítio São Benedito (Rodolfo Serisava Pitta).dwg

Benati 10/09/2025