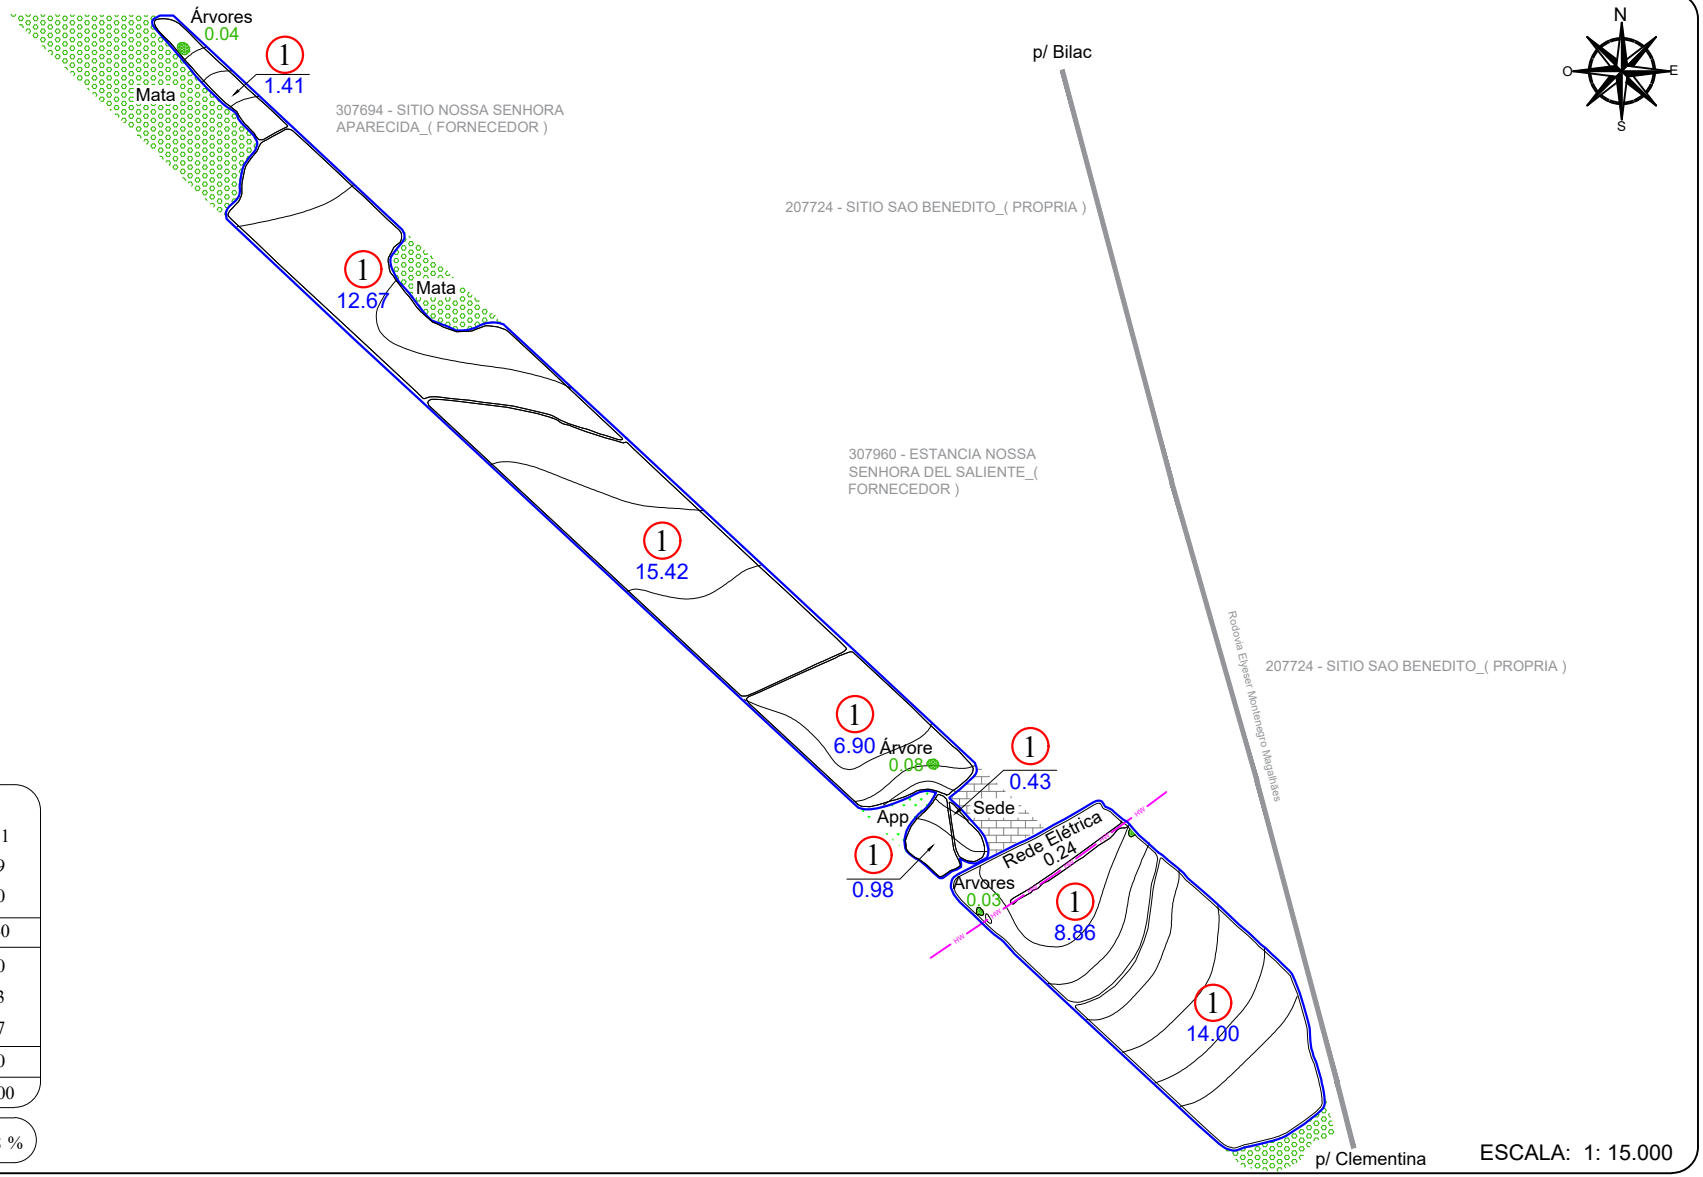


Nº TAL.	DATA PL.	ÁREA (ha)	VARIEDADE
1	04/2025	60.67	CTC 04
TOTAL PLANTIO		60.67	

ÁREAS	(ha)	(%)
PLANTIO	60.67	93.31
CARREADORES	3.96	6.09
OUTROS	0.00	0.00
SUB TOTAL AGRICULTÁVEL	64.63	99.40
AP.P.	0.00	0.00
ÁRVORES	0.15	0.23
OUTROS	0.24	0.37
SUB TOTAL NÃO AGRICULT.	0.39	0.60
ÁREA TOTAL	65.02	100.00


C. NÍVEL:	5025.88 m/l	1.16 ha	1.78 %

LEGENDA

- FAZENDA
- TALHÃO
- REDE ELÉTRICA
- TERRAÇO BASE LARGA
- TERRAÇO EMBUTIDO

ESPAÇAMENTO:	1.50 x 1.50	D.V: 0.00 %
TIRO MÉDIO ESTIMADO:	212.48 m	

CROQUI DE ACESSO

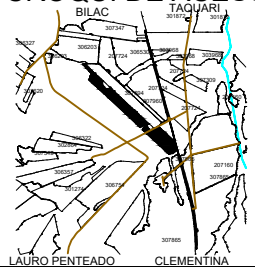

SÍTIO SÃO LUIZ

PROPRIETÁRIO: RODOLFO SERISAVA PITTA
COMPRADOR: CLEALCO
MUNICÍPIO: BILAC - SP

DISTÂNCIAS (km):
UNID. I - Asfalto: 16.00 Terra.: 0.00
UNID.I I - Asfalto: 70.00 Terra.: 0.00

COORDENADAS: E(X): 557061.82 N(Y): 7627904.50
LAT: -21°27'1.4154" LONG: -50°26'57.4444"

CLEALCO - AÇÚCAR E ALCOOL S/A - DEPARTAMENTO DE GEOTECNOLOGIA

LEVANTAMENTO VIA:
SATÉLITE
GPS / VANT
GOOGLE

UNIDADE: I

PARTE: A/A

FUNDO AGRÍCOLA: 307728

M:\01-Mapa de safra\Mapas Atualizados\Terceiro\307728 - Sitio Sao Luiz (Rodolfo Serisava Pitta)\307728 - Sitio Sao Luiz (Rodolfo Serisava Pitta).dwg

Benati 12/09/2025