
Clealco
Açúcar, Etanol e Energia

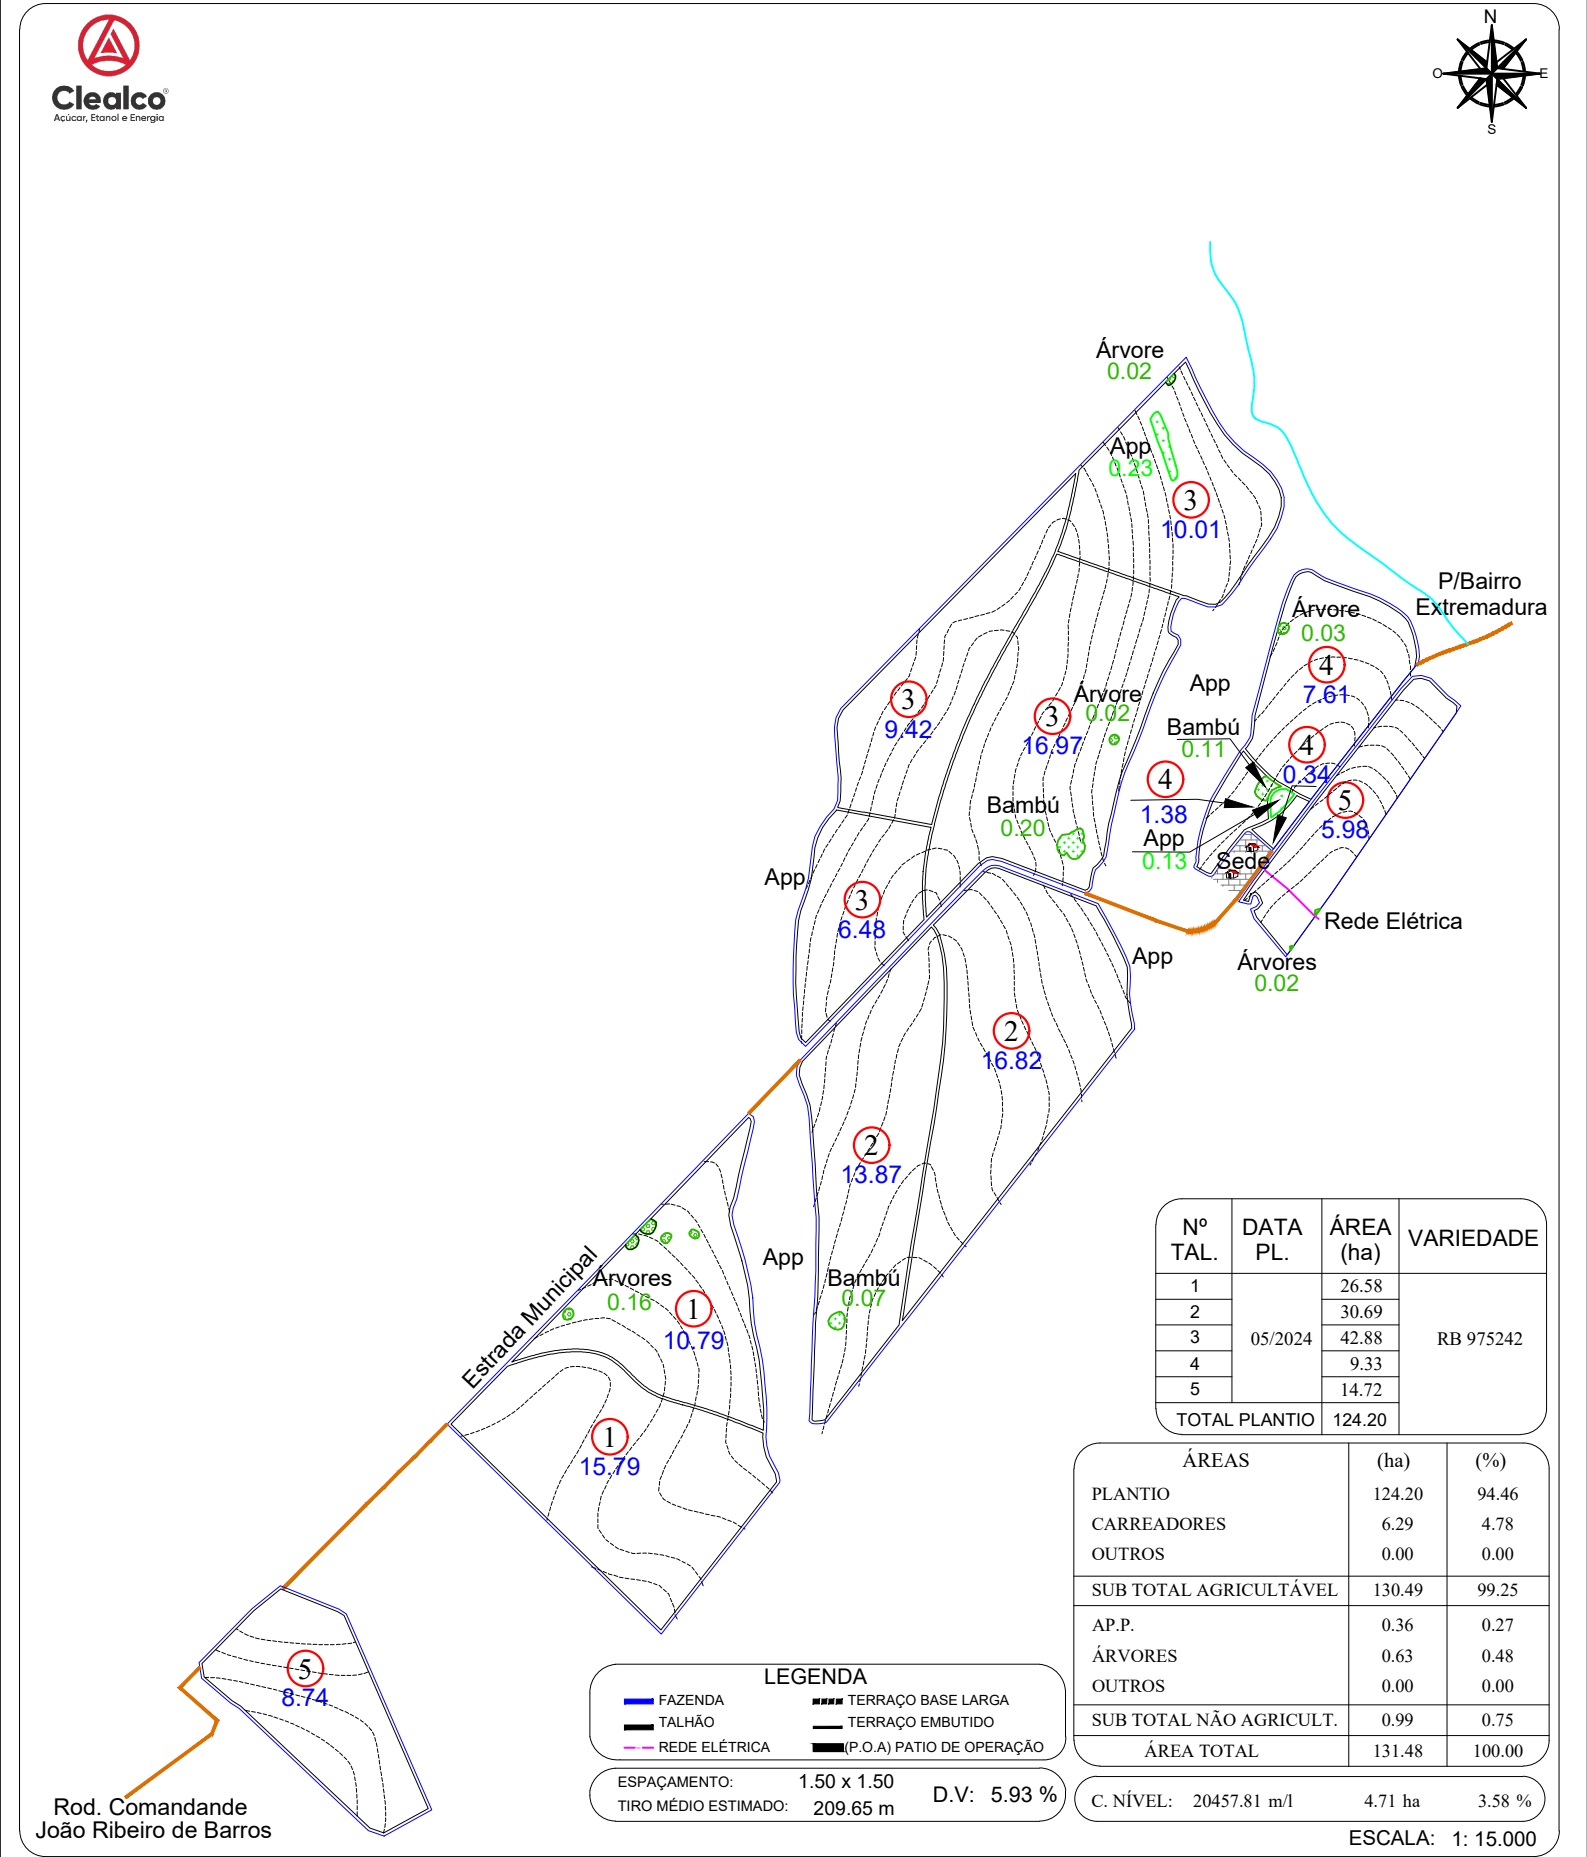

Nº TAL.	DATA PL.	ÁREA (ha)	VARIEDADE
1	05/2024	26.58	RB 975242
2		30.69	
3		42.88	
4		9.33	
5		14.72	
TOTAL PLANTIO		124.20	

ÁREAS	(ha)	(%)
PLANTIO	124.20	94.46
CARREADORES	6.29	4.78
OUTROS	0.00	0.00
SUB TOTAL AGRICULTÁVEL	130.49	99.25
AP.P.	0.36	0.27
ÁRVORES	0.63	0.48
OUTROS	0.00	0.00
SUB TOTAL NÃO AGRICULT.	0.99	0.75
ÁREA TOTAL	131.48	100.00

LEGENDA


- FAZENDA
- TALHÃO
- REDE ELÉTRICA
- TERRAÇO BASE LARGA
- TERRAÇO EMBUTIDO
- (P.O.A) PATIO DE OPERAÇÃO

ESPAÇAMENTO: 1.50 x 1.50
TIRO MÉDIO ESTIMADO: 209.65 m
D.V: 5.93 %

C. NÍVEL: 20457.81 m/l 4.71 ha 3.58 %

ESCALA: 1: 15.000

CROQUI DE ACESSO

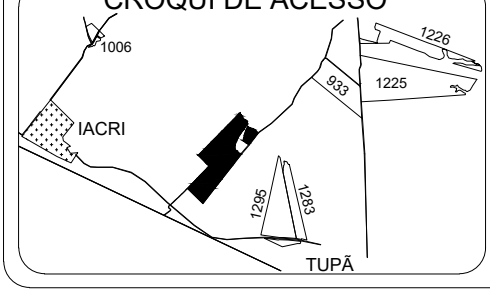

FAZENDA SANTA MARIA

PROPRIETÁRIO: CLAUDEMIR STEFANELLI
COMPRADOR: CLEALCO
MUNICÍPIO: IACRI - SP

DISTÂNCIAS (km):
UNID. I - Asfalto: 37.50 Terra.: 12.00
UNID.I I - Asfalto: 71.00 Terra.: 12.00

COORDENADAS: E(X): 536064.85 N(Y): 7581451.78
LAT: -21°52'14.2574" LONG: -50°39'3.3200"

CLEALCO - AÇÚCAR E ALCOOL S/A - DEPARTAMENTO DE GEOTECNOLOGIA

LEVANTAMENTO VIA:
SATÉLITE
GPS / VANT
GOOGLE

UNIDADE: II
PARTE: A/A
FUNDO AGRÍCOLA: 307729

M:\01-Mapa de safra\Mapas Atualizados\Terceiro\307729 - Fazenda Santa Maria (Claudemir Stefanelli)\307729 - Fazenda Santa Maria (Claudemir Stefanelli).dwg

Bruno Gamboa 25/07/25