D.V.	Nº TAL.	DATA PL.	ÁREA (ha)	VARIEDADE
4.10 %	1	04/2024	25.15	CTC-9001
	2		21.78	
TOTAL PLANTIO			46.93	--------


ÁREAS	(ha)	(%)
PLANTIO	46.93	96.24
CARREADORES	1.47	3.02
OUTROS	0.13	0.27
SUB TOTAL AGRICULTÁVEL	48.53	99.53
AP.P.	0.00	0.00
ÁRVORES	0.23	0.47
OUTROS	0.00	0.00
SUB TOTAL NÃO AGRICULT.	0.23	0.47
ÁREA TOTAL	48.76	100.00

C. NÍVEL: 2670.32 m/l 0.61 ha 1.26 %


LEGENDA

- FAZENDA
- TALHÃO
- CURVA DE NÍVEL
- CARREADOR
- CONFRONTANTE
- REDE ELÉTRICA
- TRAJETO VAZIO
- TRAJETO CARREGADO

PLANTIO MANUAL - ESPAÇAMENTO: 1.50 X 1.50
TIRO MÉDIO ESTIMADO: 359.43 m

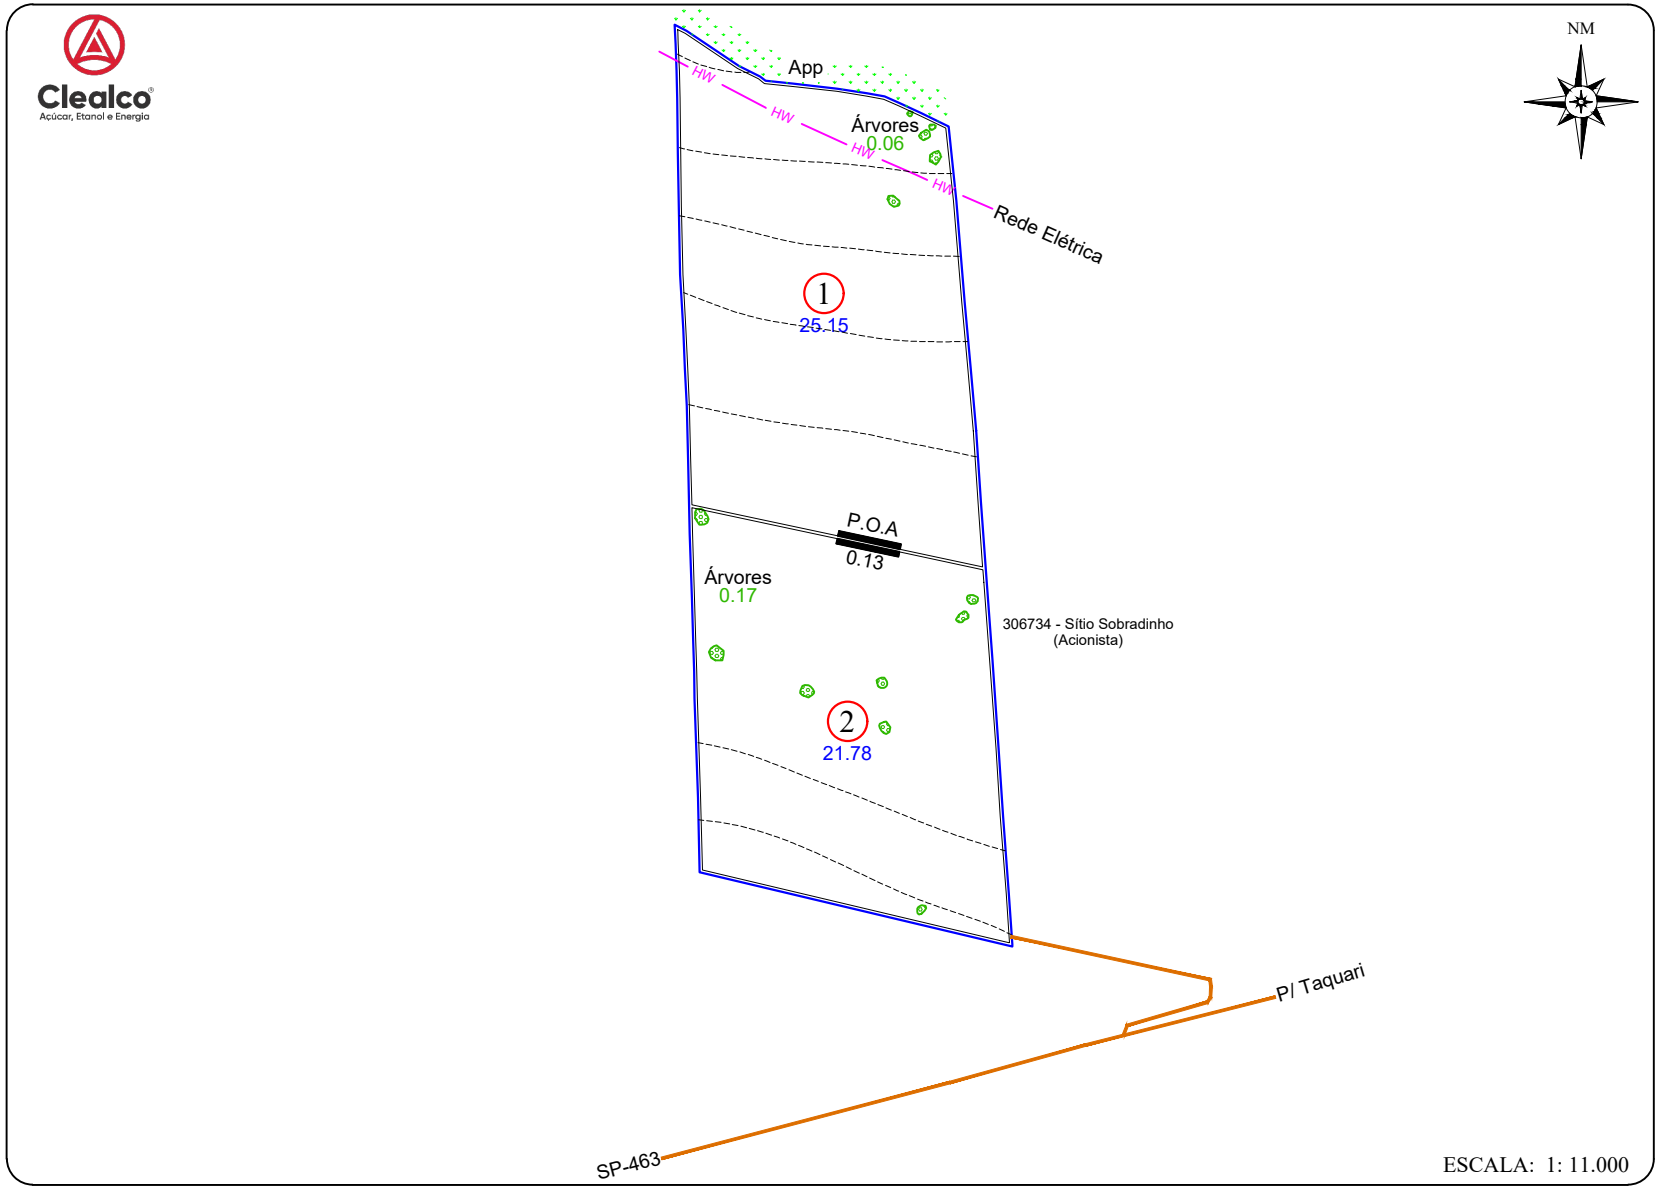

CROQUI DE ACESSO

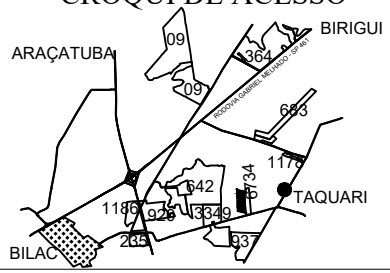

SÍTIO 3 M

PROPRIETÁRIO: JORGE LUIZ ZAGO
COMPRADOR: CLEALCO S/A
MUNICÍPIO: BIRIGUI

DISTÂNCIAS (km):
UNID. I - Asfalto: 31.00 Terra.: 3.57
UNID.I I - Asfalto: 77.50 Terra.: 3.57
UNID. III -Asfalto: 42.00 Terra.: 3.57

COORDENADAS: E(X): 559605.70 N(Y): 7634913.35
LAT: -21°23'13.1549" LONG: -50°25'29.9554"

CLEALCO - AÇÚCAR E ALCOOL S/A - DEPARTAMENTO DE TOPOGRAFIA

UNIDADE: I
PARTE: A/A
FUNDO AGRÍCOLA: 307734

M:\01-Mapa de safra\Mapas Atualizados\Terceiro\307734 - Sítio 3M (Jorge Luiz Zago)\307734 - Sítio 3M (Jorge Luiz Zago).dwg

Peterson Santos 15/01/2025