D.V.	Nº TAL.	DATA PL.	ÁREA (ha)	VARIEDADE
2.67%	1	06/2024	69.41	RB975201
	2		54.09	
TOTAL PLANTIO			123.50	

ÁREAS	(ha)	(%)
PLANTIO	123.50	97.35
CARREADORES	3.26	2.57
OUTROS	0.00	0.00
SUB TOTAL AGRICULTÁVEL	126.76	99.92
AP.P.	0.00	0.00
ÁRVORES	0.10	0.08
OUTROS	0.00	0.00
SUB TOTAL NÃO AGRICULT.	0.10	0.08
ÁREA TOTAL	126.86	100.00


C. NÍVEL: 0.00 m/l 0.00 ha 0.00 %

LEGENDA

- FAZENDA
- TALHÃO
- REDE ELÉTRICA
- TERRAÇO BASE LARGA
- TERRAÇO EMBUTIDO


ESPAÇAMENTO: 1.50 x 1.50

TIRO MÉDIO ESTIMADO: 411.97 m

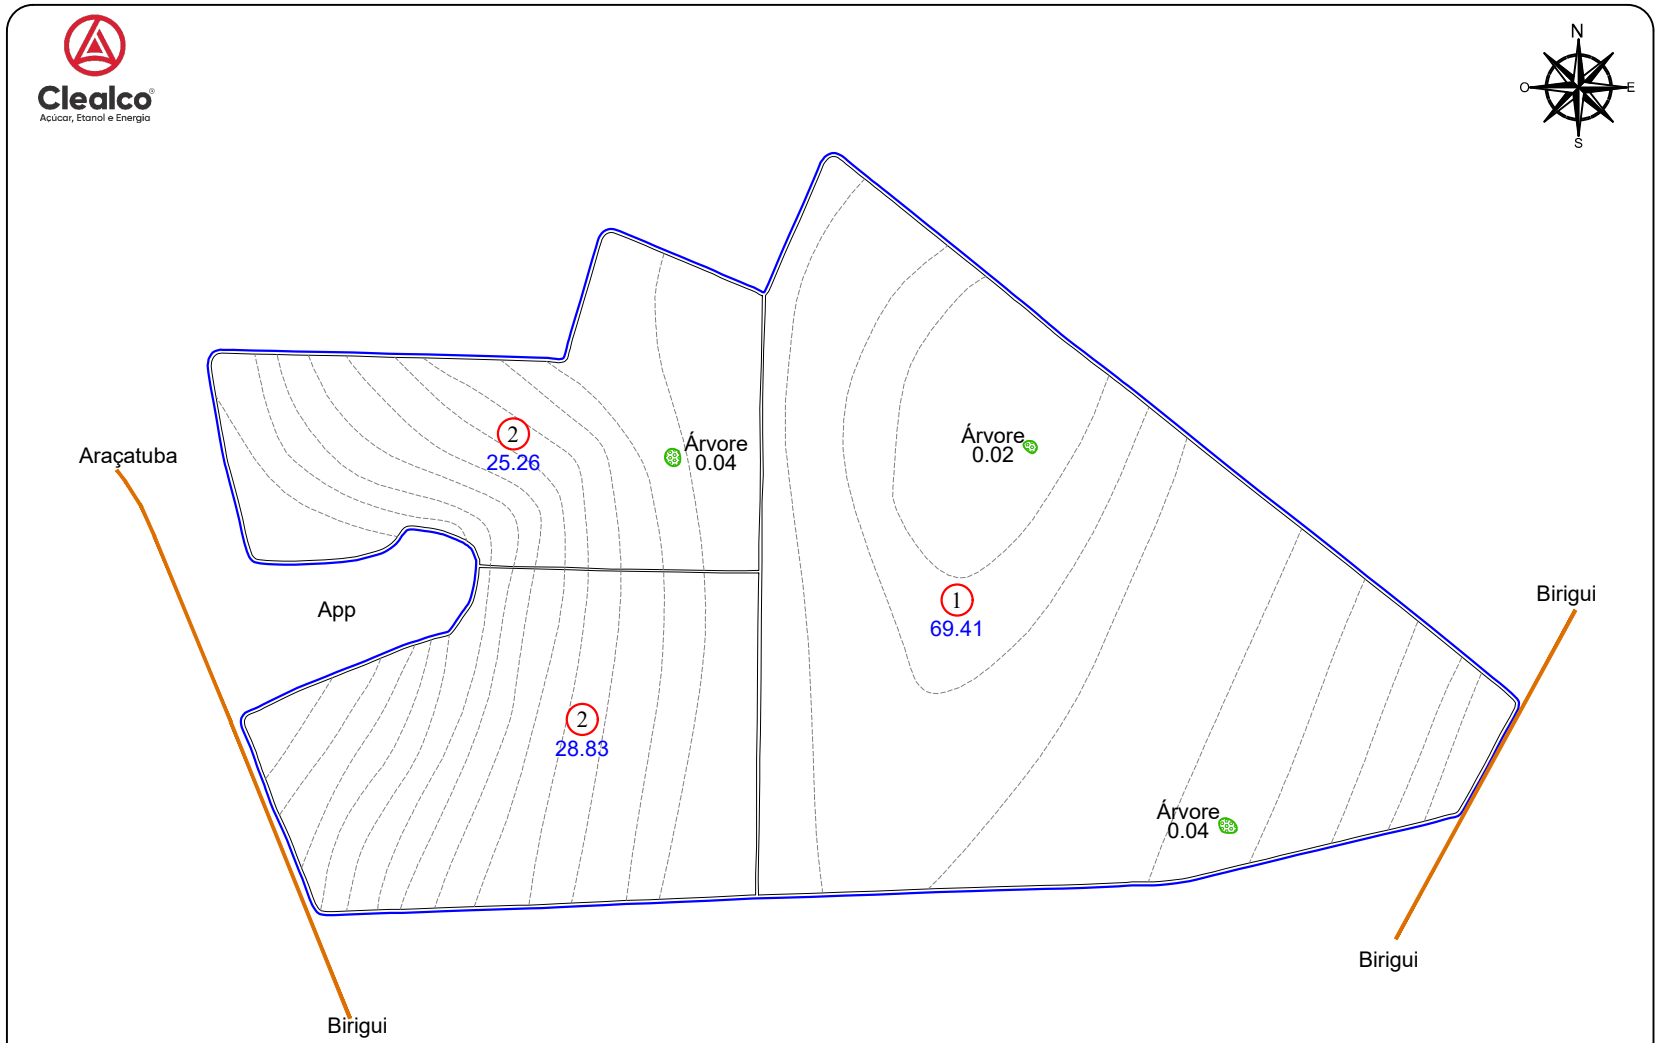

ESCALA: 1: 11.000

CROQUI DE ACESSO

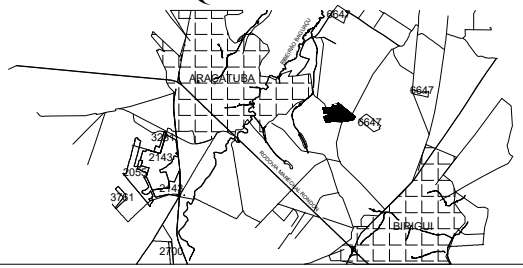

FAZENDA ESPERANÇA

PROPRIETÁRIO: JORGE LUIZ ZAGO
COMPRADOR: CLEALCO S/A
MUNICÍPIO: ARAÇATUBA

DISTÂNCIAS (km):
UNID. I - Asfalto: 44.00 Terra.: 6.80
UNID.I I - Asfalto: 93.45 Terra.: 10.25
UNID. III -Asfalto: 46.55 Terra.: 10.25

COORDENADAS: E(X): 563990.36 N(Y): 7653336.34
LAT: -21°13'13.4010" LONG: -50°23'0.1889"

CLEALCO - AÇÚCAR E ALCOOL S/A - DEPARTAMENTO DE TOPOGRAFIA

UNIDADE: I

PARTE: A/A

FUNDO AGRÍCOLA: 307735

Fabiano Castro 16/04/25