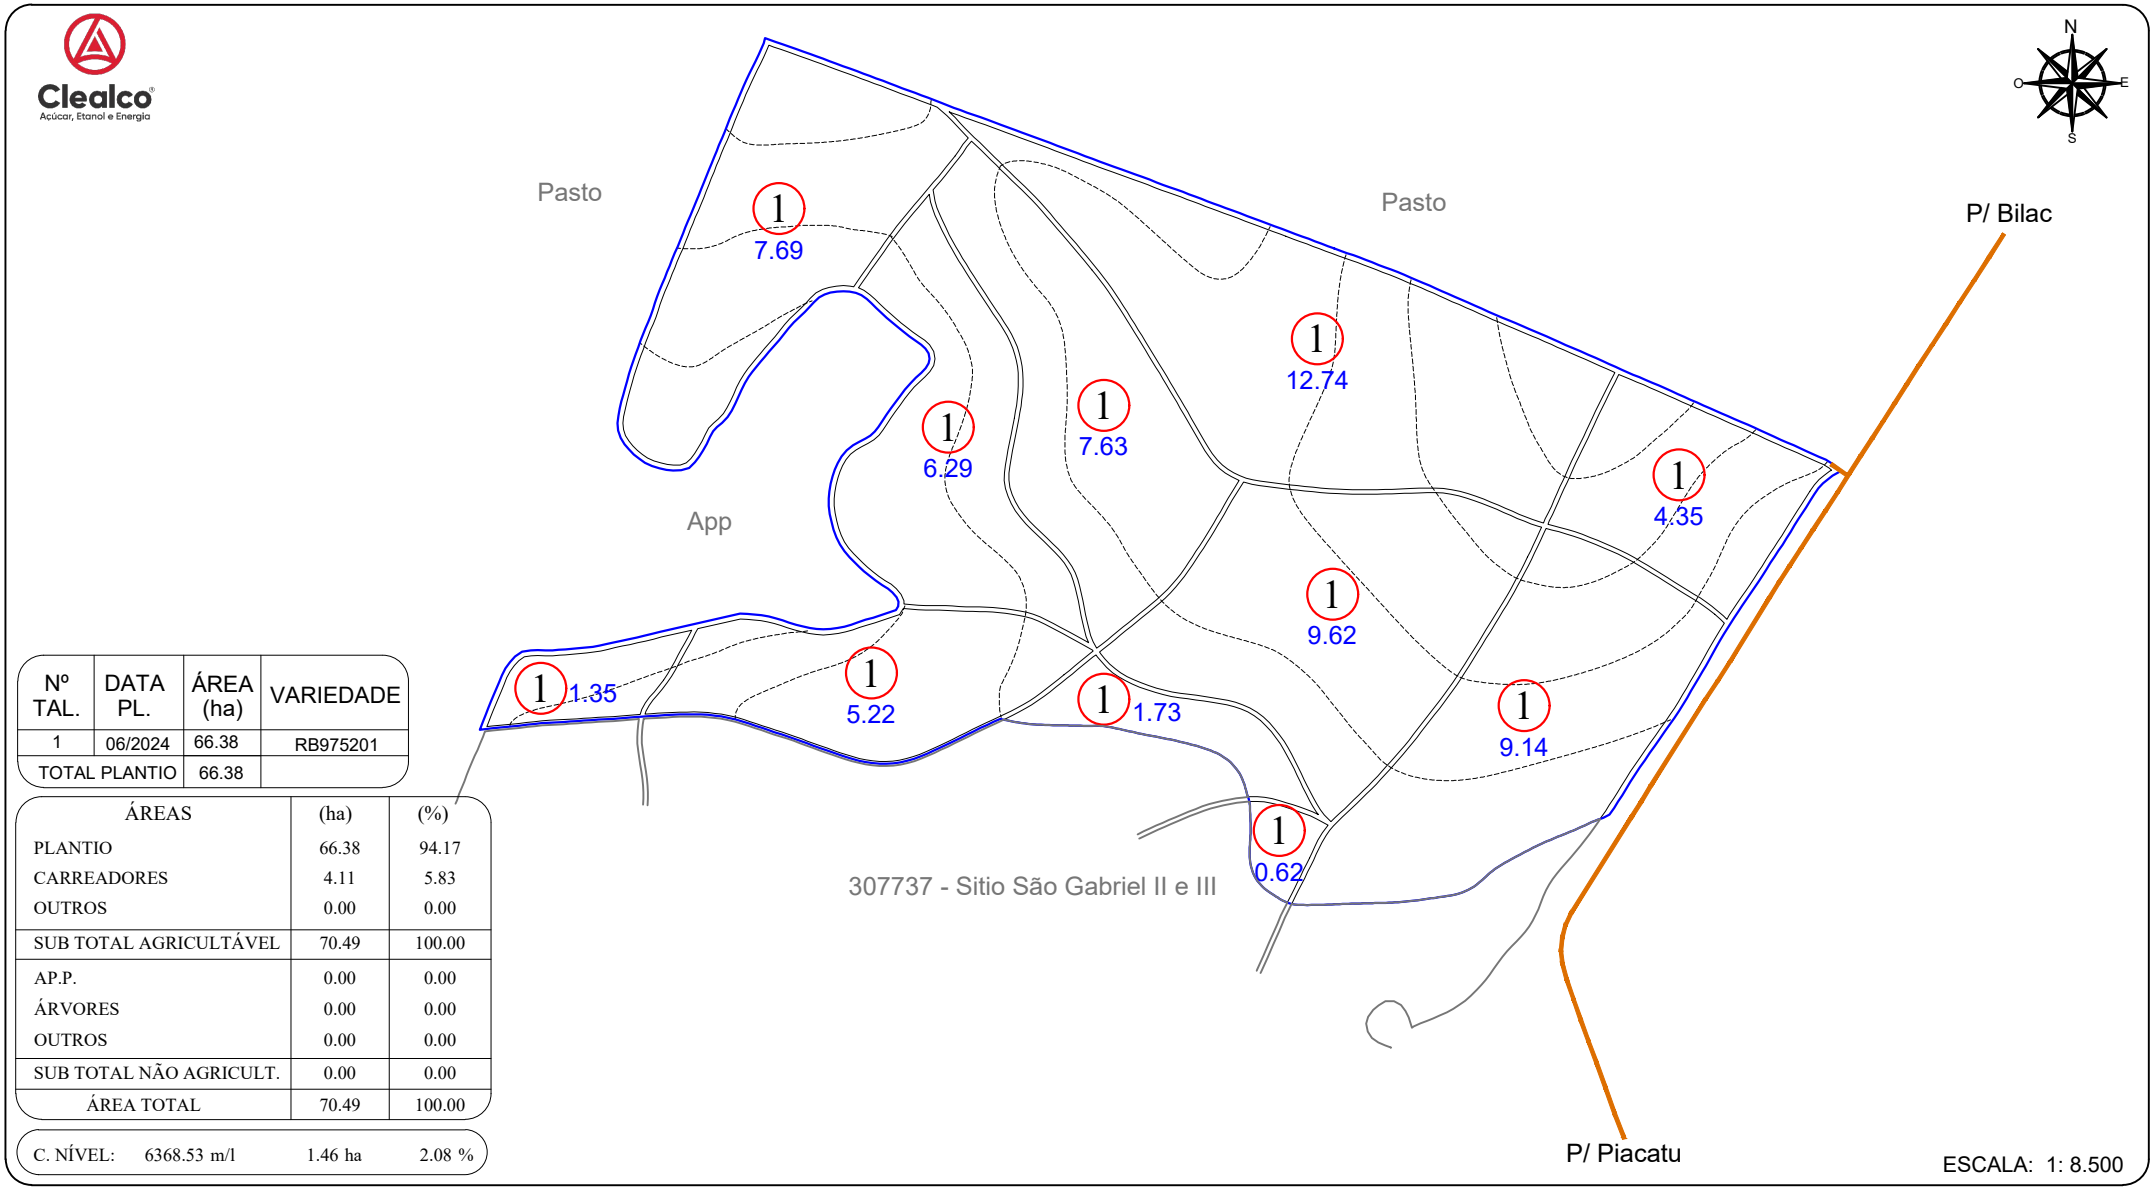


Nº TAL.	DATA PL.	ÁREA (ha)	VARIEDADE
1	06/2024	66.38	RB975201
TOTAL PLANTIO		66.38	

ÁREAS	(ha)	(%)
PLANTIO	66.38	94.17
CARREADORES	4.11	5.83
OUTROS	0.00	0.00
SUB TOTAL AGRICULTÁVEL	70.49	100.00
AP.P.	0.00	0.00
ÁRVORES	0.00	0.00
OUTROS	0.00	0.00
SUB TOTAL NÃO AGRICULT.	0.00	0.00
ÁREA TOTAL	70.49	100.00

C. NÍVEL: 6368.53 m/l 1.46 ha 2.08 %


ESCALA: 1: 8.500

LEGENDA

- FAZENDA
- TALHÃO
- REDE ELÉTRICA
- TERRAÇO BASE LARGA
- TERRAÇO EMBUTIDO

ESPAÇAMENTO: 1.50 x 1.50
TIRO MÉDIO ESTIMADO: 253.05 m
D.V: - %

CROQUI DE ACESSO

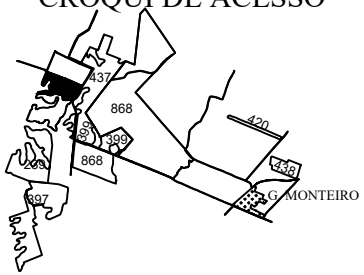

FAZENDA SÃO GABRIEL

PROPRIETÁRIO: JOÃO LOPES
COMPRADOR: CLEALCO
MUNICÍPIO: GABRIEL MONTEIRO - SP

DISTÂNCIAS (km):
UNID. I - Asfalto: 22.90 Terra.: 13.10
UNID.I I - Asfalto: 59.30 Terra.: 13.10

COORDENADAS: E(X): 539964.28 N(Y): 7623003.83
LAT: -21°29'42.4754" LONG: -50°36'51.0489"
CLEALCO - AÇÚCAR E ALCOOL S/A - DEPARTAMENTO DE GEOTECNOLOGIA

LEVANTAMENTO VIA:
SATÉLITE
GPS / VANT
GOOGLE

UNIDADE: I
PARTE: A/A
FUNDO AGRÍCOLA: 307736

M:\01-Mapa de safra\Mapas Atualizados\Terceiro\307736 - Fazenda São Gabriel (Joao Lopes)\307736 - Fazenda São Gabriel (Joao Lopes).dwg

Peterson Santos 15/01/25