| D.V. | Nº TAL. | DATA PL. | ÁREA (ha) | VARIEDADE |
|---|---|---|---|---|
| 5.63 % | 1 | 04/2024 | 14.76 | RB97 5201 |
| | 2 | | 23.55 | |
| | 3 | | 6.75 | |
| TOTAL PLANTIO | | | 45.06 | -------- |


| ÁREAS | (ha) | (%) |
|---|---|---|
| PLANTIO | 45.06 | 93.27 |
| CARREADORES | 3.25 | 6.73 |
| OUTROS | 0.00 | 0.00 |
| SUB TOTAL AGRICULTÁVEL | 48.31 | 100.00 |
| AP.P. | 0.00 | 0.00 |
| ÁRVORES | 0.00 | 0.00 |
| OUTROS | 0.00 | 0.00 |
| SUB TOTAL NÃO AGRICULT. | 0.00 | 0.00 |
| ÁREA TOTAL | 48.31 | 100.00 |

C. NÍVEL: 5682.82 m/l 1.31 ha 2.71 %


LEGENDA

- FAZENDA
- TALHÃO
- CURVA DE NÍVEL
- CARREADOR
- CONFRONTANTE
- REDE ELÉTRICA

PLANTIO MANUAL - ESPAÇAMENTO: 1.50 X 1.50
TIRO MÉDIO ESTIMADO: 290.79 m

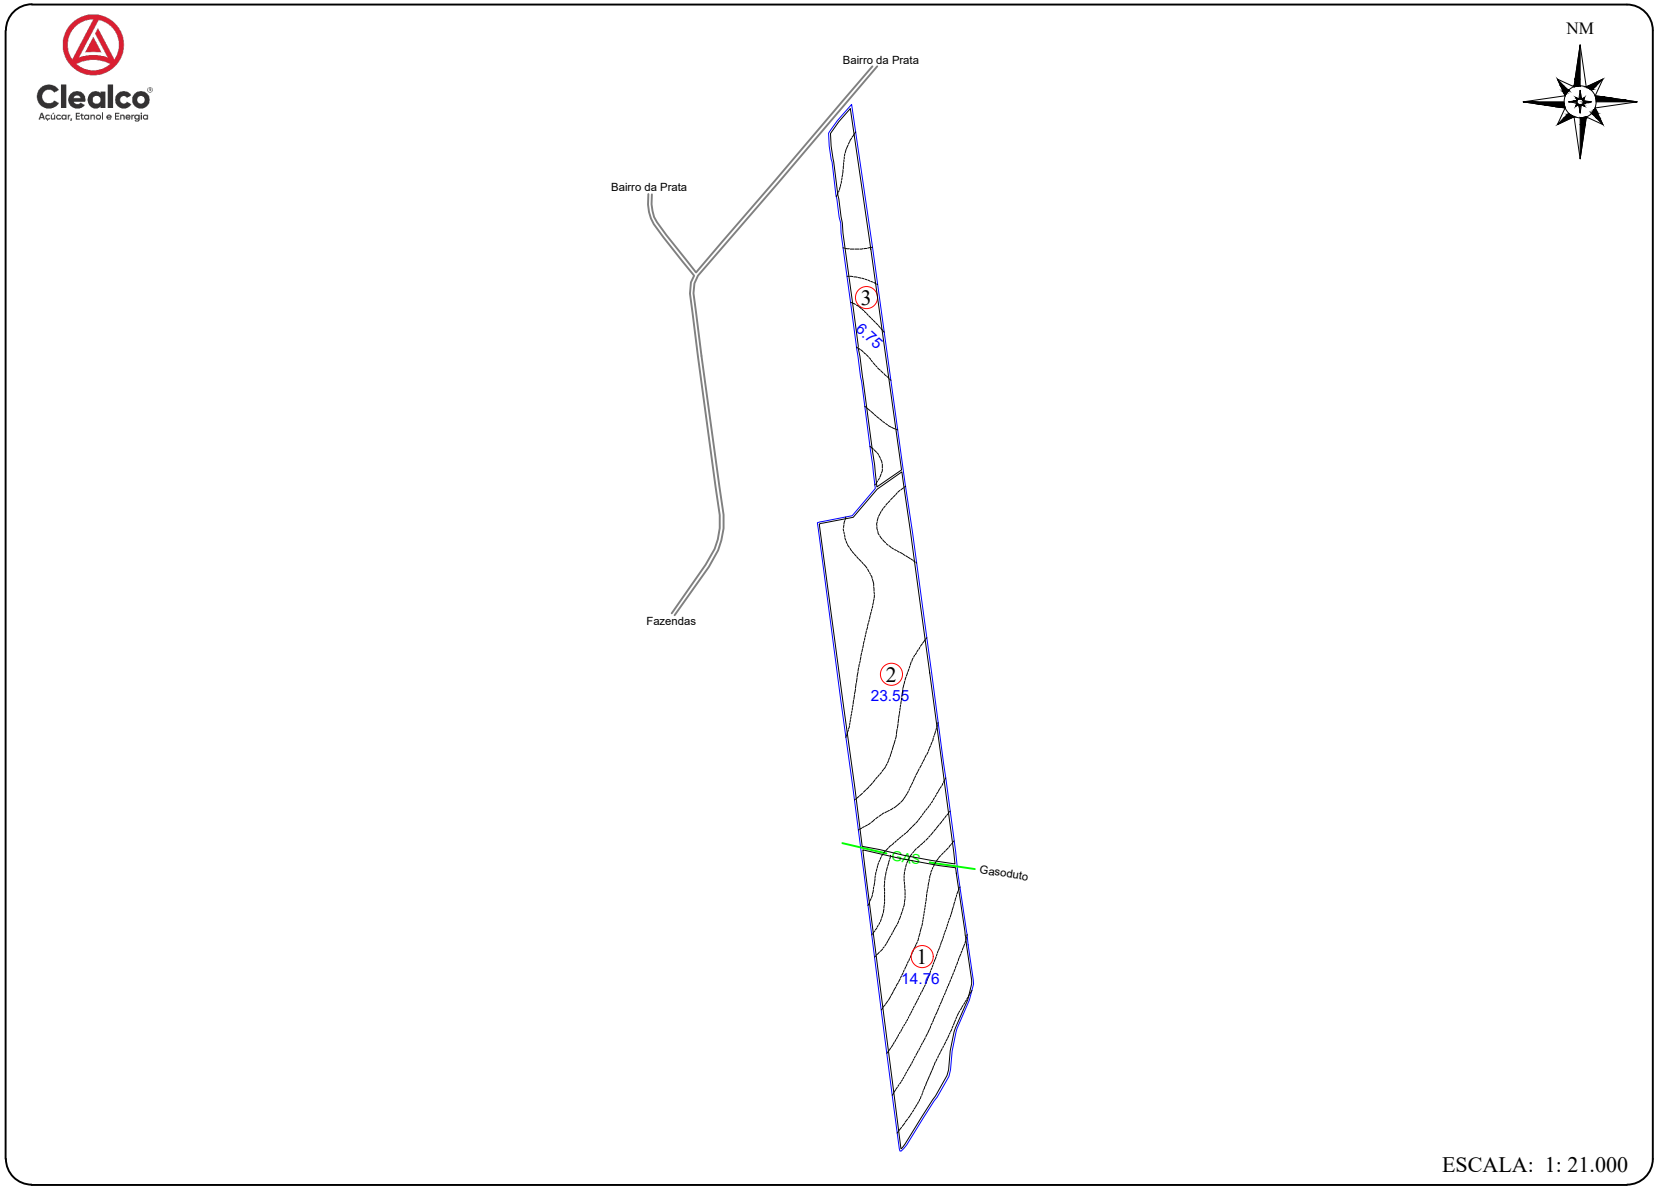


CROQUI DE ACESSO

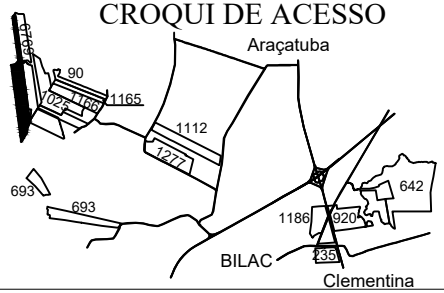


# SÍTIO 3R

PROPRIETÁRIO: LUIZ CARLOS GENARI
COMPRADOR: CLEALCO S/A
MUNICÍPIO: ARAÇATUBA

DISTÂNCIAS (km):
UNIDADE I - 33.20
UNIDADE I I - 91.00

COORDENADAS: E(X): 548787.01 N(Y): 7637902.95
LAT: -21°21'37.0867" LONG: -50°31'45.9774"

CLEALCO - AÇÚCAR E ALCOOL S/A - DEPARTAMENTO DE TOPOGRAFIA

UNIDADE: I
PARTE: A/A
FUNDO AGRÍCOLA: 307740