D.V.	Nº TAL.	DATA PL.	ÁREA (ha)	VARIEDADE
3.34 %	1	05/2024	26.83	RB97 5242
	2		38.22	
	3		36.58	
TOTAL PLANTIO			101.63	--------

ÁREAS	(ha)	(%)
PLANTIO	101.63	97.02
CARREADORES	3.03	2.89
OUTROS	0.00	0.00
SUB TOTAL AGRICULTÁVEL	104.66	99.90
AP.P.	0.00	0.00
ÁRVORES	0.04	0.04
OUTROS	0.06	0.06
SUB TOTAL NÃO AGRICULT.	0.10	0.10
ÁREA TOTAL	104.76	100.00


C. NÍVEL: 8004.69 m/l 1.84 ha 1.76 %

LEGENDA


- FAZENDA
- TALHÃO
- REDE ELÉTRICA
- TERRAÇO BASE LARGA
- TERRAÇO EMBUTIDO

ESPAÇAMENTO: 0.00 x 0.00

TIRO MÉDIO ESTIMADO: 000.00 m

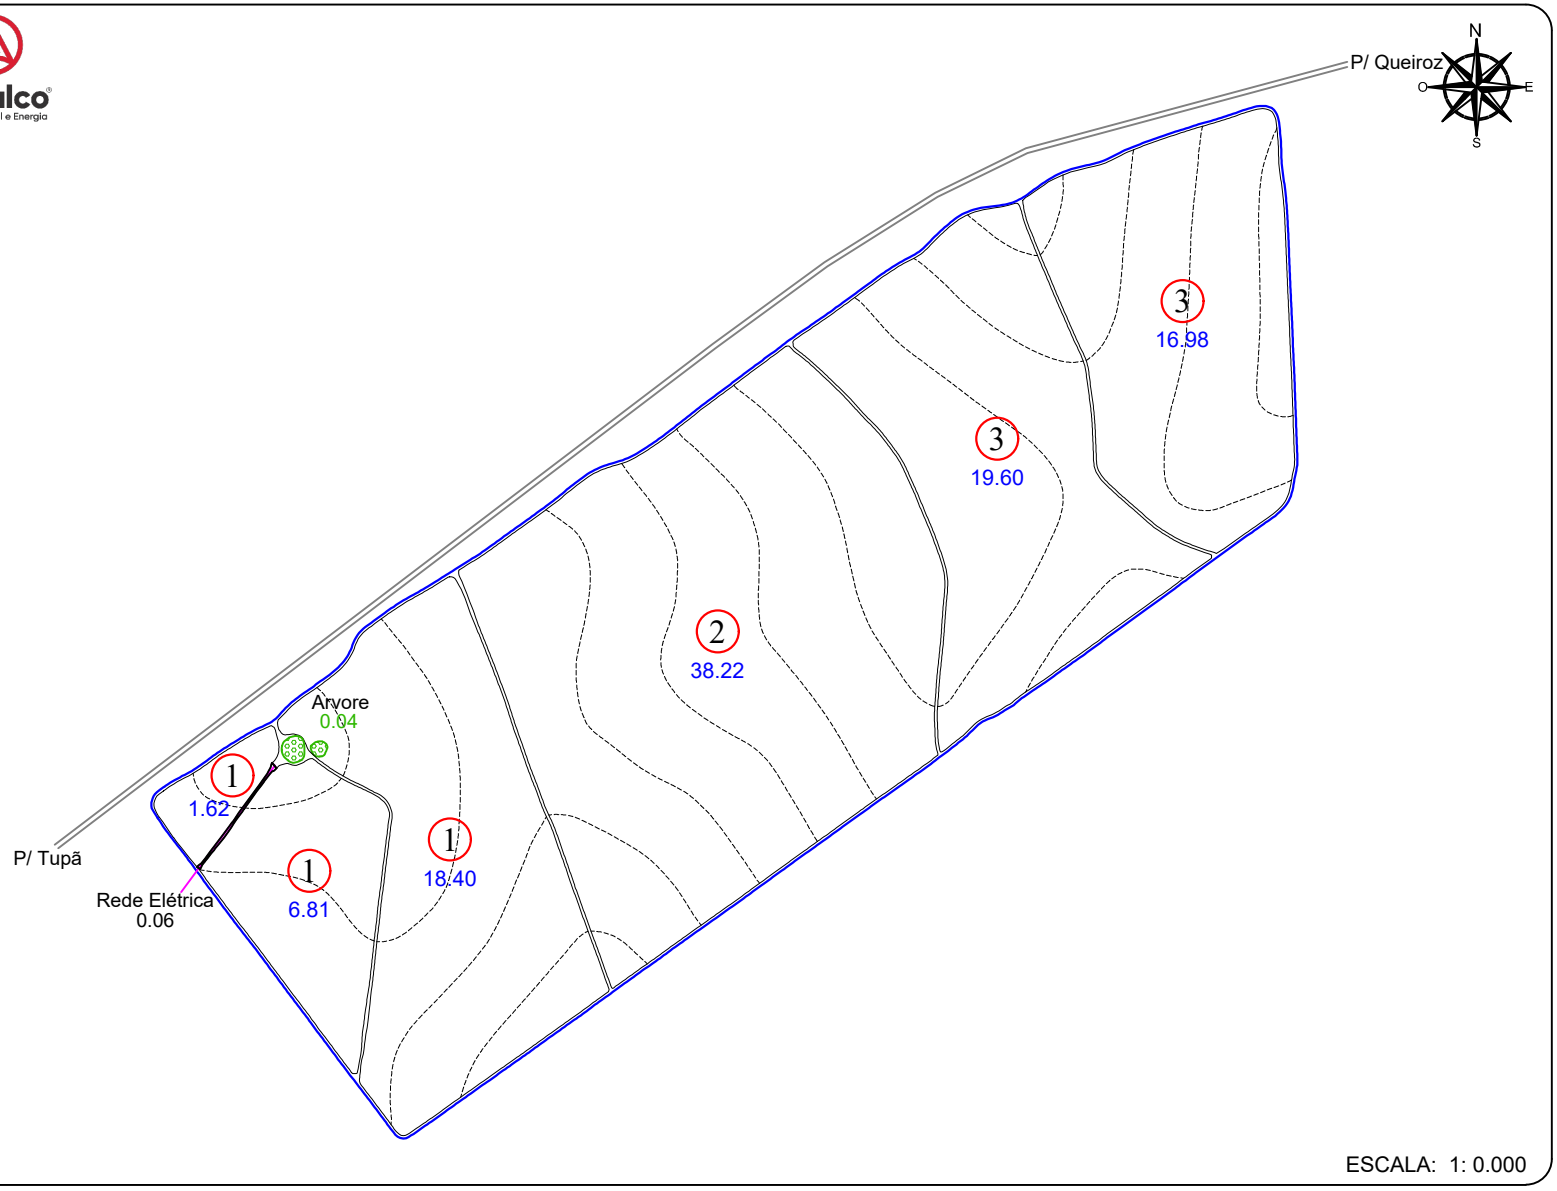

CROQUI DE ACESSO

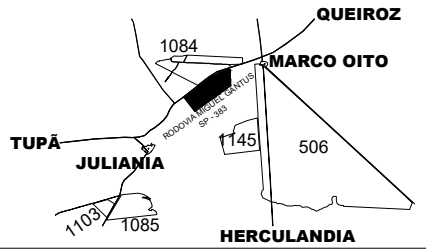

FAZENDA ELDORADO

PROPRIETÁRIO: JORGE LUÍZ GILBERTO
COMPRADOR: CLEALCO S/A
MUNICÍPIO: HERCULÂNDIA

DISTÂNCIAS (km):
UNID. I - Asfalto: 32.50 Terra.: 23.50
UNID.I I - Asfalto: 16.70 Terra.: 2.10
UNID. III -Asfalto: 71.00 Terra.: 2.10

COORDENADAS: E(X): 567645.49 N(Y): 7580020.21
LAT: -21°52'57.4643" LONG: -50°20'42.7222"

CLEALCO - AÇÚCAR E ALCOOL S/A - DEPARTAMENTO DE GEOTECNOLOGIA

UNIDADE: II

PARTE: A/A

FUNDO AGRÍCOLA: 307743